


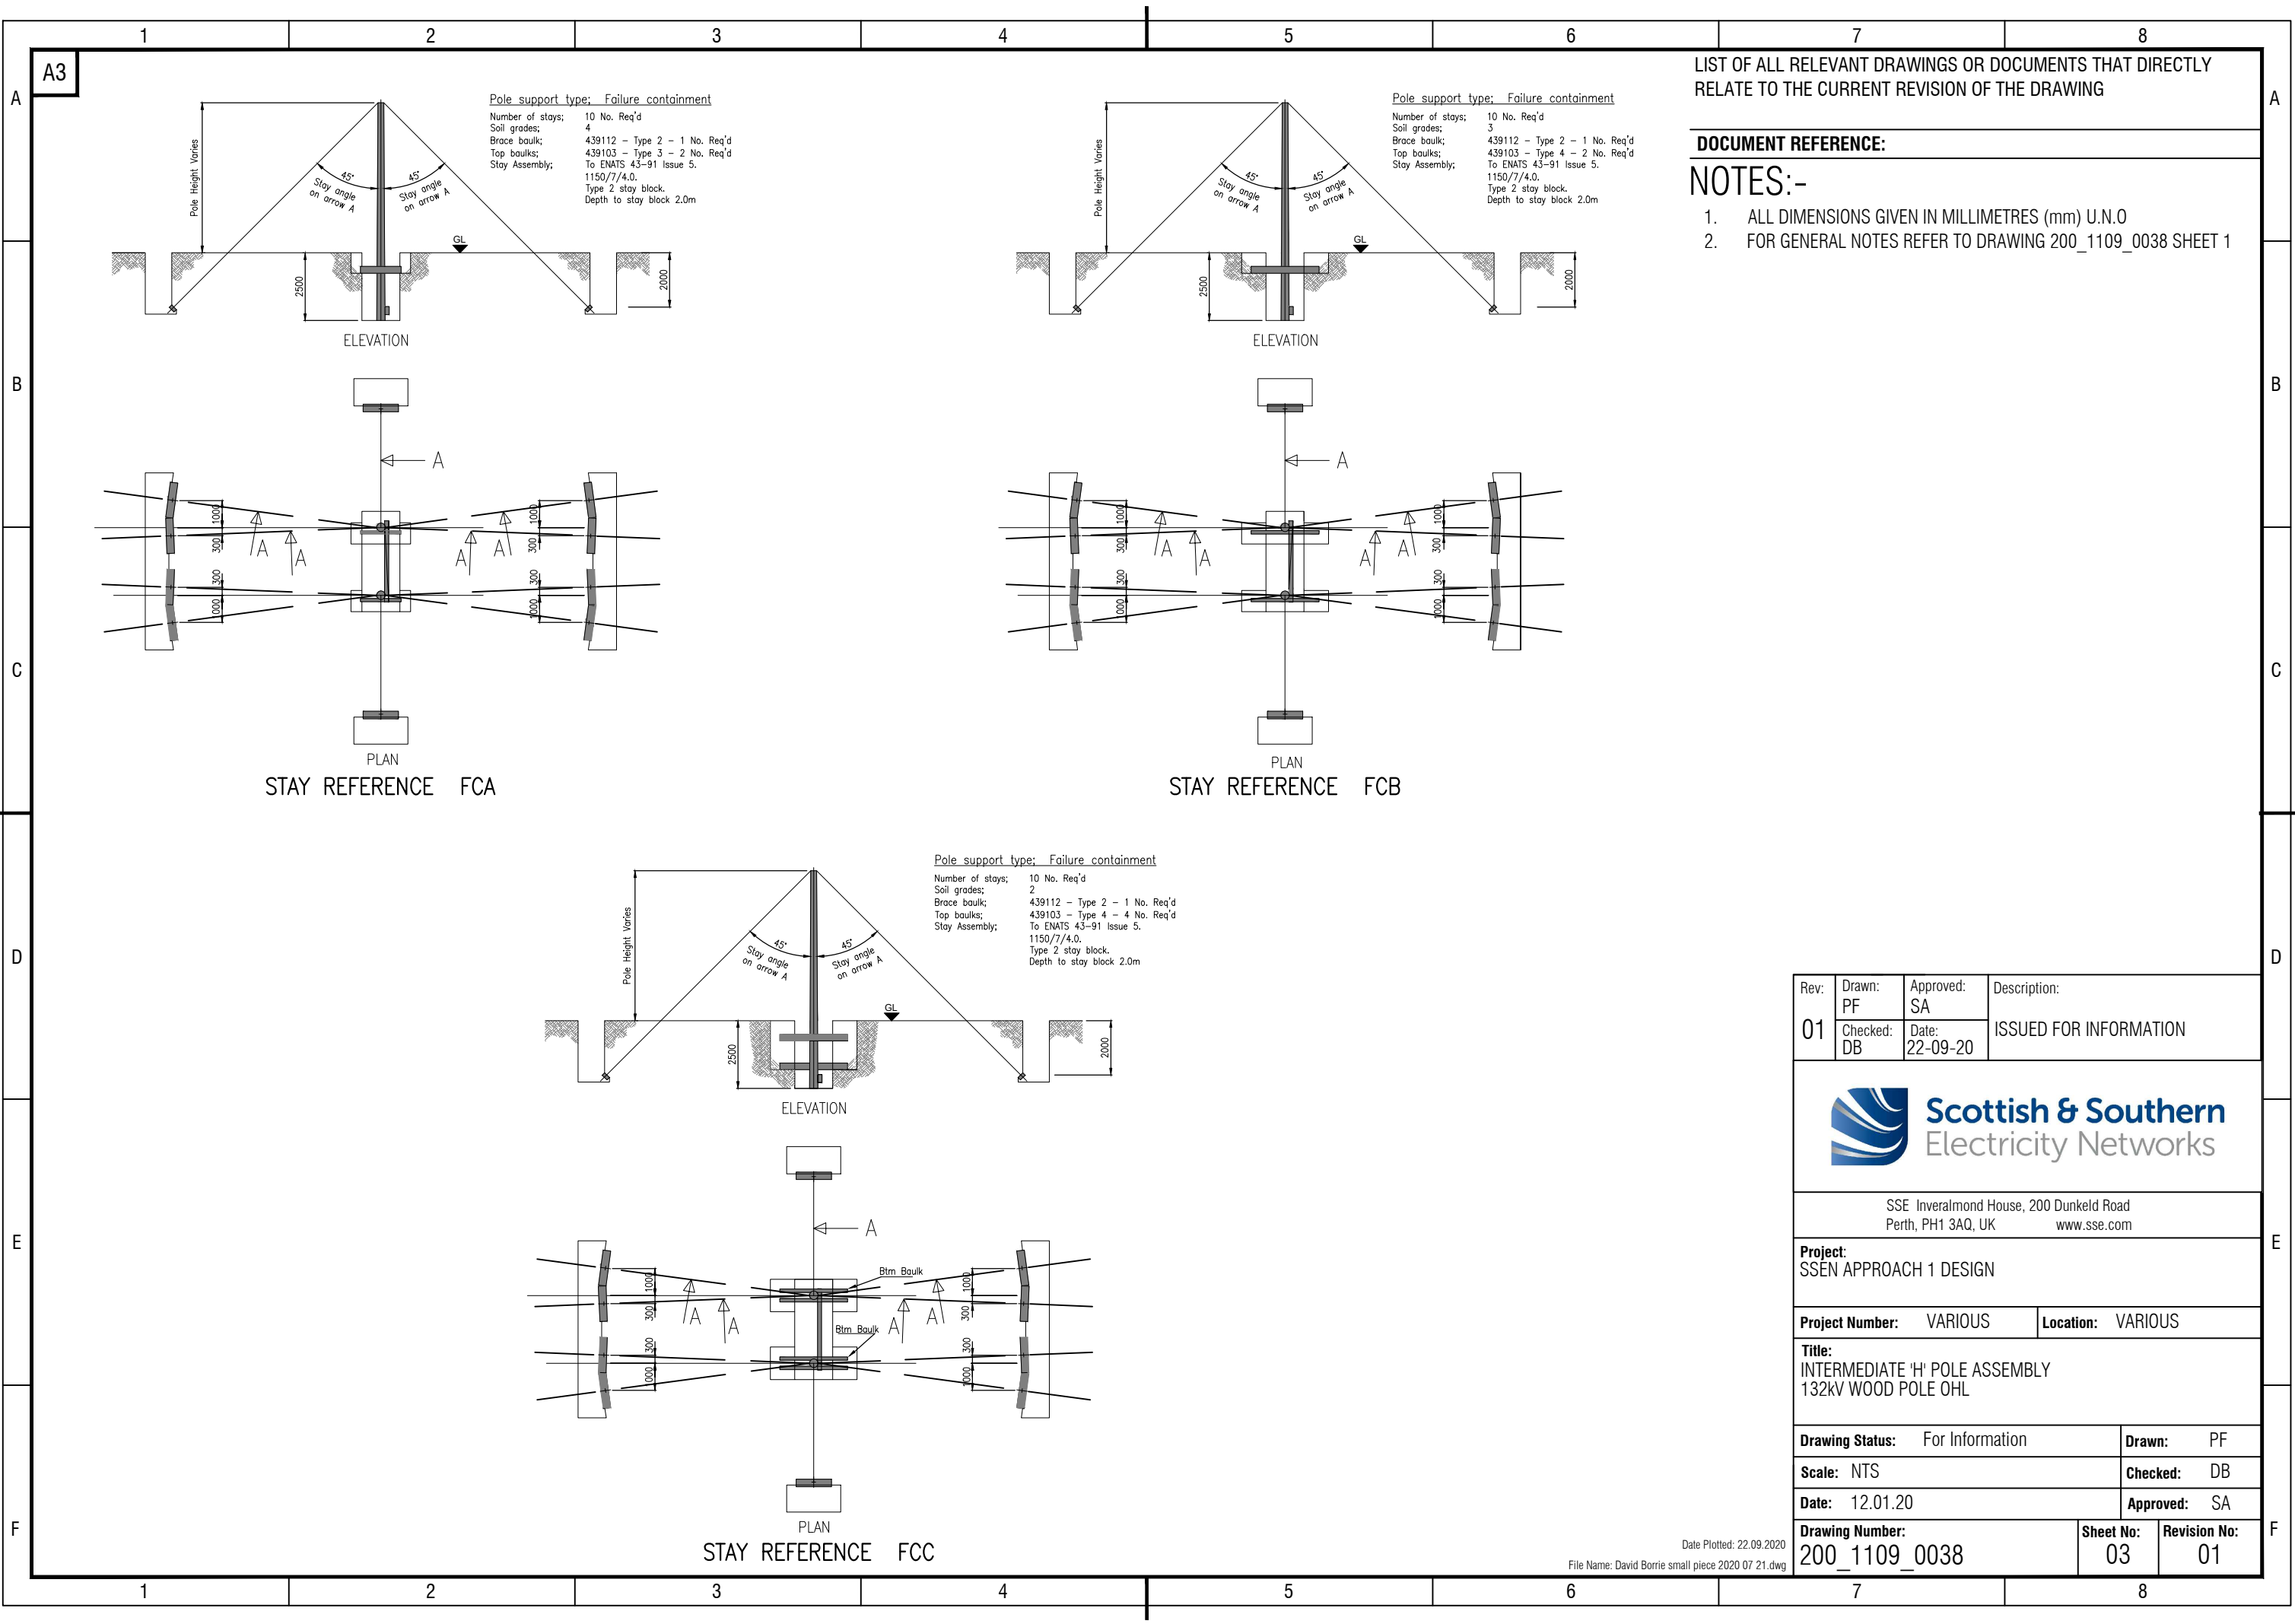

LIST OF ALL RELEVANT DRAWINGS OR DOCUMENTS THAT DIRECTLY RELATE TO THE CURRENT REVISION OF THE DRAWING

DOCUMENT REFERENCE:

NOTES:-

- 1. ALL DIMENSIONS GIVEN IN MILLIMETRES (mm) U.N.O
- 2. FOR GENERAL NOTES REFER TO DRAWING 200_1109_0038 SHEET 1

Rev: 01	Drawn: PF	Approved: SA	Description: ISSUED FOR INFORMATION
	Checked: DB	Date: 22-09-20	



Scottish & Southern
Electricity Networks

SSE Inverlmond House, 200 Dunkeld Road
Perth, PH1 3AQ, UK www.sse.com

Project:
SSEN APPROACH 1 DESIGN

Project Number: VARIOUS	Location: VARIOUS
--------------------------------	--------------------------

Title:
INTERMEDIATE 'H' POLE ASSEMBLY
132kV WOOD POLE OHL

Drawing Status: For Information	Drawn: PF
Scale: NTS	Checked: DB
Date: 12.01.20	Approved: SA

Drawing Number: 200_1109_0038	Sheet No: 03	Revision No: 01
---	------------------------	---------------------------