


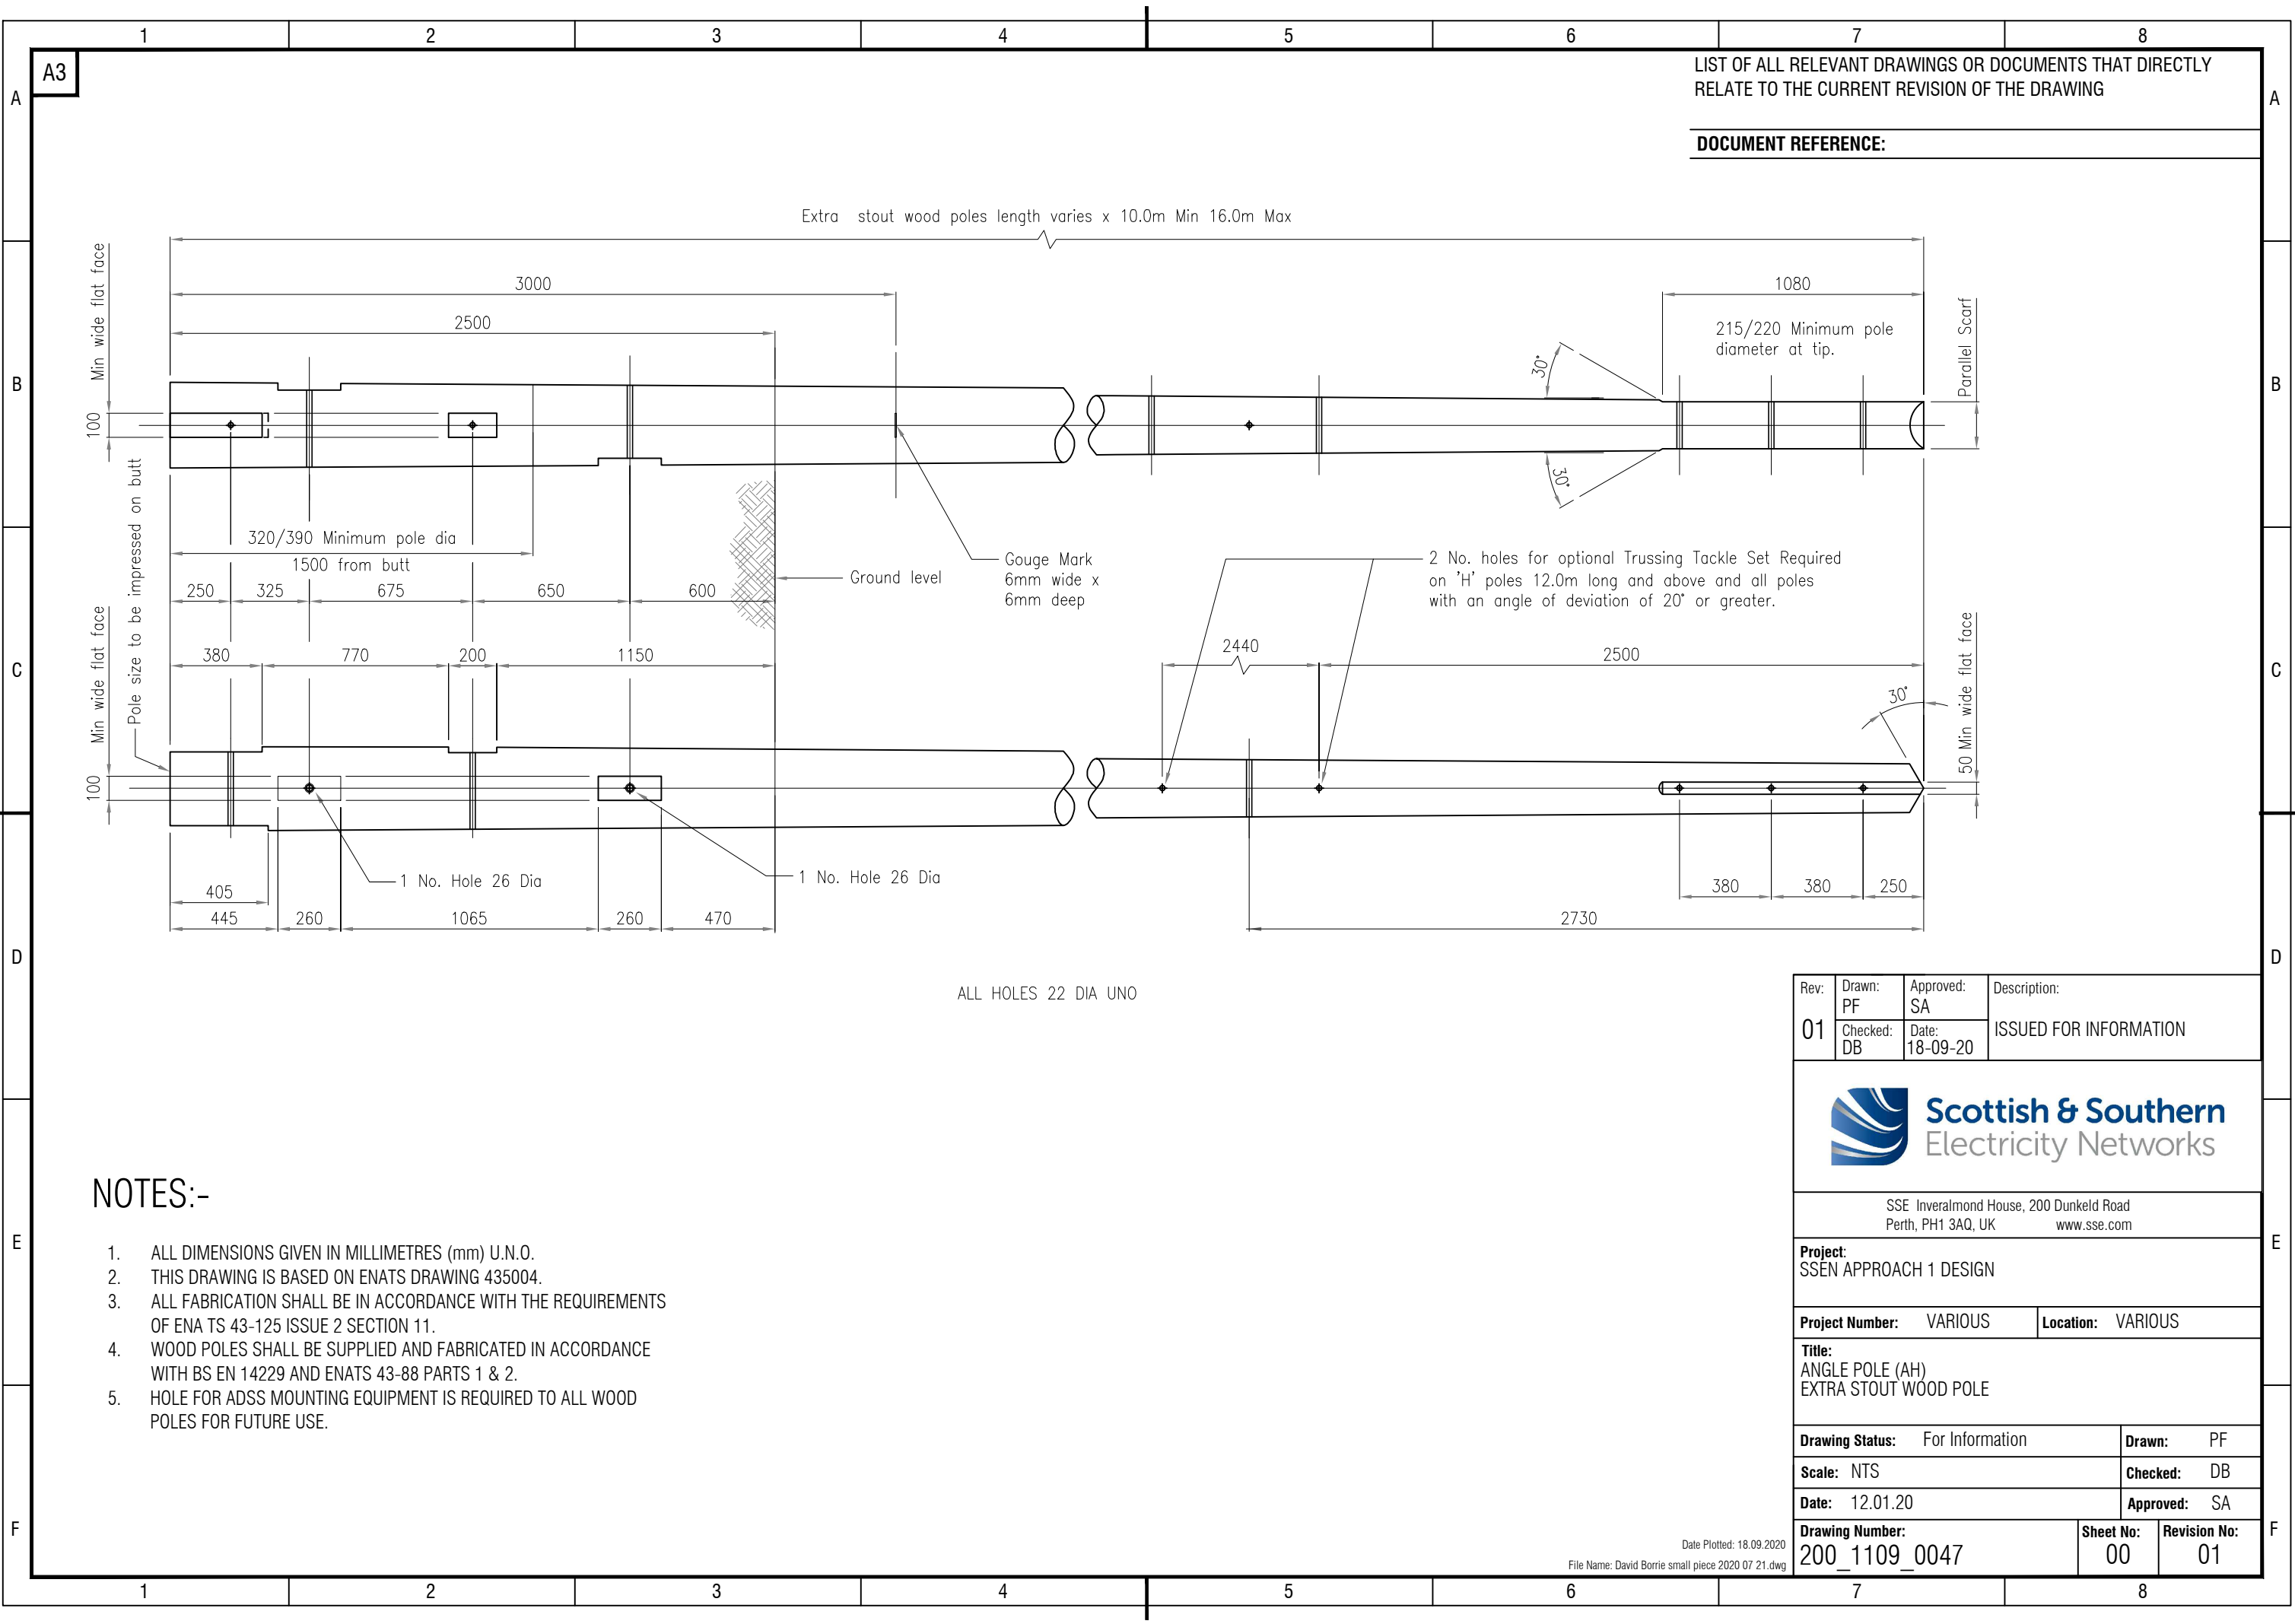

NOTES:-

1. ALL DIMENSIONS GIVEN IN MILLIMETRES (mm) U.N.O.
2. THIS DRAWING IS BASED ON ENATS DRAWING 435004.
3. ALL FABRICATION SHALL BE IN ACCORDANCE WITH THE REQUIREMENTS OF ENA TS 43-125 ISSUE 2 SECTION 11.
4. WOOD POLES SHALL BE SUPPLIED AND FABRICATED IN ACCORDANCE WITH BS EN 14229 AND ENATS 43-88 PARTS 1 & 2.
5. HOLE FOR ADSS MOUNTING EQUIPMENT IS REQUIRED TO ALL WOOD POLES FOR FUTURE USE.

ALL HOLES 22 DIA UNO

Rev:	Drawn: PF	Approved: SA	Description:
01	Checked: DB	Date: 18-09-20	ISSUED FOR INFORMATION
 Scottish & Southern Electricity Networks			
SSE Inveralmond House, 200 Dunkeld Road Perth, PH1 3AQ, UK www.sse.com			
Project: SSEN APPROACH 1 DESIGN			
Project Number: VARIOUS		Location: VARIOUS	
Title: ANGLE POLE (AH) EXTRA STOUT WOOD POLE			
Drawing Status: For Information			Drawn: PF
Scale: NTS			Checked: DB
Date: 12.01.20			Approved: SA
Drawing Number: 200_1109_0047			Sheet No: 00
			Revision No: 01

Date Plotted: 18.09.2020
File Name: David Borrie small piece 2020 07 21.dwg