


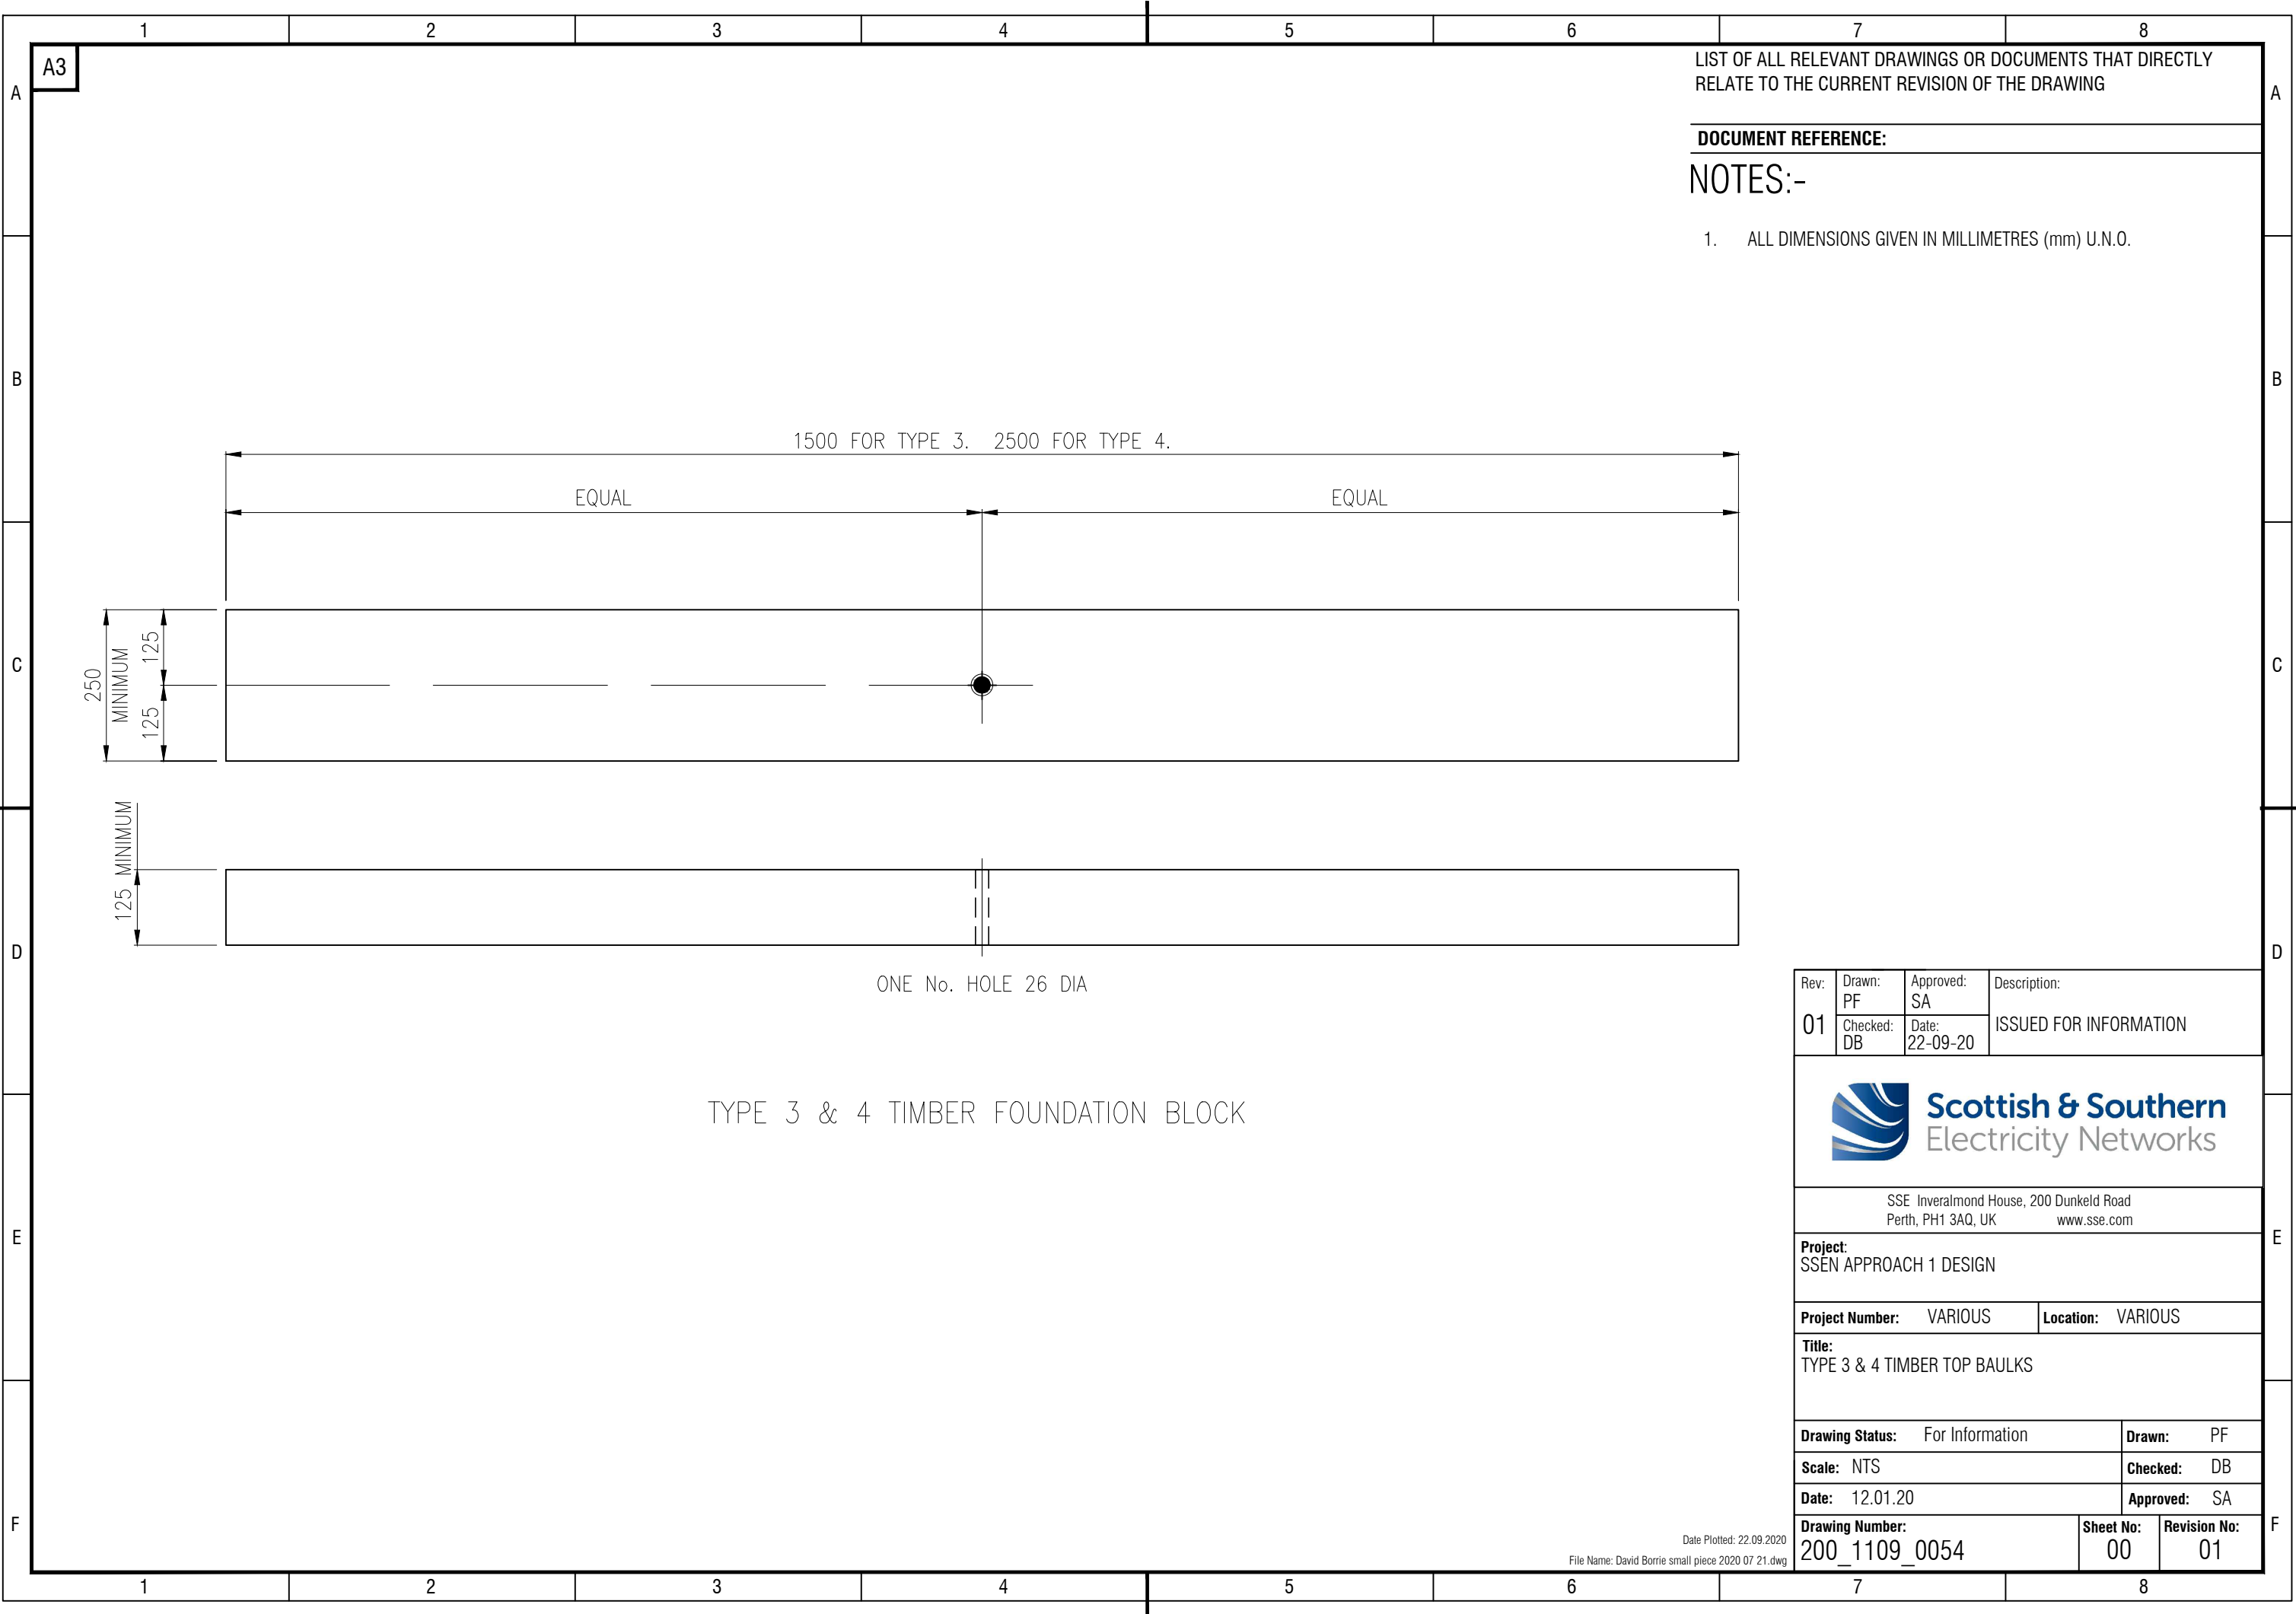

LIST OF ALL RELEVANT DRAWINGS OR DOCUMENTS THAT DIRECTLY RELATE TO THE CURRENT REVISION OF THE DRAWING

DOCUMENT REFERENCE:

NOTES:-

- 1. ALL DIMENSIONS GIVEN IN MILLIMETRES (mm) U.N.O.

Rev:	Drawn: PF	Approved: SA	Description: ISSUED FOR INFORMATION
01	Checked: DB	Date: 22-09-20	



Scottish & Southern
Electricity Networks

SSE Inveralmond House, 200 Dunkeld Road
Perth, PH1 3AQ, UK
www.sse.com

Project:
SSEN APPROACH 1 DESIGN

Project Number:	VARIOUS	Location:	VARIOUS
------------------------	---------	------------------	---------

Title:
TYPE 3 & 4 TIMBER TOP BAULKS

Drawing Status:	For Information	Drawn:	PF
Scale:	NTS	Checked:	DB
Date:	12.01.20	Approved:	SA

Drawing Number: 200_1109_0054	Sheet No: 00	Revision No: 01
---	------------------------	---------------------------