


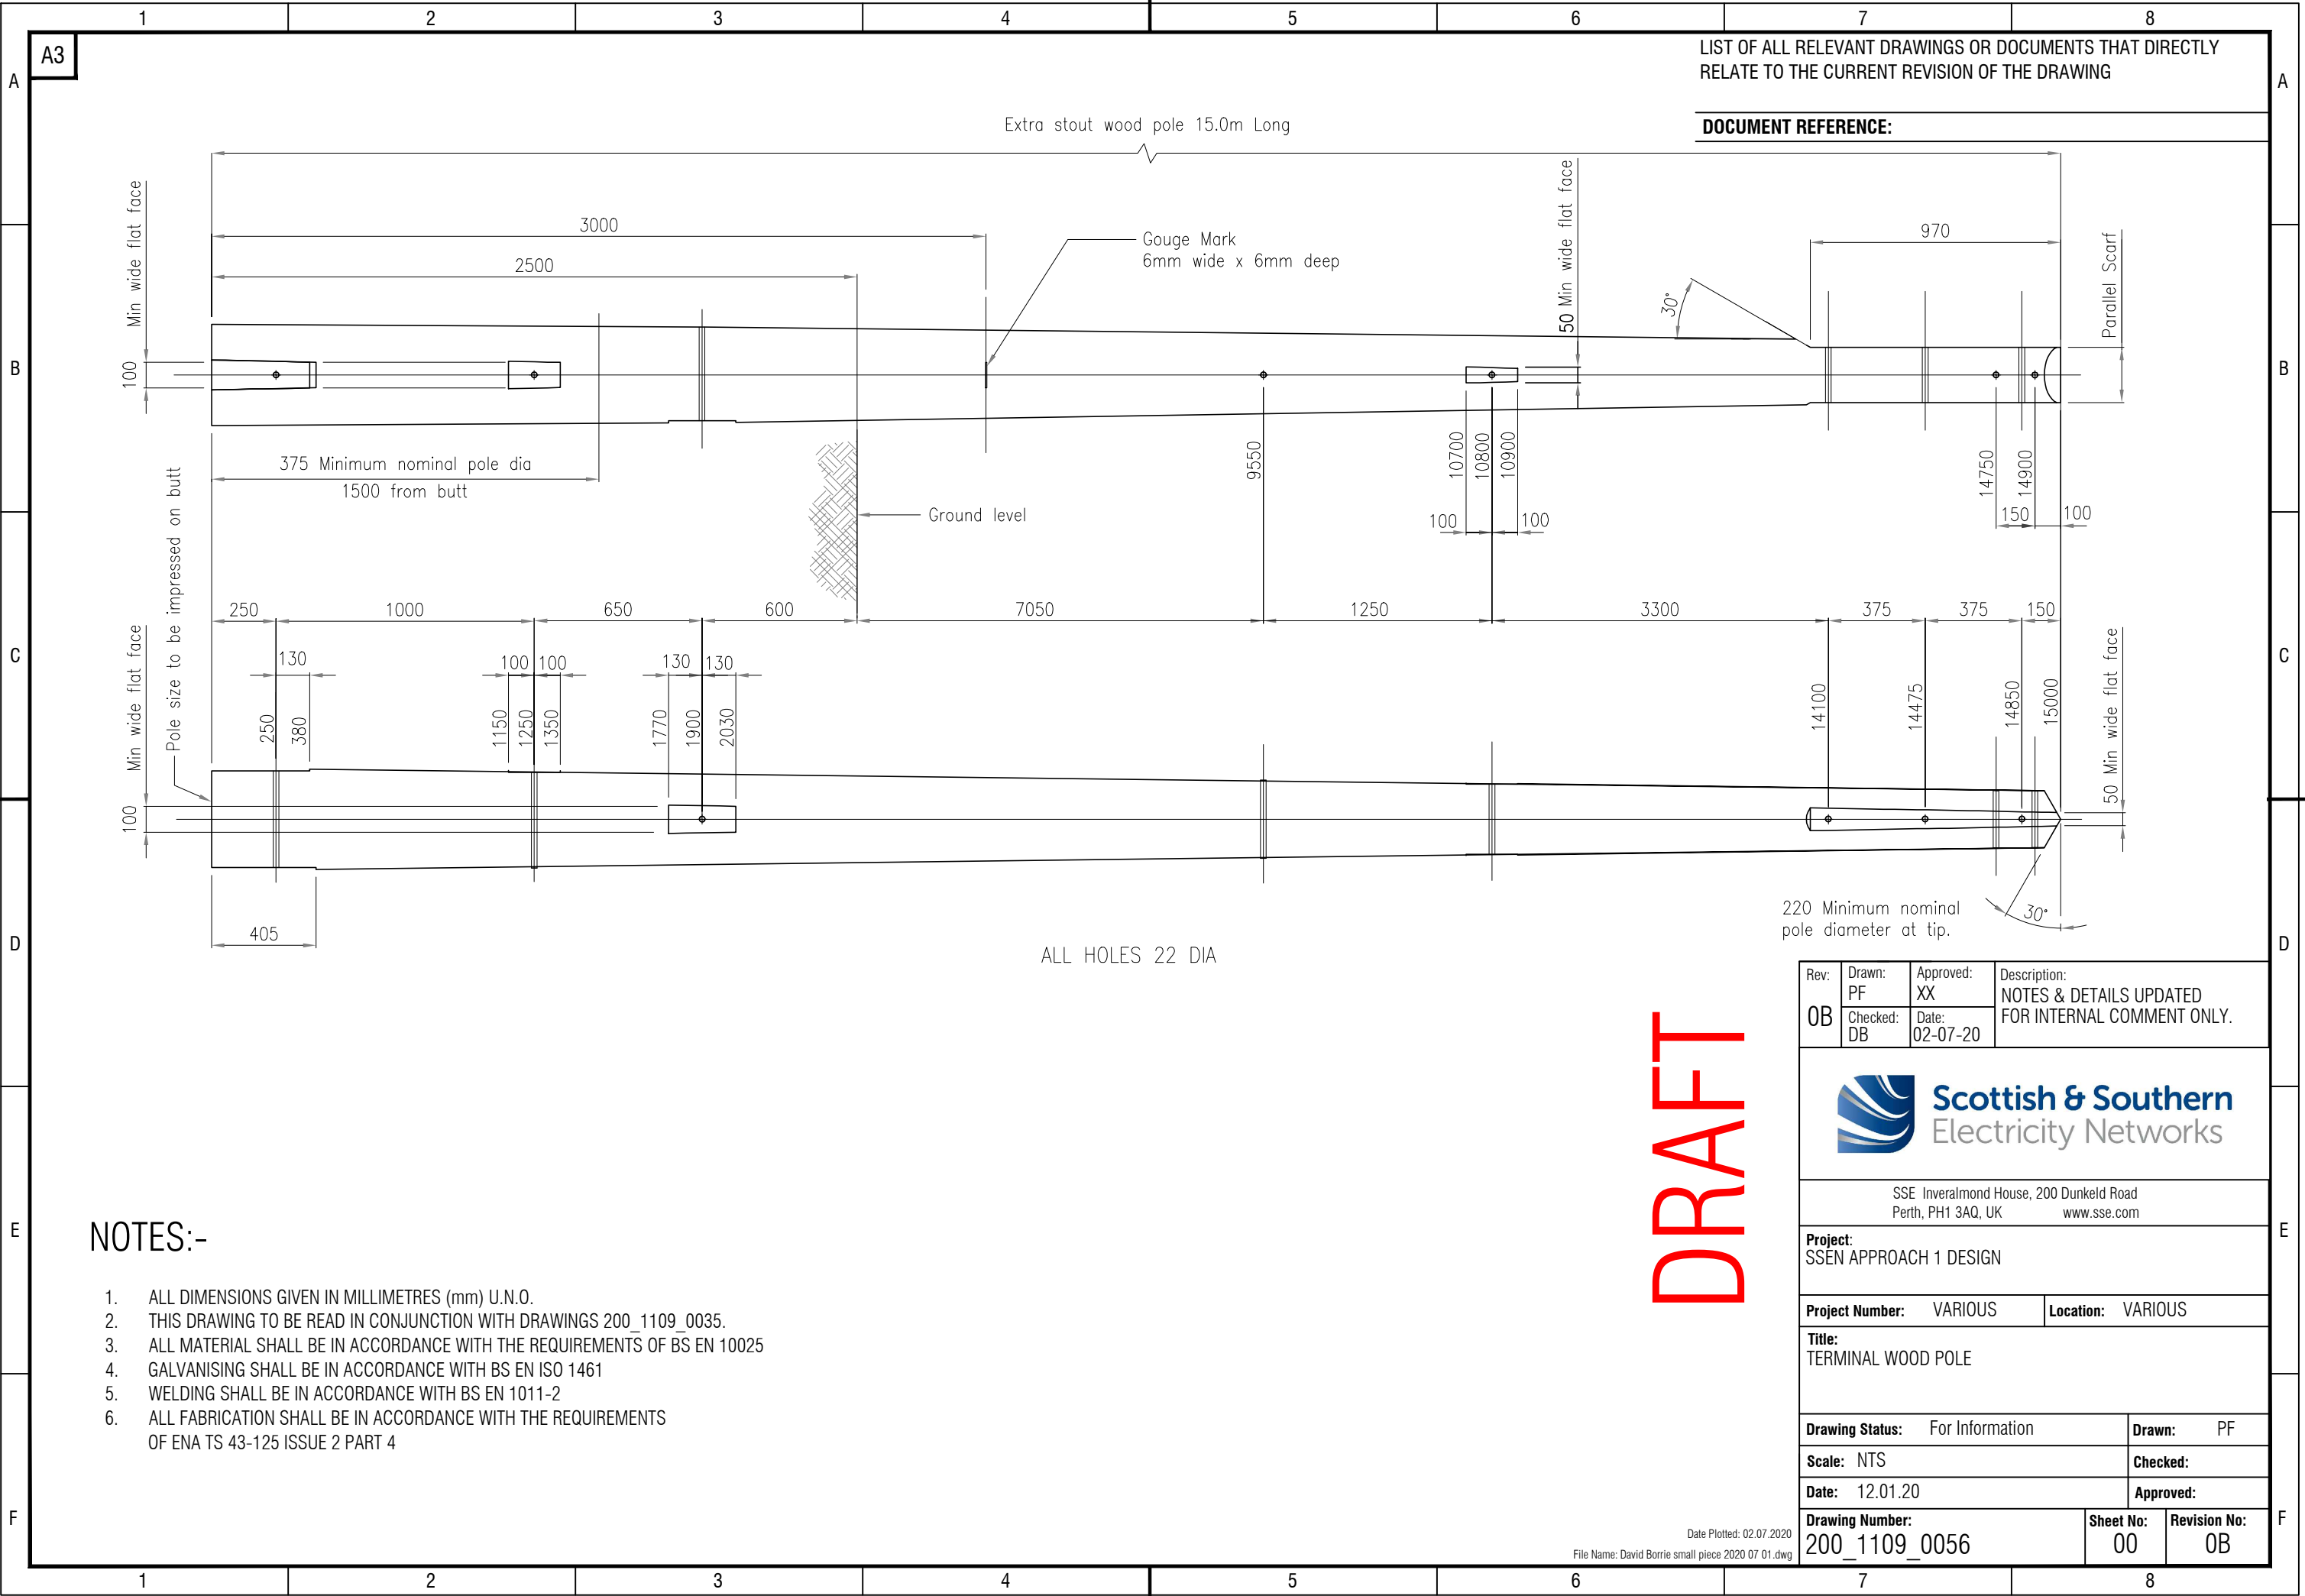

LIST OF ALL RELEVANT DRAWINGS OR DOCUMENTS THAT DIRECTLY RELATE TO THE CURRENT REVISION OF THE DRAWING

DOCUMENT REFERENCE:

NOTES:-

1. ALL DIMENSIONS GIVEN IN MILLIMETRES (mm) U.N.O.
2. THIS DRAWING TO BE READ IN CONJUNCTION WITH DRAWINGS 200_1109_0035.
3. ALL MATERIAL SHALL BE IN ACCORDANCE WITH THE REQUIREMENTS OF BS EN 10025
4. GALVANISING SHALL BE IN ACCORDANCE WITH BS EN ISO 1461
5. WELDING SHALL BE IN ACCORDANCE WITH BS EN 1011-2
6. ALL FABRICATION SHALL BE IN ACCORDANCE WITH THE REQUIREMENTS OF ENA TS 43-125 ISSUE 2 PART 4

Rev:	Drawn:	Approved:	Description:
0B	PF	XX	NOTES & DETAILS UPDATED FOR INTERNAL COMMENT ONLY.
	Checked: DB	Date: 02-07-20	

		Scottish & Southern Electricity Networks
---	--	--

SSE Inveralmond House, 200 Dunkeld Road Perth, PH1 3AQ, UK		www.sse.com
---	--	-------------

Project: SSEN APPROACH 1 DESIGN	
---	--

Project Number:	VARIOUS	Location:	VARIOUS
------------------------	---------	------------------	---------

Title: TERMINAL WOOD POLE	
-------------------------------------	--

Drawing Status:	For Information	Drawn:	PF
Scale:	NTS	Checked:	
Date:	12.01.20	Approved:	
Drawing Number:	200_1109_0056	Sheet No:	00
		Revision No:	0B