


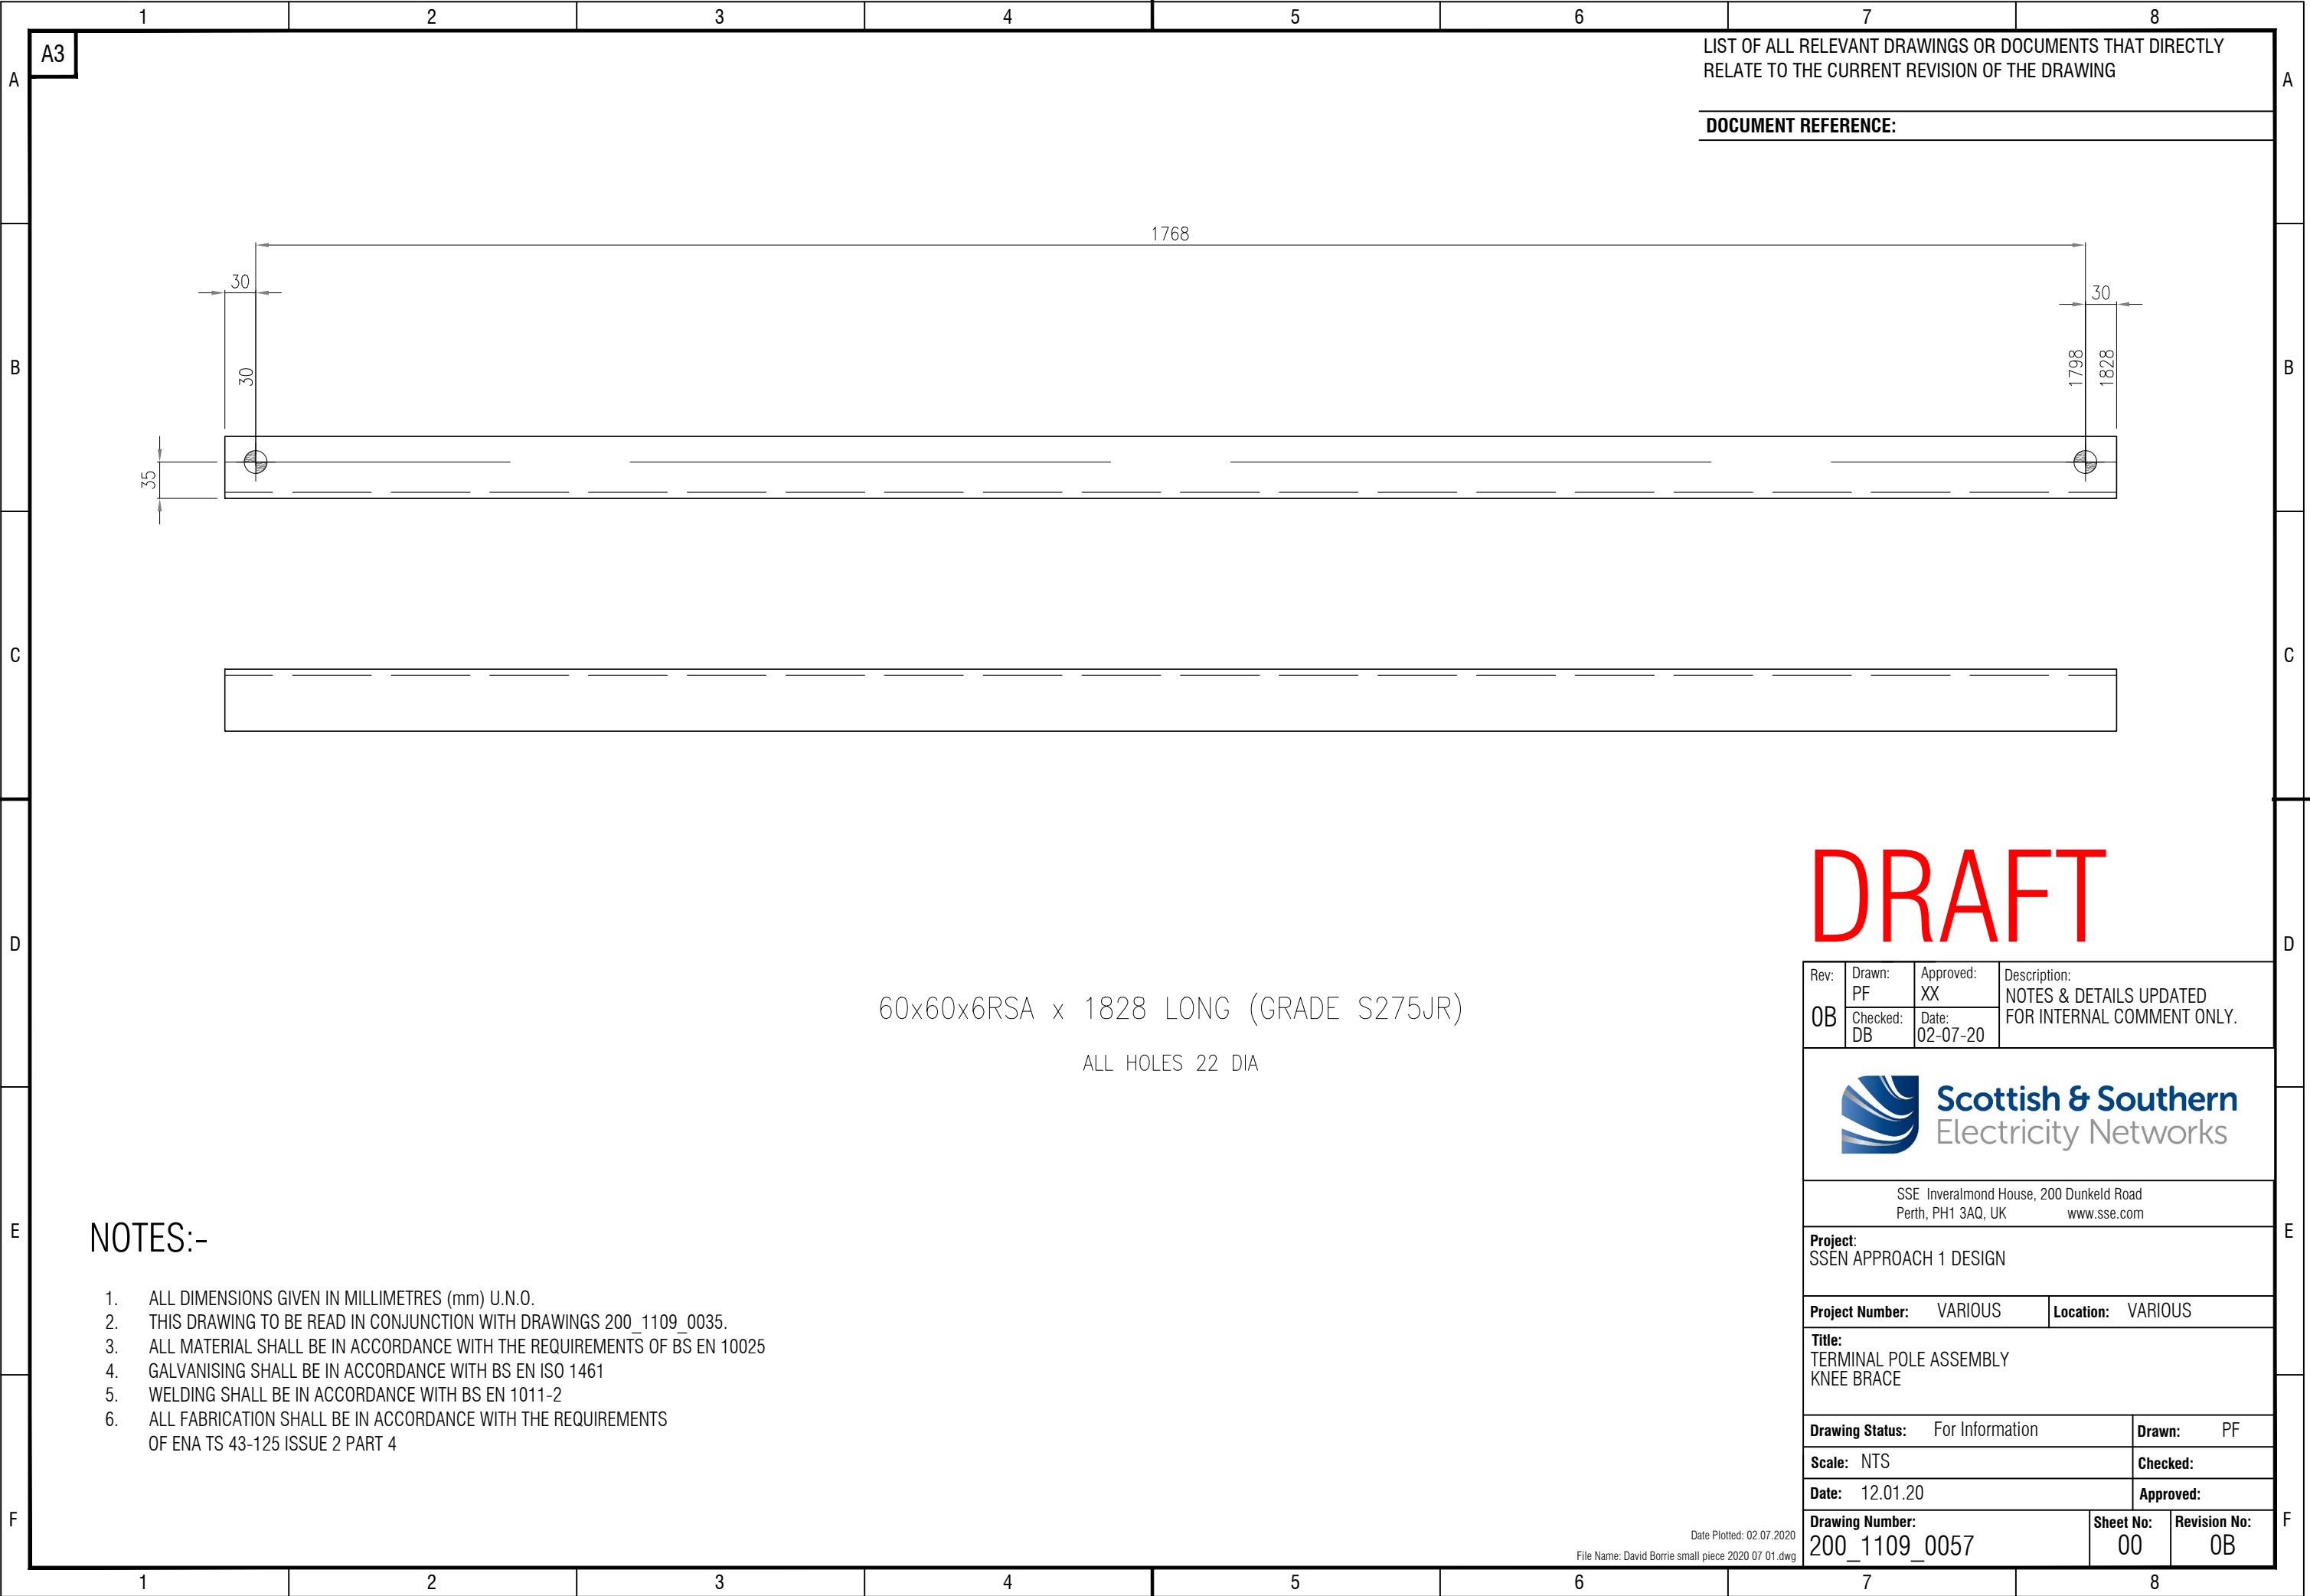

LIST OF ALL RELEVANT DRAWINGS OR DOCUMENTS THAT DIRECTLY
RELATE TO THE CURRENT REVISION OF THE DRAWING

DOCUMENT REFERENCE:

DRAFT

60x60x6RSA x 1828 LONG (GRADE S275JR)

ALL HOLES 22 DIA

NOTES:-

1. ALL DIMENSIONS GIVEN IN MILLIMETRES (mm) U.N.O.
2. THIS DRAWING TO BE READ IN CONJUNCTION WITH DRAWINGS 200_1109_0035.
3. ALL MATERIAL SHALL BE IN ACCORDANCE WITH THE REQUIREMENTS OF BS EN 10025
4. GALVANISING SHALL BE IN ACCORDANCE WITH BS EN ISO 1461
5. WELDING SHALL BE IN ACCORDANCE WITH BS EN 1011-2
6. ALL FABRICATION SHALL BE IN ACCORDANCE WITH THE REQUIREMENTS OF ENA TS 43-125 ISSUE 2 PART 4

Rev:	Drawn:	Approved:	Description:
0B	PF	XX	NOTES & DETAILS UPDATED FOR INTERNAL COMMENT ONLY.
Checked:	Date:		
DB	02-07-20		
 Scottish & Southern Electricity Networks			
SSE Inveralmond House, 200 Dunkeld Road Perth, PH1 3AQ, UK www.sse.com			
Project: SSEN APPROACH 1 DESIGN			
Project Number: VARIOUS		Location: VARIOUS	
Title: TERMINAL POLE ASSEMBLY KNEE BRACE			
Drawing Status: For Information		Drawn: PF	
Scale: NTS		Checked:	
Date: 12.01.20		Approved:	
Drawing Number: 200_1109_0057		Sheet No: 00	Revision No: 0B

Date Plotted: 02.07.2020

File Name: David Borrie small piece 2020 07 01.dwg