


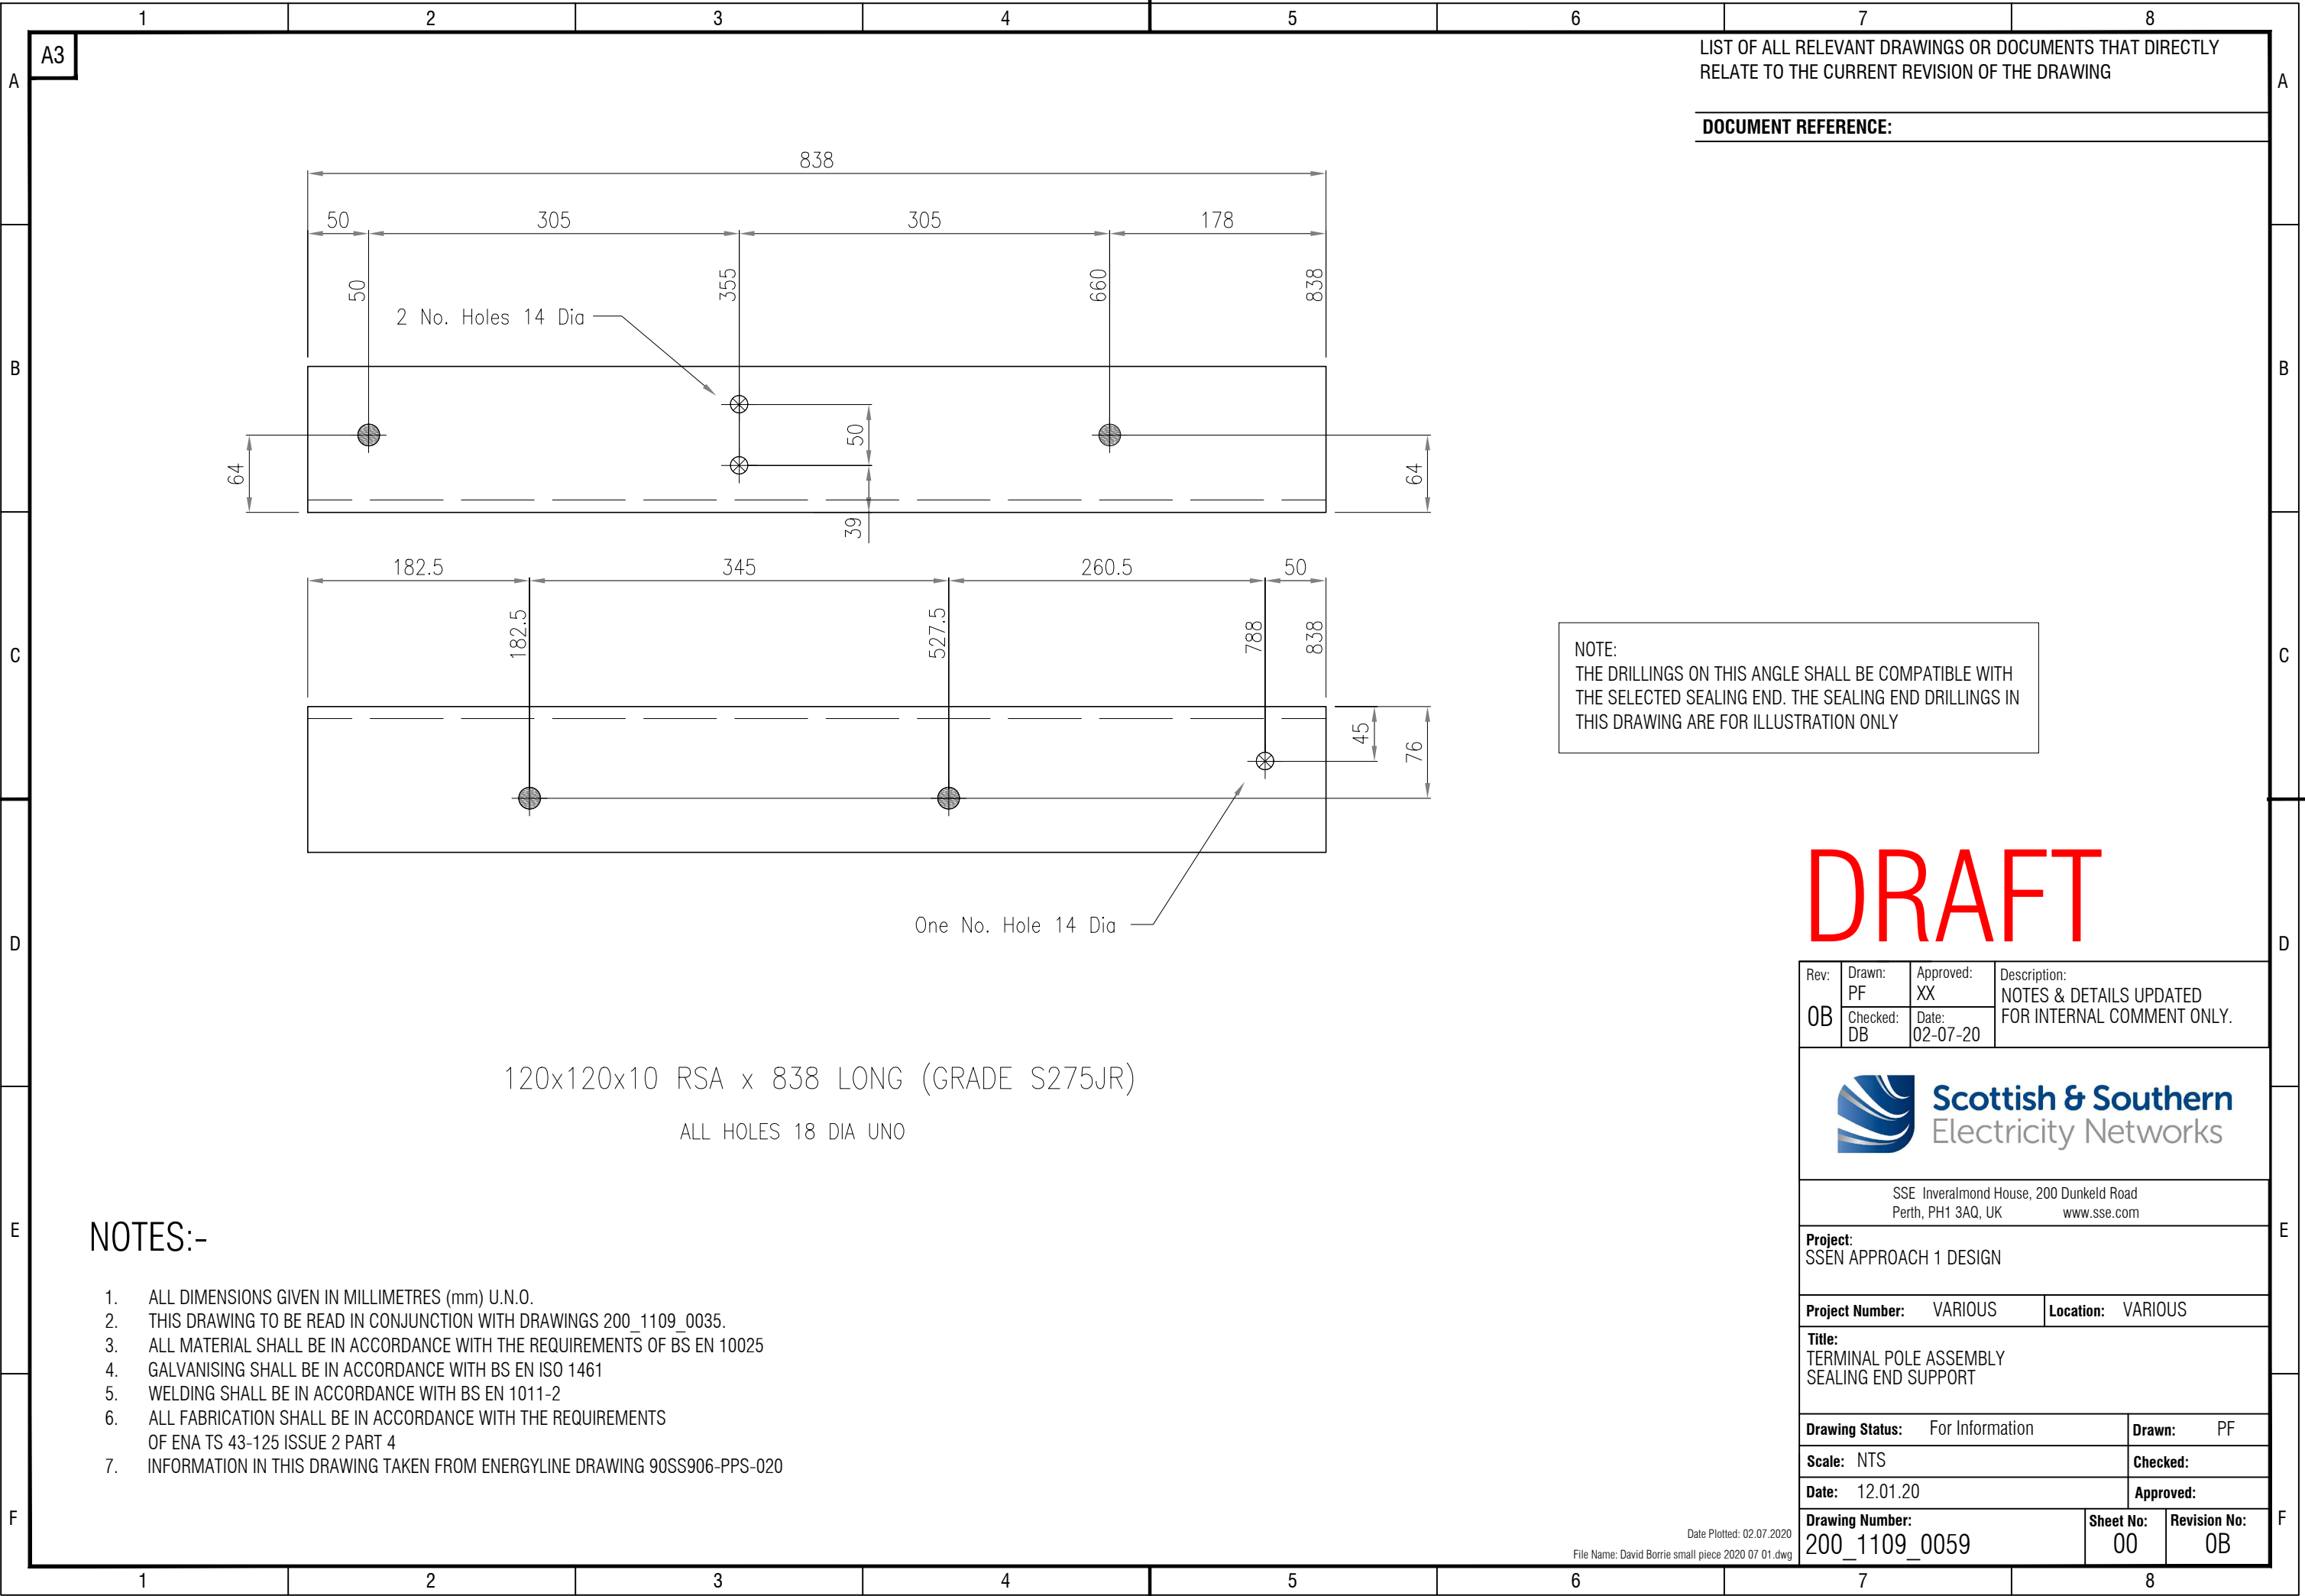

LIST OF ALL RELEVANT DRAWINGS OR DOCUMENTS THAT DIRECTLY RELATE TO THE CURRENT REVISION OF THE DRAWING

DOCUMENT REFERENCE:

NOTE:
THE DRILLINGS ON THIS ANGLE SHALL BE COMPATIBLE WITH THE SELECTED SEALING END. THE SEALING END DRILLINGS IN THIS DRAWING ARE FOR ILLUSTRATION ONLY

DRAFT

Rev:	Drawn:	Approved:	Description:
0B	PF	XX	NOTES & DETAILS UPDATED FOR INTERNAL COMMENT ONLY.
	Checked: DB	Date: 02-07-20	

	Scottish & Southern Electricity Networks
---	--

SSE Inveralmond House, 200 Dunkeld Road Perth, PH1 3AQ, UK www.sse.com	
--	--

Project: SSEN APPROACH 1 DESIGN	
---	--

Project Number: VARIOUS	Location: VARIOUS
--------------------------------	--------------------------

Title: TERMINAL POLE ASSEMBLY SEALING END SUPPORT	
--	--

Drawing Status: For Information	Drawn: PF	
Scale: NTS	Checked:	
Date: 12.01.20	Approved:	
Drawing Number: 200_1109_0059	Sheet No: 00	Revision No: 0B

NOTES:-

- ALL DIMENSIONS GIVEN IN MILLIMETRES (mm) U.N.O.
- THIS DRAWING TO BE READ IN CONJUNCTION WITH DRAWINGS 200_1109_0035.
- ALL MATERIAL SHALL BE IN ACCORDANCE WITH THE REQUIREMENTS OF BS EN 10025
- GALVANISING SHALL BE IN ACCORDANCE WITH BS EN ISO 1461
- WELDING SHALL BE IN ACCORDANCE WITH BS EN 1011-2
- ALL FABRICATION SHALL BE IN ACCORDANCE WITH THE REQUIREMENTS OF ENA TS 43-125 ISSUE 2 PART 4
- INFORMATION IN THIS DRAWING TAKEN FROM ENERGYLINE DRAWING 90SS906-PPS-020