


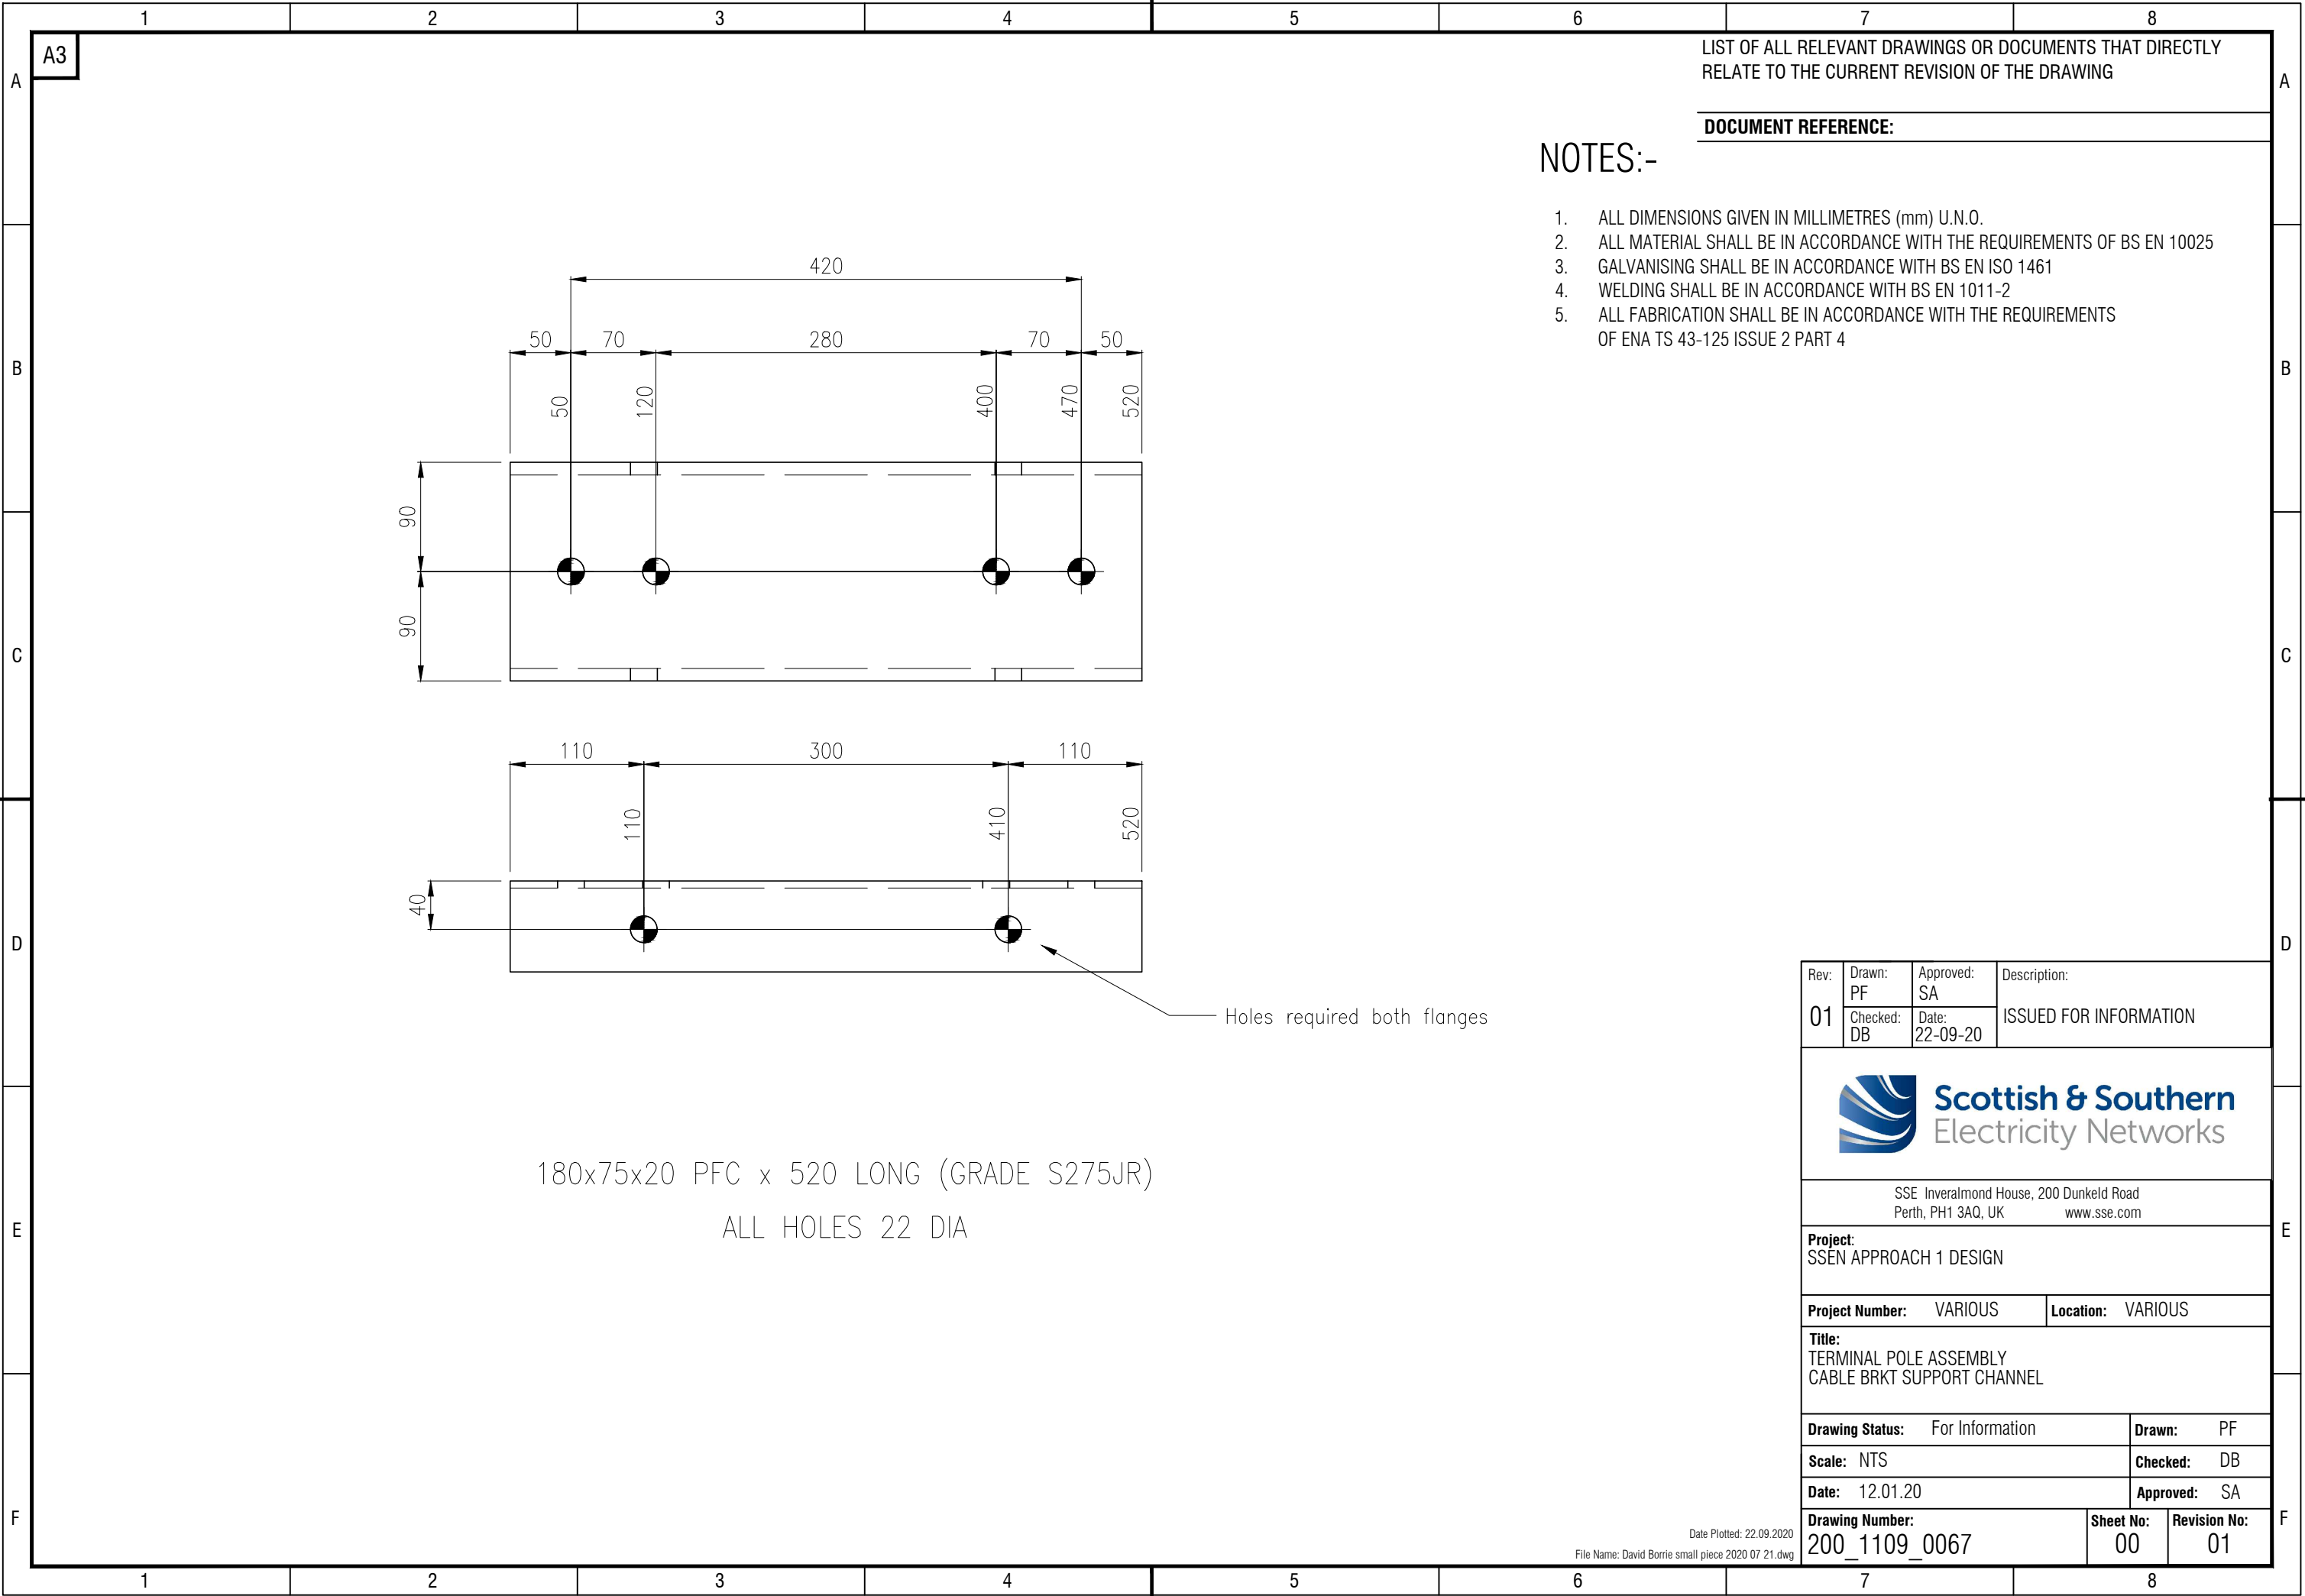

LIST OF ALL RELEVANT DRAWINGS OR DOCUMENTS THAT DIRECTLY RELATE TO THE CURRENT REVISION OF THE DRAWING

DOCUMENT REFERENCE:

NOTES:-

1. ALL DIMENSIONS GIVEN IN MILLIMETRES (mm) U.N.O.
2. ALL MATERIAL SHALL BE IN ACCORDANCE WITH THE REQUIREMENTS OF BS EN 10025
3. GALVANISING SHALL BE IN ACCORDANCE WITH BS EN ISO 1461
4. WELDING SHALL BE IN ACCORDANCE WITH BS EN 1011-2
5. ALL FABRICATION SHALL BE IN ACCORDANCE WITH THE REQUIREMENTS OF ENA TS 43-125 ISSUE 2 PART 4

|   |             |                   |                        |
|---|-------------|-------------------|------------------------|
| Rev:   | Drawn: PF   | Approved: SA      | Description:           |
| 01   | Checked: DB | Date: 22-09-20    | ISSUED FOR INFORMATION |
| <div><div>Scottish &amp; Southern<br/>Electricity Networks</div></div> |             |                   |                        |
| SSE Inverlmond House, 200 Dunkeld Road<br>Perth, PH1 3AQ, UKwww.sse.com                                                                                     |             |                   |                        |
| Project:<br>SSEN APPROACH 1 DESIGN   |             |                   |                        |
| Project Number: VARIOUS   |             | Location: VARIOUS |                        |
| Title:<br>TERMINAL POLE ASSEMBLY<br>CABLE BRKT SUPPORT CHANNEL                                                                                              |             |                   |                        |
| Drawing Status: For Information   |             | Drawn: PF         |                        |
| Scale: NTS   |             | Checked: DB       |                        |
| Date: 12.01.20   |             | Approved: SA      |                        |
| Drawing Number:<br>200_1109_0067   |             | Sheet No:<br>00   | Revision No:<br>01     |