


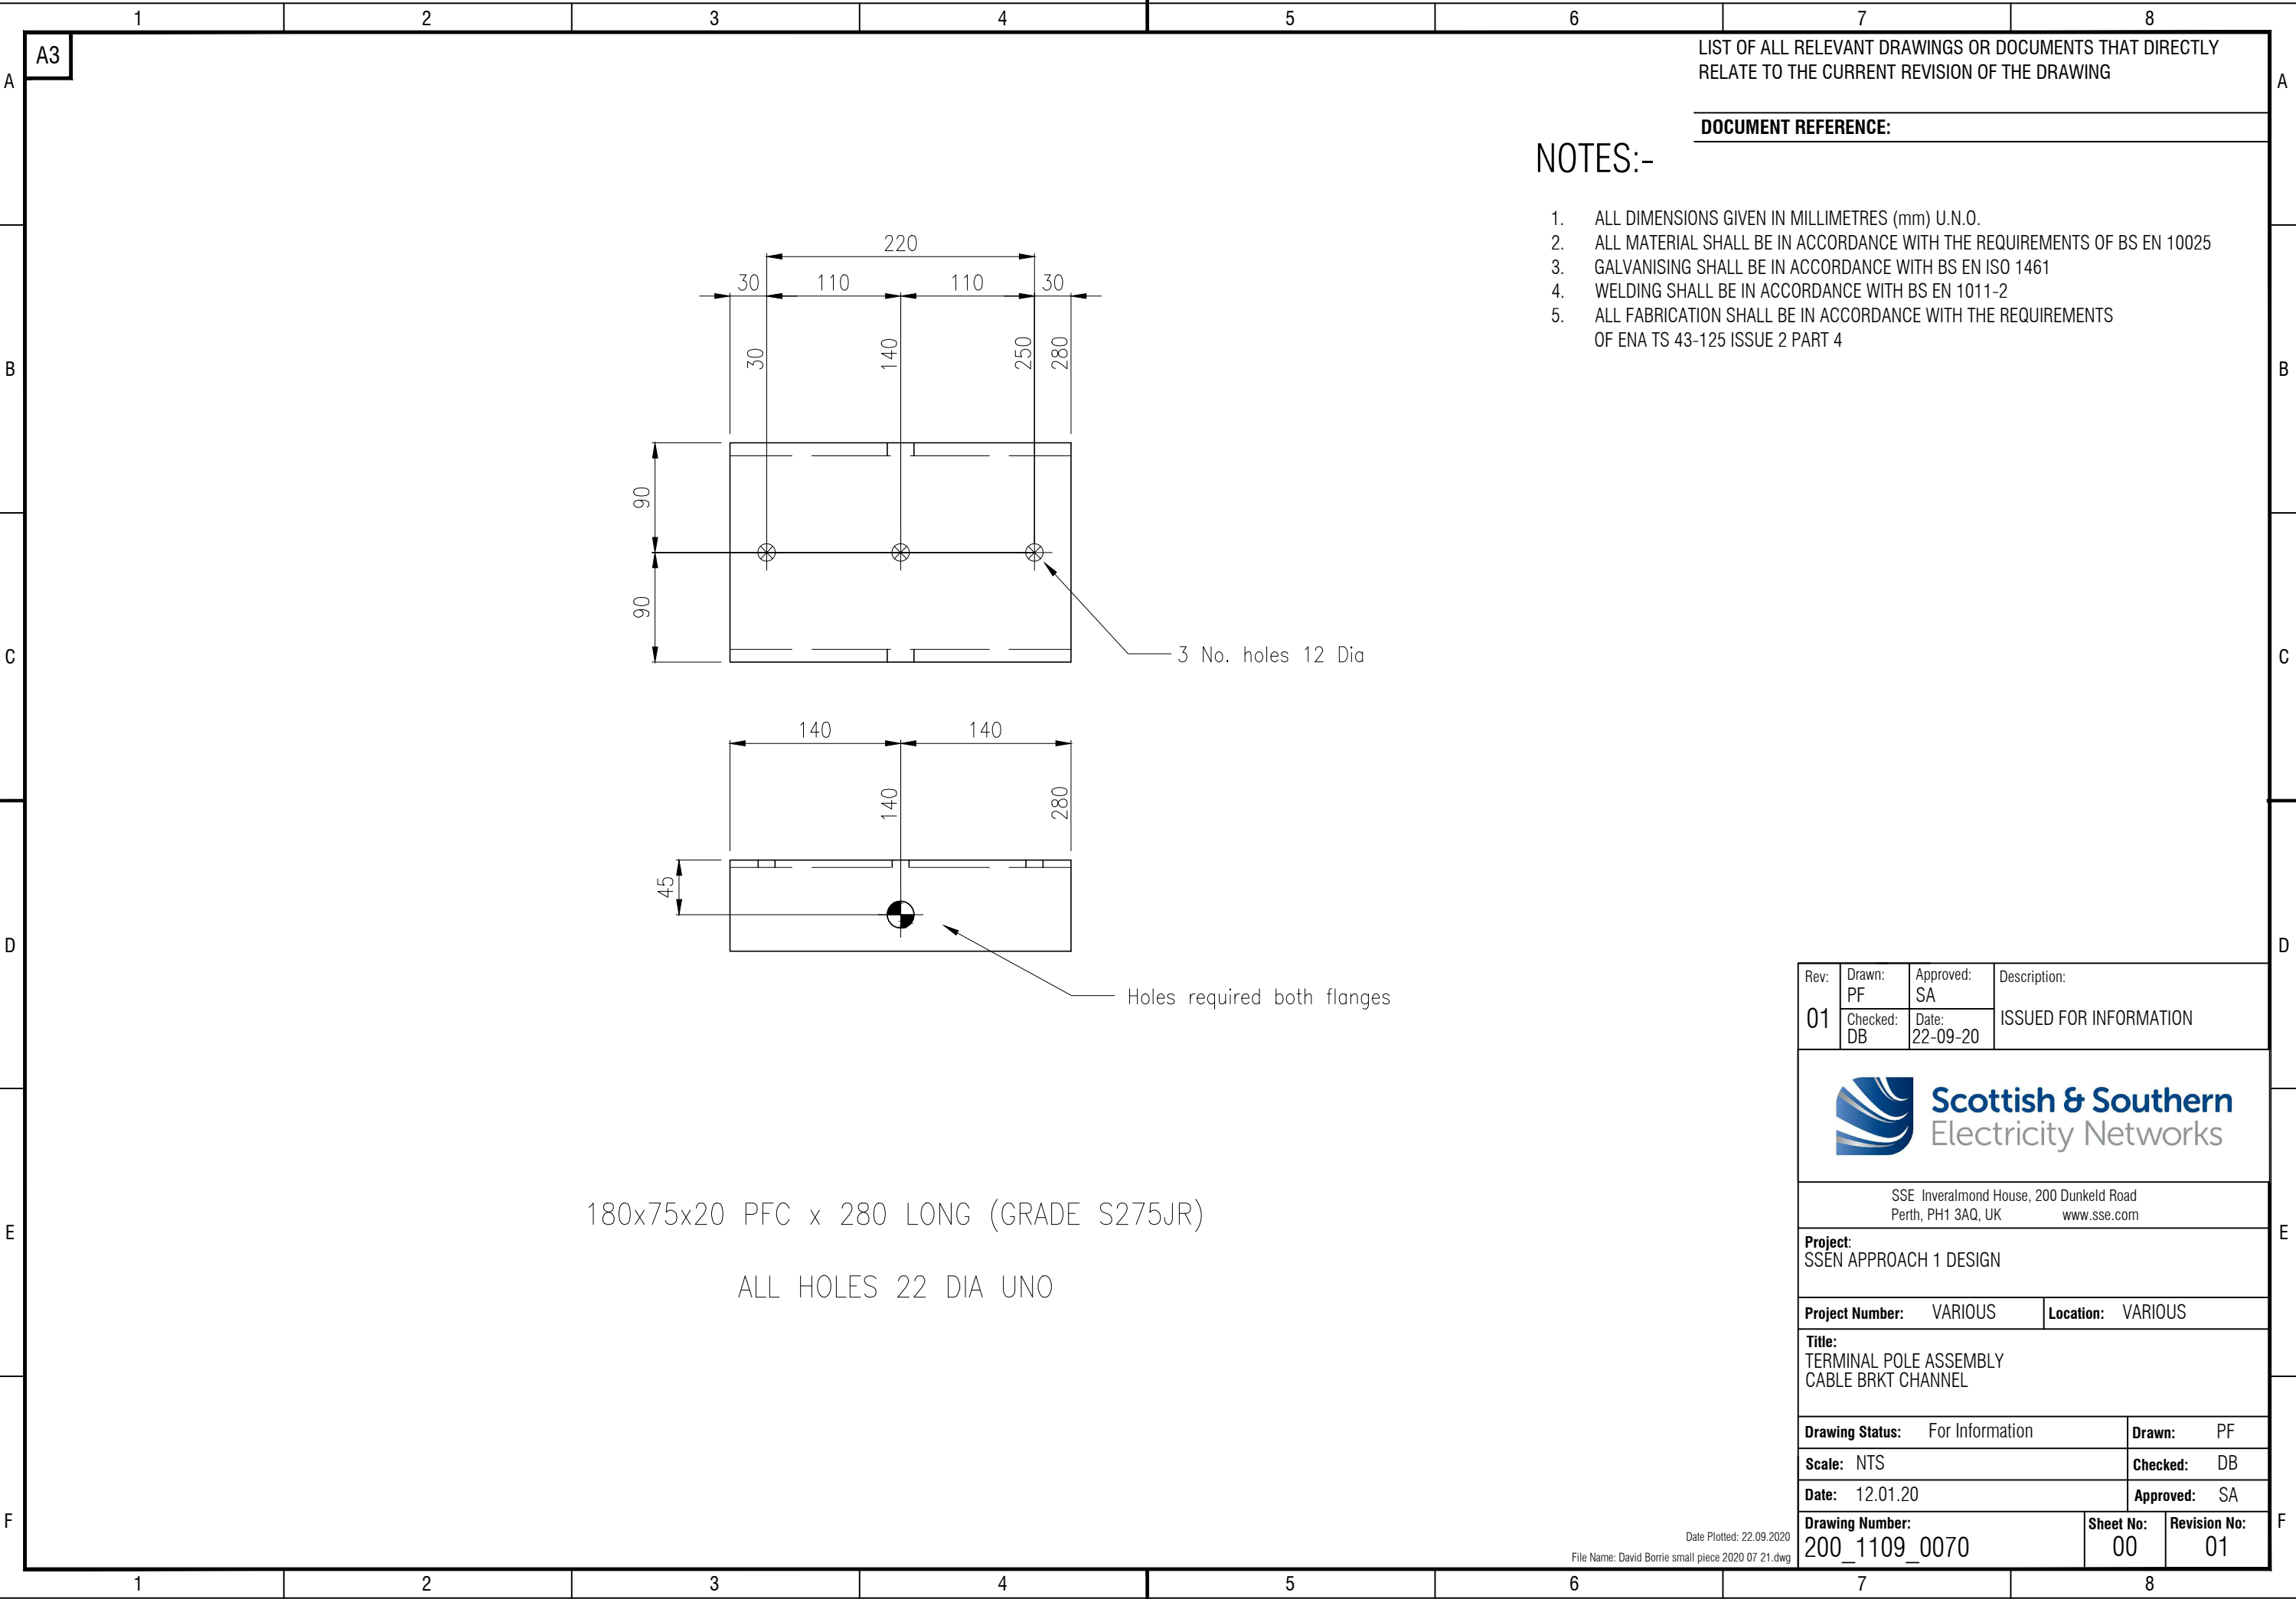

LIST OF ALL RELEVANT DRAWINGS OR DOCUMENTS THAT DIRECTLY
RELATE TO THE CURRENT REVISION OF THE DRAWING

DOCUMENT REFERENCE:

NOTES:-

1. ALL DIMENSIONS GIVEN IN MILLIMETRES (mm) U.N.O.
2. ALL MATERIAL SHALL BE IN ACCORDANCE WITH THE REQUIREMENTS OF BS EN 10025
3. GALVANISING SHALL BE IN ACCORDANCE WITH BS EN ISO 1461
4. WELDING SHALL BE IN ACCORDANCE WITH BS EN 1011-2
5. ALL FABRICATION SHALL BE IN ACCORDANCE WITH THE REQUIREMENTS
OF ENA TS 43-125 ISSUE 2 PART 4

Rev:	Drawn: PF	Approved: SA	Description:
01	Checked: DB	Date: 22-09-20	ISSUED FOR INFORMATION



Scottish & Southern
Electricity Networks

SSE Inveralmond House, 200 Dunkeld Road
Perth, PH1 3AQ, UKwww.sse.com

Project:
SSEN APPROACH 1 DESIGN

Project Number:	VARIOUS	Location:	VARIOUS
Title: TERMINAL POLE ASSEMBLY CABLE BRKT CHANNEL			

Drawing Status:	For Information	Drawn:	PF
Scale:	NTS	Checked:	DB
Date:	12.01.20	Approved:	SA
Drawing Number: 200_1109_0070	Sheet No: 00	Revision No: 01	

Date Plotted: 22.09.2020

File Name: David Borrie small piece 2020 07 21.dwg