


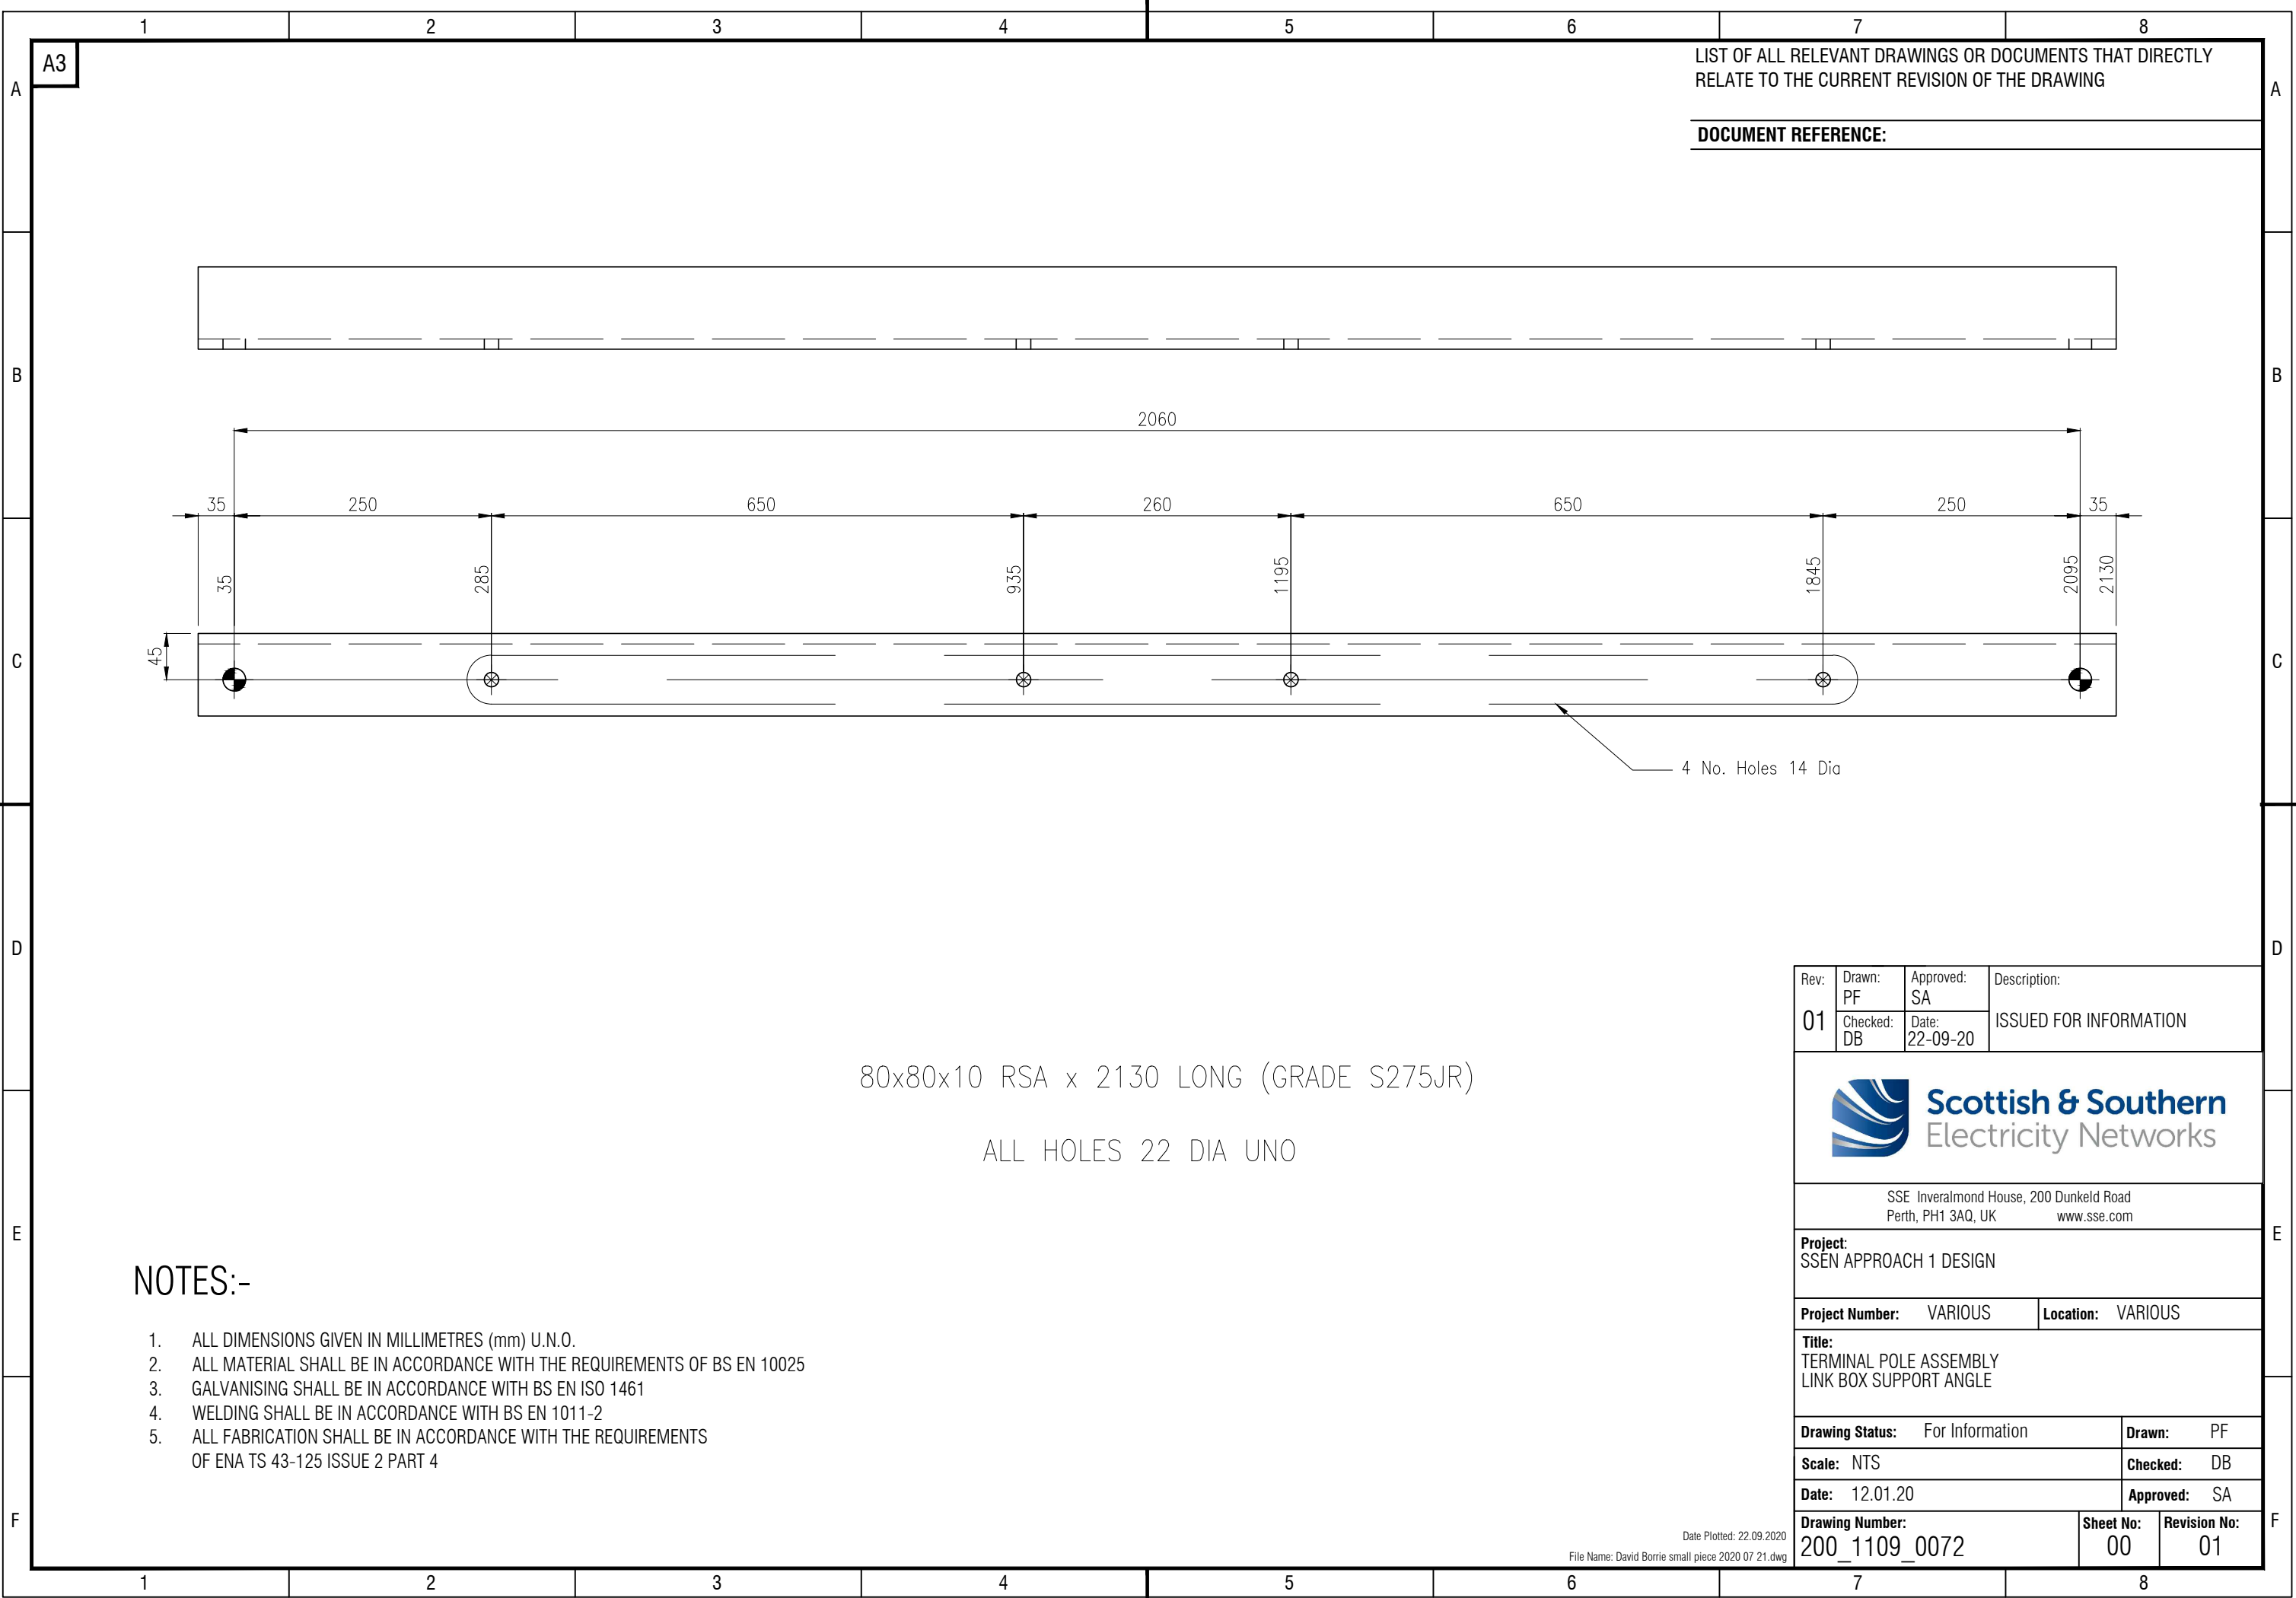

LIST OF ALL RELEVANT DRAWINGS OR DOCUMENTS THAT DIRECTLY
RELATE TO THE CURRENT REVISION OF THE DRAWING

DOCUMENT REFERENCE:

Rev:	Drawn: PF	Approved: SA	Description:
01	Checked: DB	Date: 22-09-20	ISSUED FOR INFORMATION
 Scottish & Southern Electricity Networks			
SSE Inveralmond House, 200 Dunkeld Road Perth, PH1 3AQ, UK www.sse.com			
Project: SSEN APPROACH 1 DESIGN			
Project Number: VARIOUS		Location: VARIOUS	
Title: TERMINAL POLE ASSEMBLY LINK BOX SUPPORT ANGLE			
Drawing Status: For Information			Drawn: PF
Scale: NTS			Checked: DB
Date: 12.01.20			Approved: SA
Drawing Number: 200_1109_0072			Sheet No: 00
			Revision No: 01

NOTES:-

1. ALL DIMENSIONS GIVEN IN MILLIMETRES (mm) U.N.O.
2. ALL MATERIAL SHALL BE IN ACCORDANCE WITH THE REQUIREMENTS OF BS EN 10025
3. GALVANISING SHALL BE IN ACCORDANCE WITH BS EN ISO 1461
4. WELDING SHALL BE IN ACCORDANCE WITH BS EN 1011-2
5. ALL FABRICATION SHALL BE IN ACCORDANCE WITH THE REQUIREMENTS
OF ENA TS 43-125 ISSUE 2 PART 4