


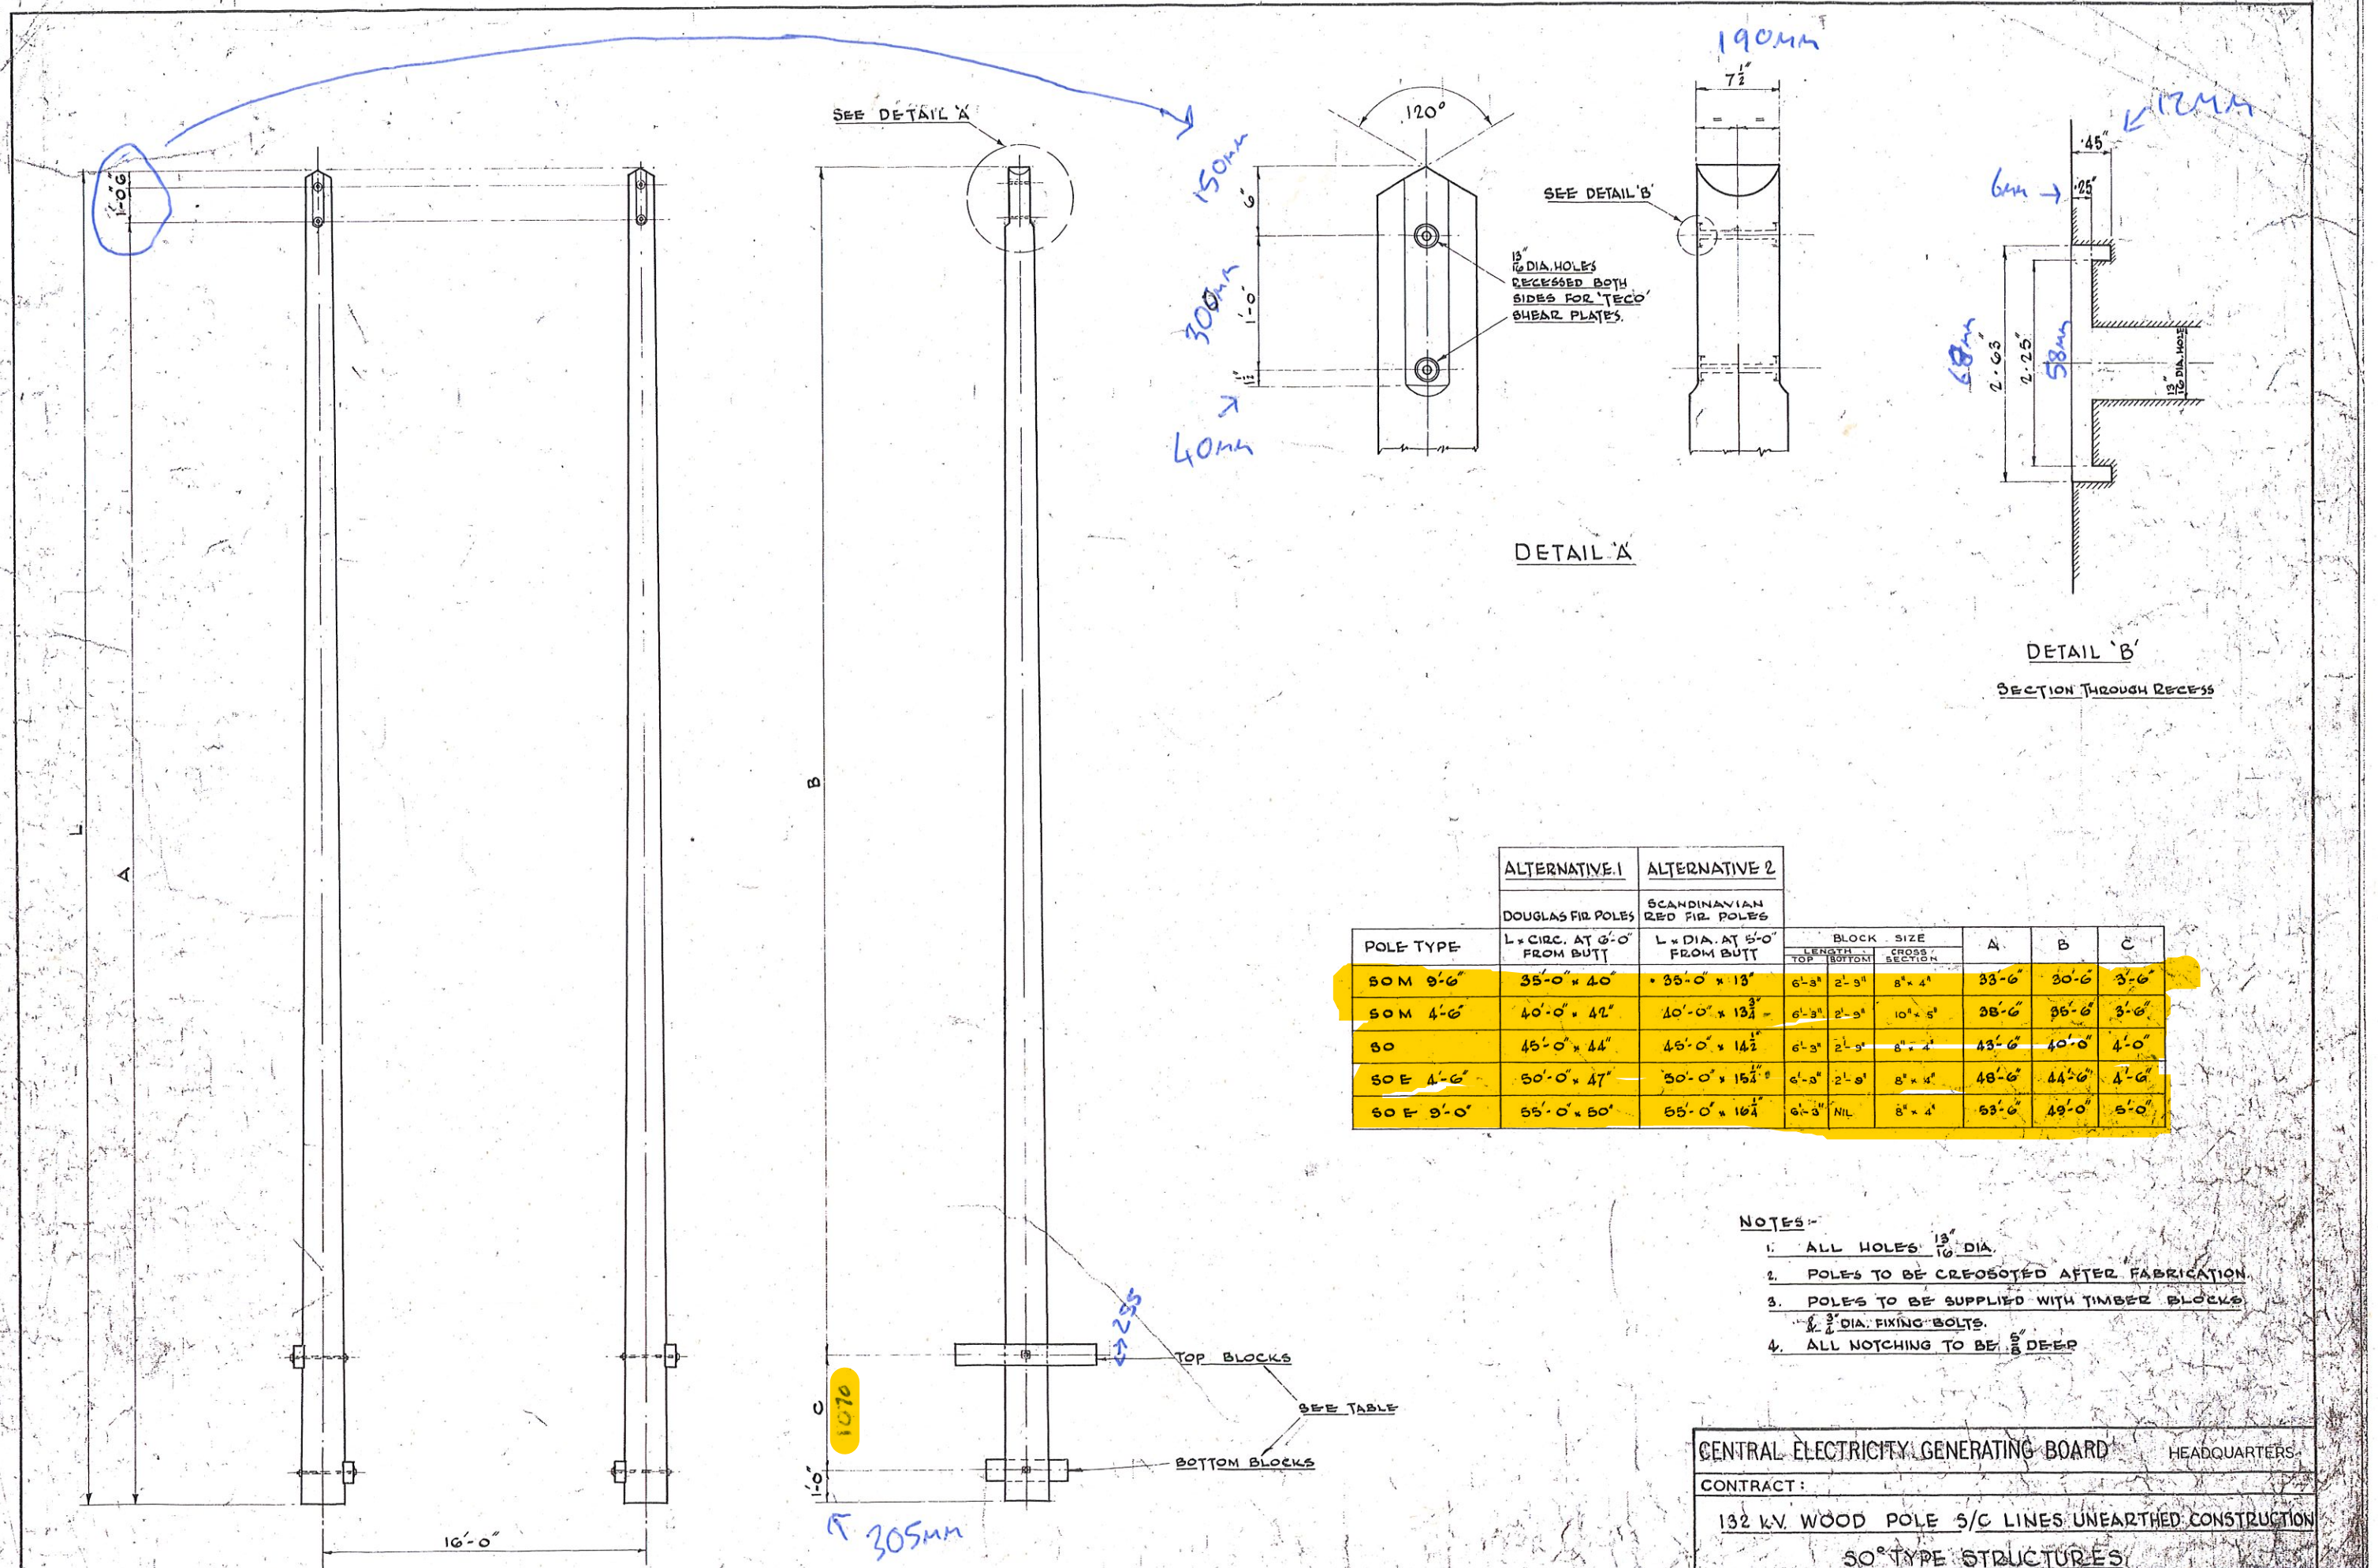

DETAIL 'A'

DETAIL 'B'
SECTION THROUGH RECESS

POLE TYPE	ALTERNATIVE 1	ALTERNATIVE 2	BLOCK SIZE			A	B	C
	DOUGLAS FIR POLES	SCANDINAVIAN RED FIR POLES	LENGTH		CROSS SECTION			
	L x CIRC. AT 6'-0" FROM BUTT	L x DIA. AT 5'-0" FROM BUTT	TOP	BOTTOM				
SOM 9'-6"	35'-0" x 40"	35'-0" x 13"	6'-3"	2'-3"	8" x 4"	33'-6"	30'-6"	3'-6"
SOM 4'-6"	40'-0" x 42"	40'-0" x 13 ³ / ₄ "	6'-3"	2'-3"	10" x 5"	28'-6"	26'-6"	3'-6"
SO	45'-0" x 44"	45'-0" x 14 ¹ / ₂ "	6'-3"	2'-3"	8" x 4"	43'-6"	40'-0"	4'-0"
SO E 4'-6"	50'-0" x 47"	50'-0" x 15 ¹ / ₂ "	6'-3"	2'-3"	8" x 4"	48'-6"	44'-6"	4'-6"
SO E 9'-0"	55'-0" x 50"	55'-0" x 16 ¹ / ₂ "	6'-3"	NIL	8" x 4"	53'-6"	49'-0"	5'-0"

- NOTES:-
1. ALL HOLES 13/16" DIA.
 2. POLES TO BE CREOSOTED AFTER FABRICATION.
 3. POLES TO BE SUPPLIED WITH TIMBER BLOCKS & 3/4" DIA. FIXING BOLTS.
 4. ALL NOTCHING TO BE 5/8" DEEP

CENTRAL ELECTRICITY GENERATING BOARD		HEADQUARTERS
CONTRACT:		
132 KV. WOOD POLE S/C LINES UNEARTHED CONSTRUCTION		
SO TYPE STRUCTURES		
FABRICATION DETAILS		
SCALE: 3/8" TO 1'-0", 1/2" TO 1'-0" & FULL SIZE		31/10/66

DRAWN	H. F. G.	31.10.57
TRACED	H. F. G.	31.10.57
CHECKED	H. F. G.	11-11-57

B	SOE 4'-6" AND SOE 9'-0" FOUNDATION BLOCK LENGTHS STANDARDISED	D.A.	A	FOUNDATION BLOCK SIZES MODIFIED TO INCREASE FO. FROM 2 1/2" TO 3 1/2" ON FOUNDATIONS	W.F.L.
---	---	------	---	--	--------