

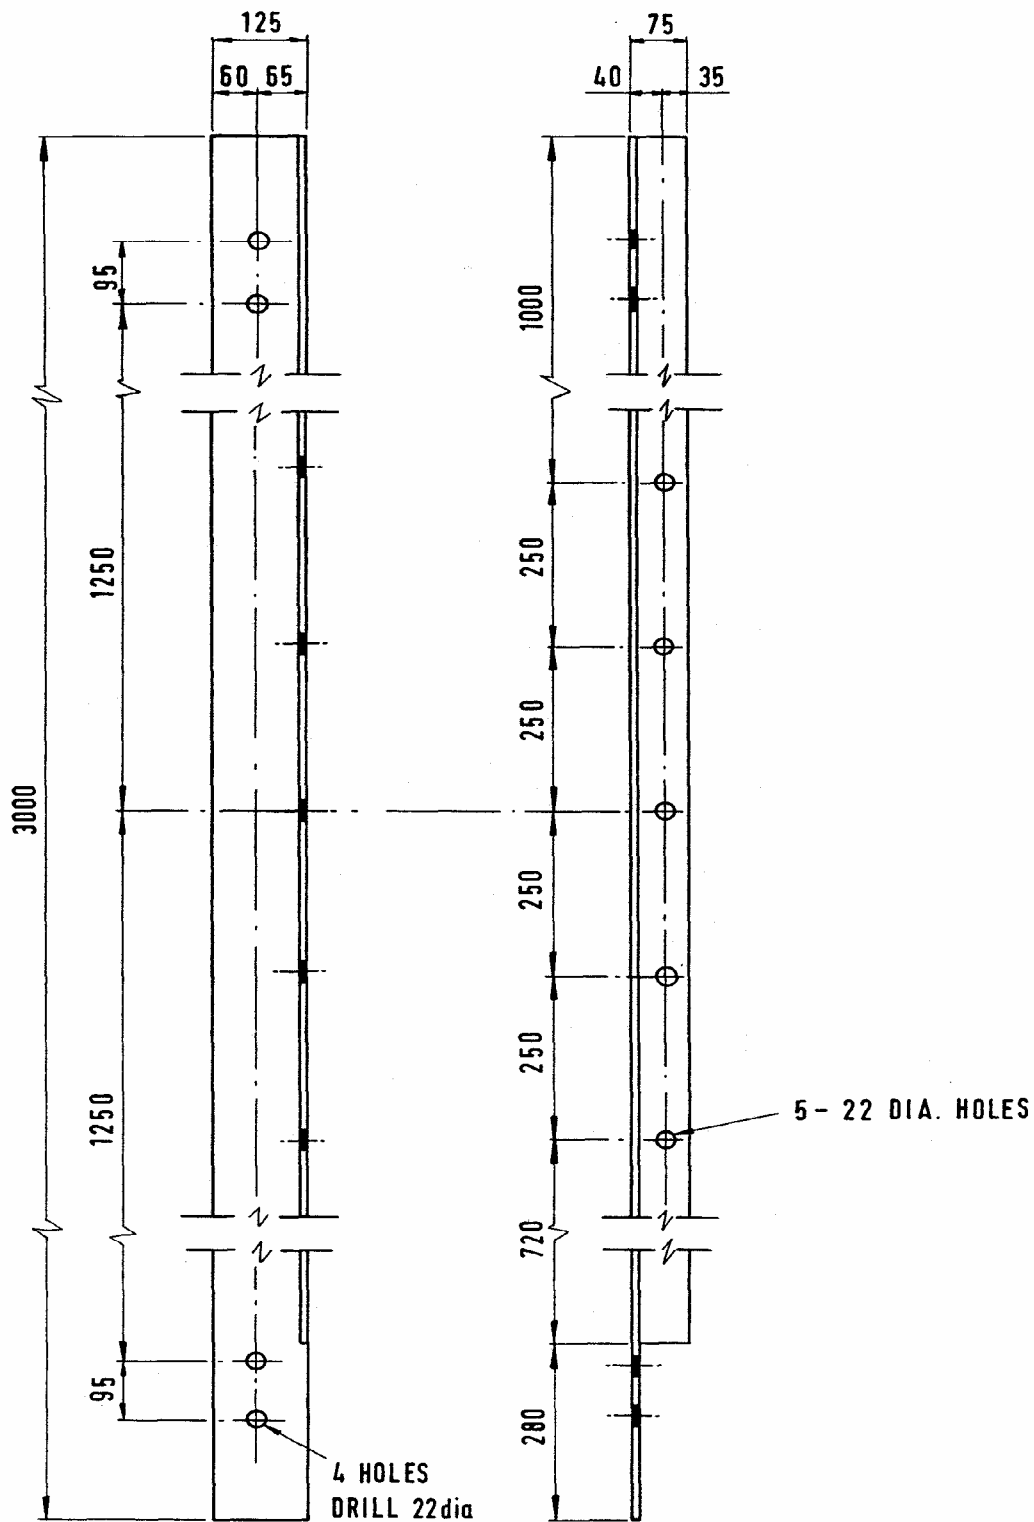


Figure 44: 'H' pole foundation brace
(ESI Drawing No. 439545)

(132 kV Lines to ESI Standard 43-50)