

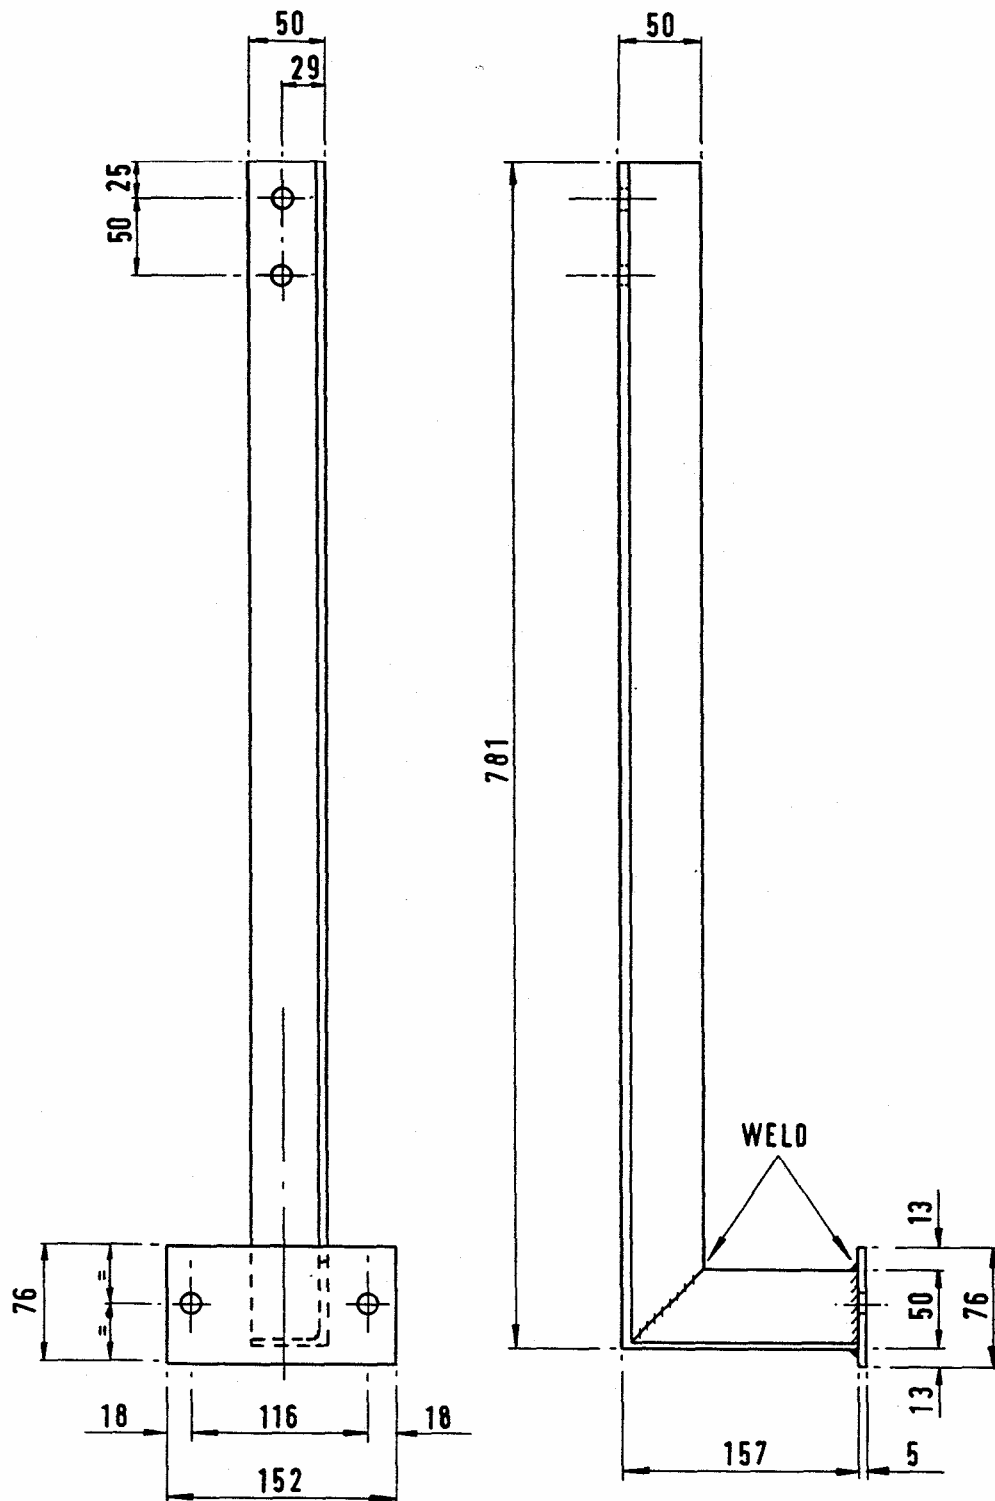


Figure 48: Cable cleat support details for 132 kV construction
(ESI Drawing No. 439549)

(132 kV lines to ESI Standards 43-50)