


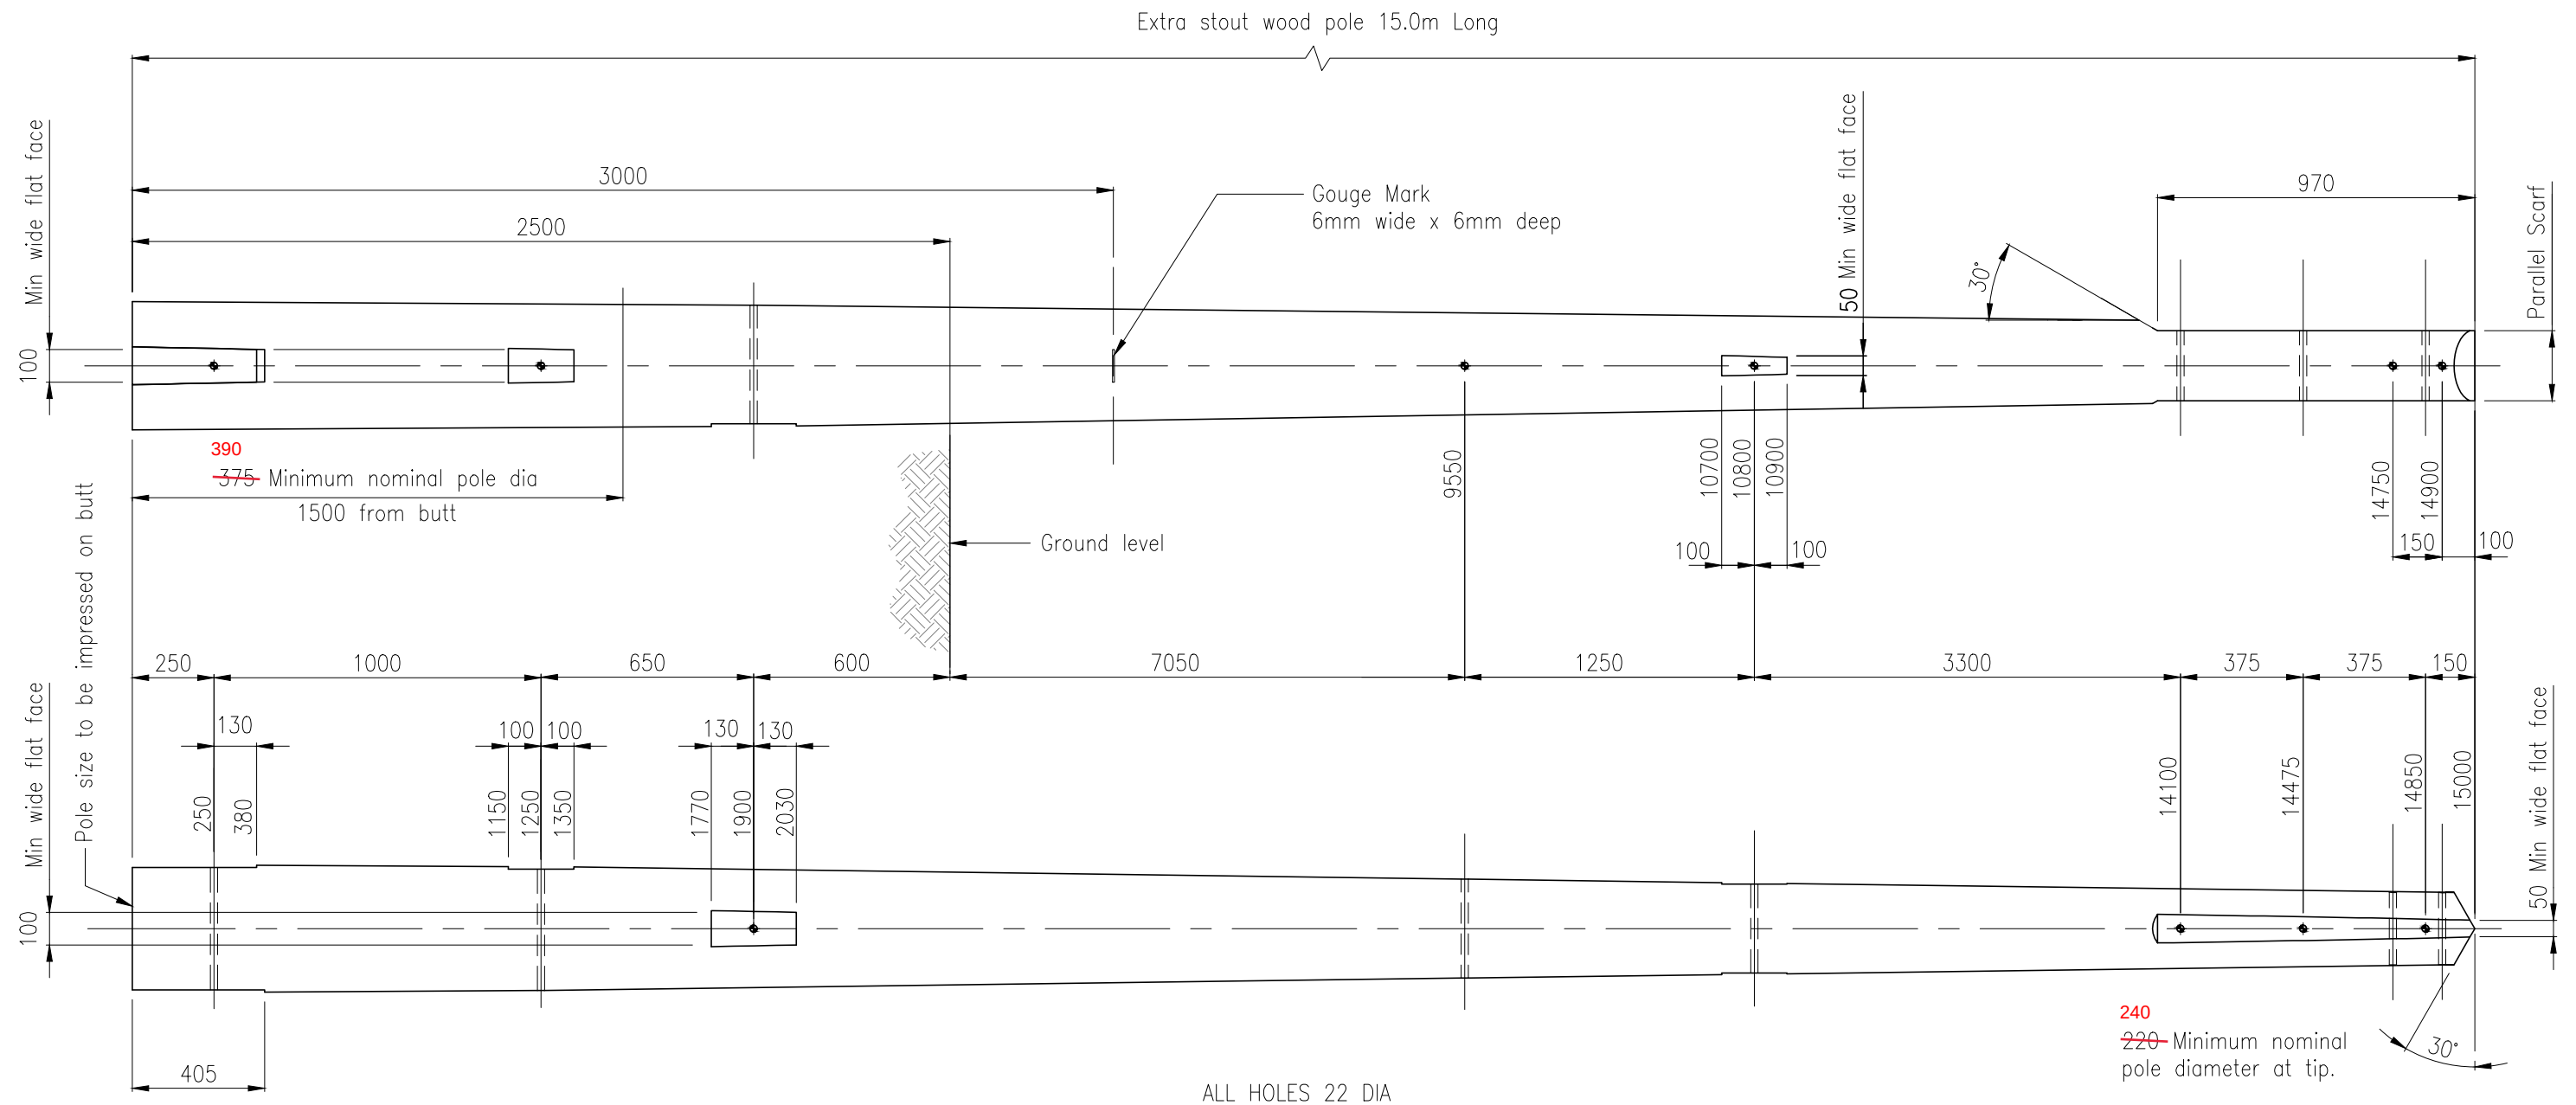

MARK PPS-017 REQUIRED AS DRAWN

This drawing is a metrication of details shown on drawing; N/A

Notes

- All dimensions in millimetres unless noted otherwise.
- All material shall be in accordance with the requirements of BS EN 10025.
- Galvanising shall be in accordance with BS EN ISO 1461.
- Welding shall be in accordance with BS EN 1011-2.
- All fabrication shall be in accordance with the requirements of E.N.A. TS 43-125, Issue 2, Part 4.
- This drawing to be read in conjunction with assembly drawing 90SS906-PGA-003.

TITLE

Piece Small Detail For MARK PPS-017
Specification TERMINAL POLE ASSEMBLY
Type
Position WOOD POLE



YORK HOUSE, 9 YORK PLACE, KNARESBOROUGH HG5 0AD
TEL: 01423-799950

(C) ENERGYLINE LTD. 2019 - THE COPYRIGHT IN THIS DRAWING & THE DESIGN RIGHT IN THE ARTICLE(S) DEPICTED BELONG TO ENERGYLINE LTD. THE DRAWING MAY NOT BE COPIED OR STORED BY ANY MEANS. NOR MAY ARTICLES BE MADE FROM THE DRAWING, EITHER DIRECTLY OR INDIRECTLY, WITHOUT THE PRIOR WRITTEN PERMISSION OF ENERGYLINE LTD.

Drawing status; Issued for construction

ROUTE /
CIRCUIT FORT AUGUSTUS - QUOICH

ENERGYLINE PROJECT DRG No.
90SS906-PPS-017

SHT No. No. of SHTS
1 1

CLIENT

CLIENTS PROJECT REF.
**

CLIENTS DRG No.
**

SCALE N.T.S.
ELEC FORM DWG

1 SHT SIZE A3

ISSUE DATE REVISION DRAWN CHK'D APP'D

1 25:06:19 Issued For Construction MCC JP SY