


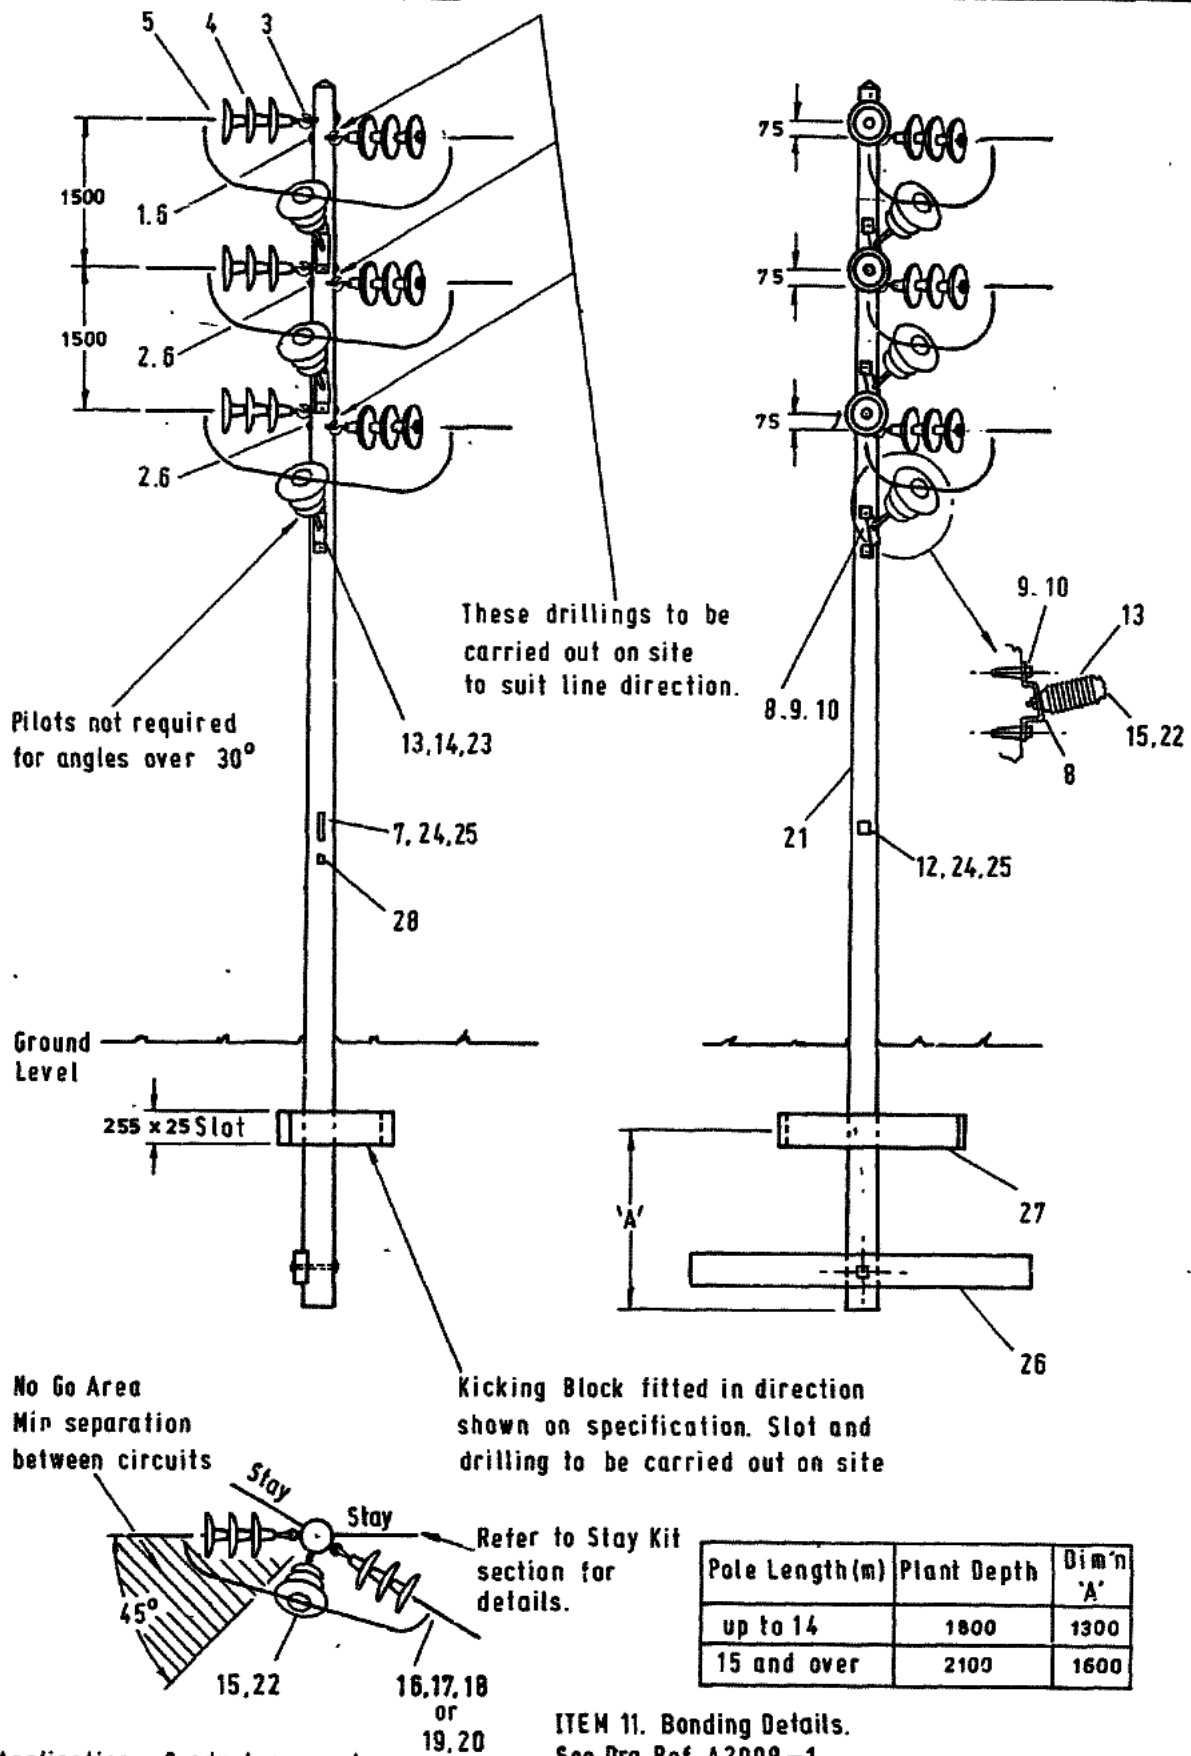

Application:- Conductors up to and including 175mm² ACAR.

Dimensions in Millimetres

ITEM 11. Bonding Details.

See Drg. Ref. A2008-1

Heavy Construction

Drawing Replaces:- 4/474 (part)

General Assembly 33kV Single Circuit (1500 Spacing). Single Section Angle Pole. Vertical Formation. Above 10°

Scale :- N.T.S.

Drn by :- D.K.W.

App by :- A.T.R.

Issue 1 / Sept-84

E.S.I.

Ref :-

Drawing

Ref :-

A2008