


southern electricity

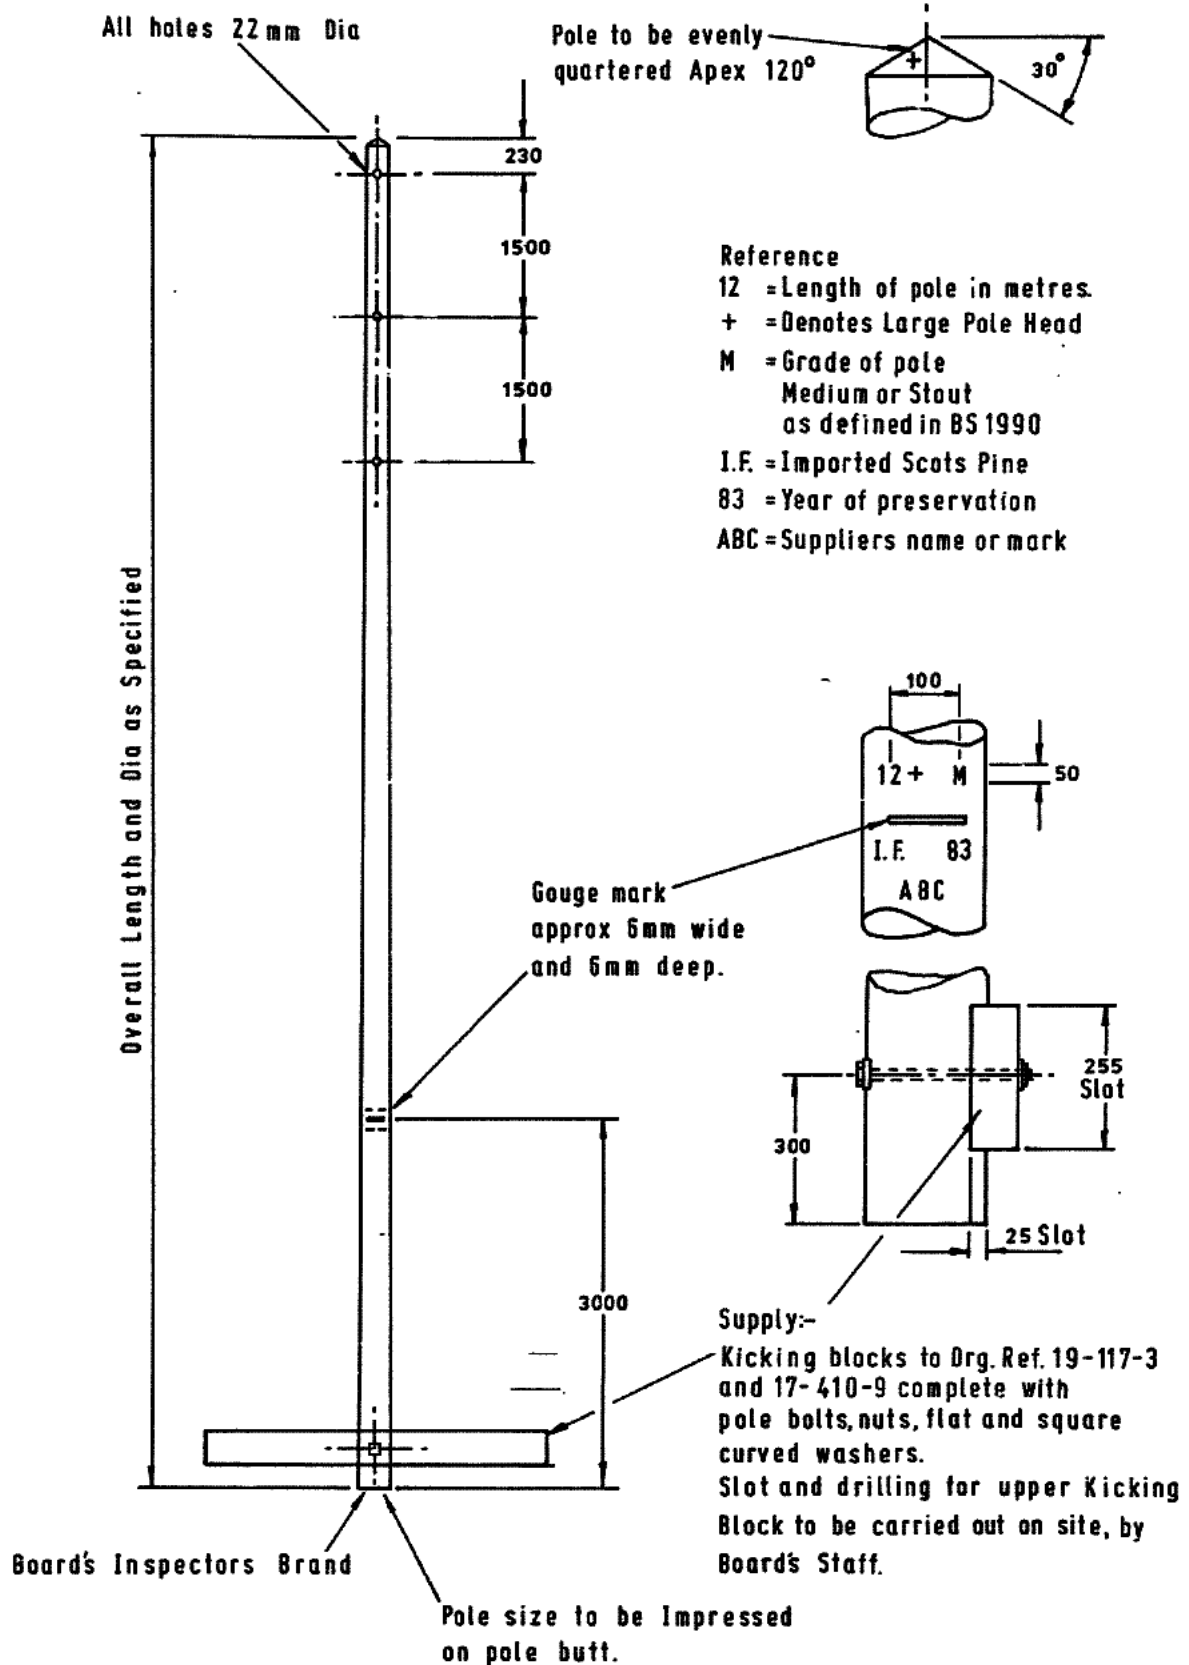

Heavy Construction

Dimensions in Millimetres

Drawing Replaces:- 4/474 (part)

Pole Drilling and Marking.
 33kV Single Circuit. (1500 Spacing)
 Single Pole Vertical Formation

Scale :- N.T.S.

E.S.I.

Drn by :- D.K.W.

Ref :-

App by :- A.T.R.

Drawing

Issue 1 / Sept-84

Ref :-

A2008-2