


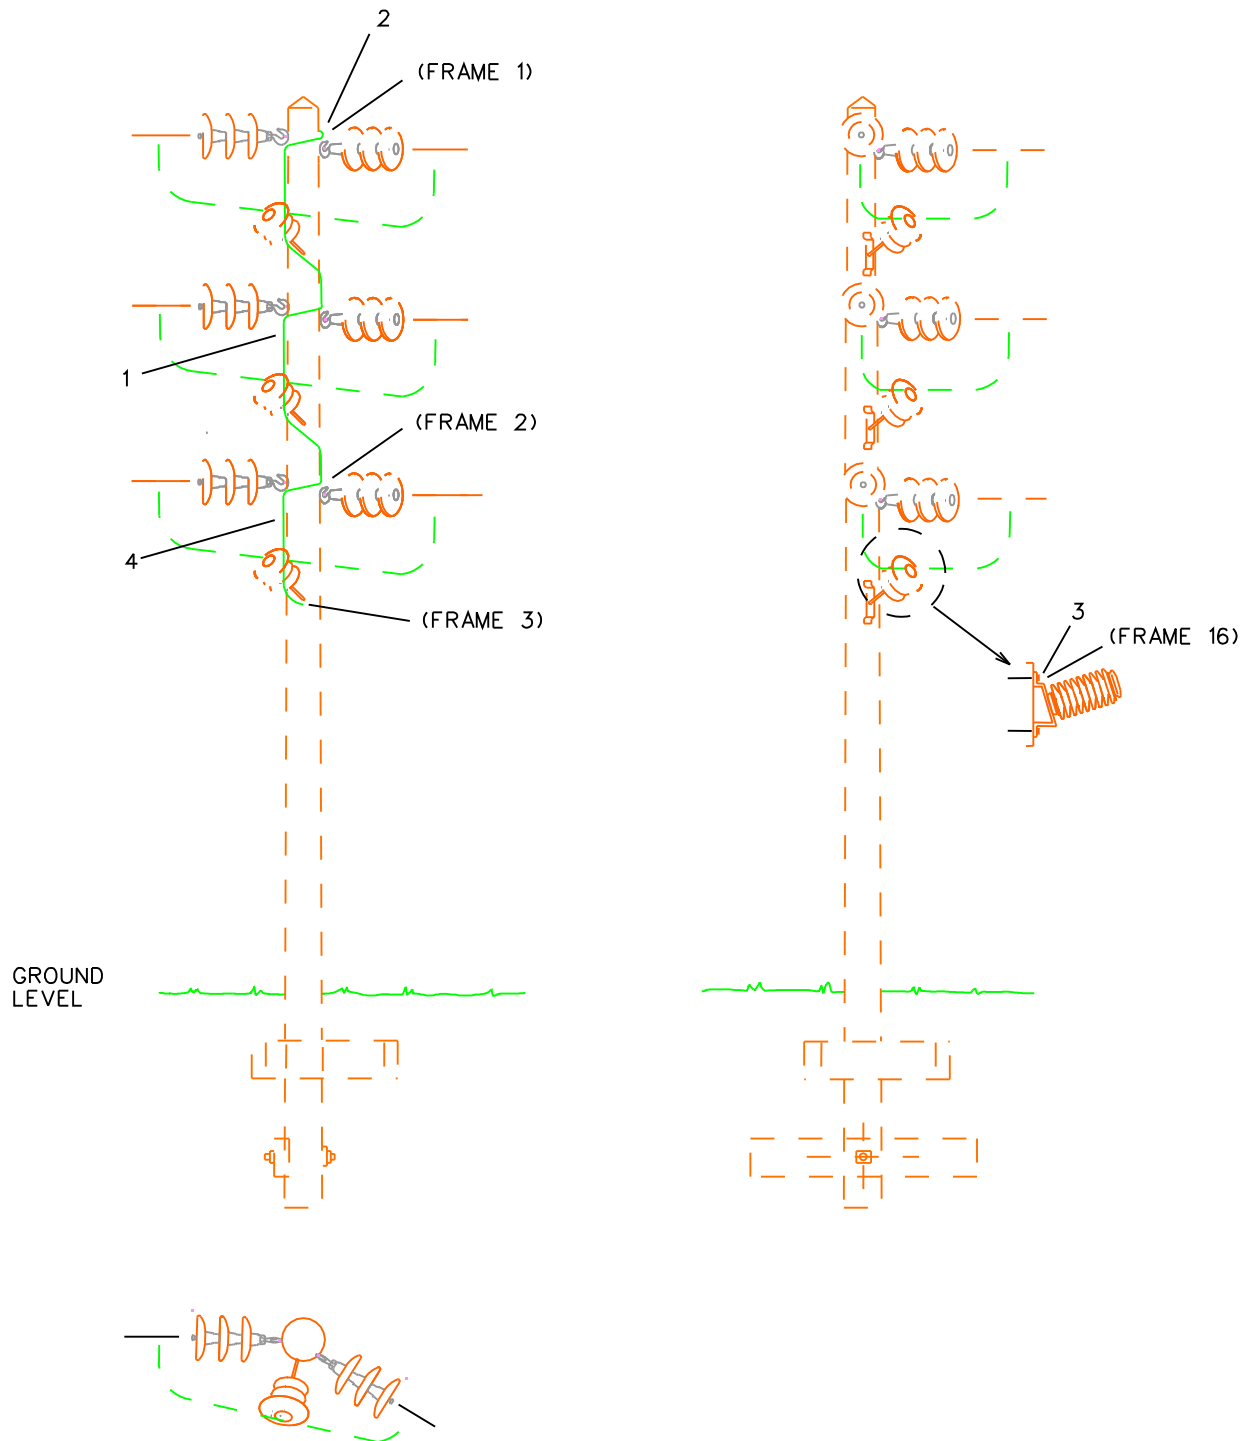

BONDING AND EARTHING CONNECTION  
TO DR. No. HO/39/4206 FRAME NUMBER  
AS SHOWN IN BRACKETS.

SCHEDULE:- E2009  
33kV HEAVY CONSTRUCTION  
SUPERSEDES DRG REF A2009-1

This drawing is protected by copyright and the information contained therein is confidential. The drawing may not be copied and the information contained therein may not be used, or disclosed to a third party wholly or in part except with the written permission of, and in the manner prescribed by SOUTHERN ELECTRIC plc c 1992 2

 **SSE Power Distribution**

**33kV SINGLE CIRCUIT (1800 SPACING)  
SINGLE SECTION ANGLE POLE. VERTICAL  
FORMATION ABOVE 10° BONDING DETAILS**

|           |        |                              |
|-----------|--------|------------------------------|
| Scale:-   | N.T.S. | Dimensions in millimetres    |
| Drn. by:- | D.K.W. | Drawing no.                  |
| Tcd. by:- | D.K.M. | <b>HO/37/2009 SHT 2 OF 3</b> |
| Ckd. by:- | W.C.S. | C.A.D. Reference. HO2009.37  |
| App. by:- | W.C.S. |                              |

A4P

DATE PLOTTED \$\$\$\$date\$\$\$