


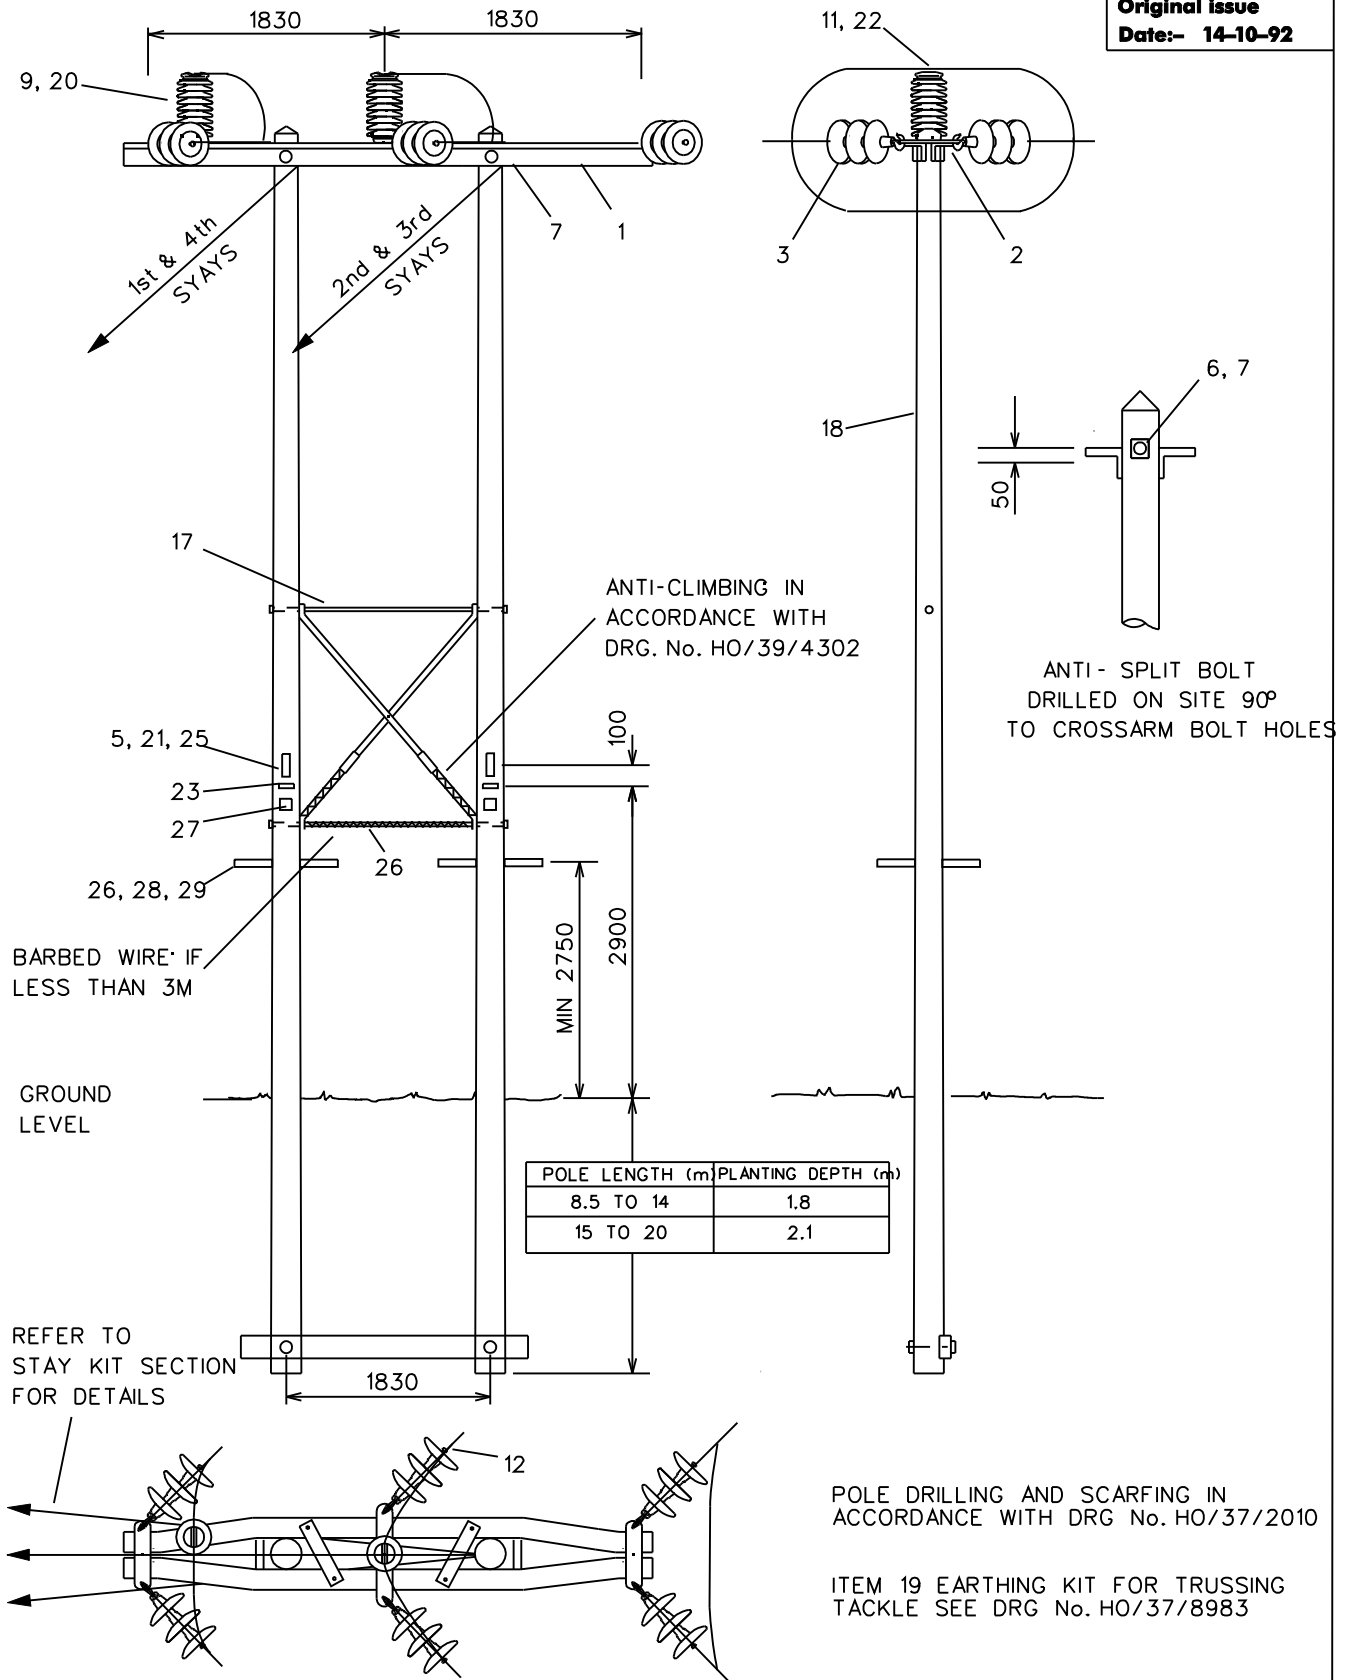

LIMITATION:- MAX ANGLE 60°

APPLICATION:- ALL CONDUCTORS UP TO AND INCLUDING 0.2sq.in CU, 250sq.mm. AAA

33kV HEAVY CONSTRUCTION

SCHEDULE:- A2016

SUPERSEDES DRG No :- 4/11 TYPE Z

This drawing is protected by copyright and the information contained therein is confidential. The drawing may not be copied and the information contained therein may not be used, or disclosed to a third party wholly or in part except with the written permission of, and in the manner prescribed by SOUTHERN ELECTRIC plc c 199 2

SSE Power Distribution

GENERAL ASSEMBLY
33kV SINGLE CIRCUIT, ANGLE/SECTION
H POLE

Scale:-	N.T.S.	Dimensions in millimetres
Drn. by:-	D.K.W.	Drawing no.
Tcd. by:-	D.K.M.	HO /37 /2016
Ckd. by:-	W.C.S.	C.A.D.Reference. HO2016.37
App. by:-	W.C.S.	

A4P

DATE PLOTTED \$\$\$\$date\$\$\$