


Original Issue
Date:- OCT 92

ISSUE 1
POLE MARKING &
ROOFING ADDED.
D.K.M. MAR 93

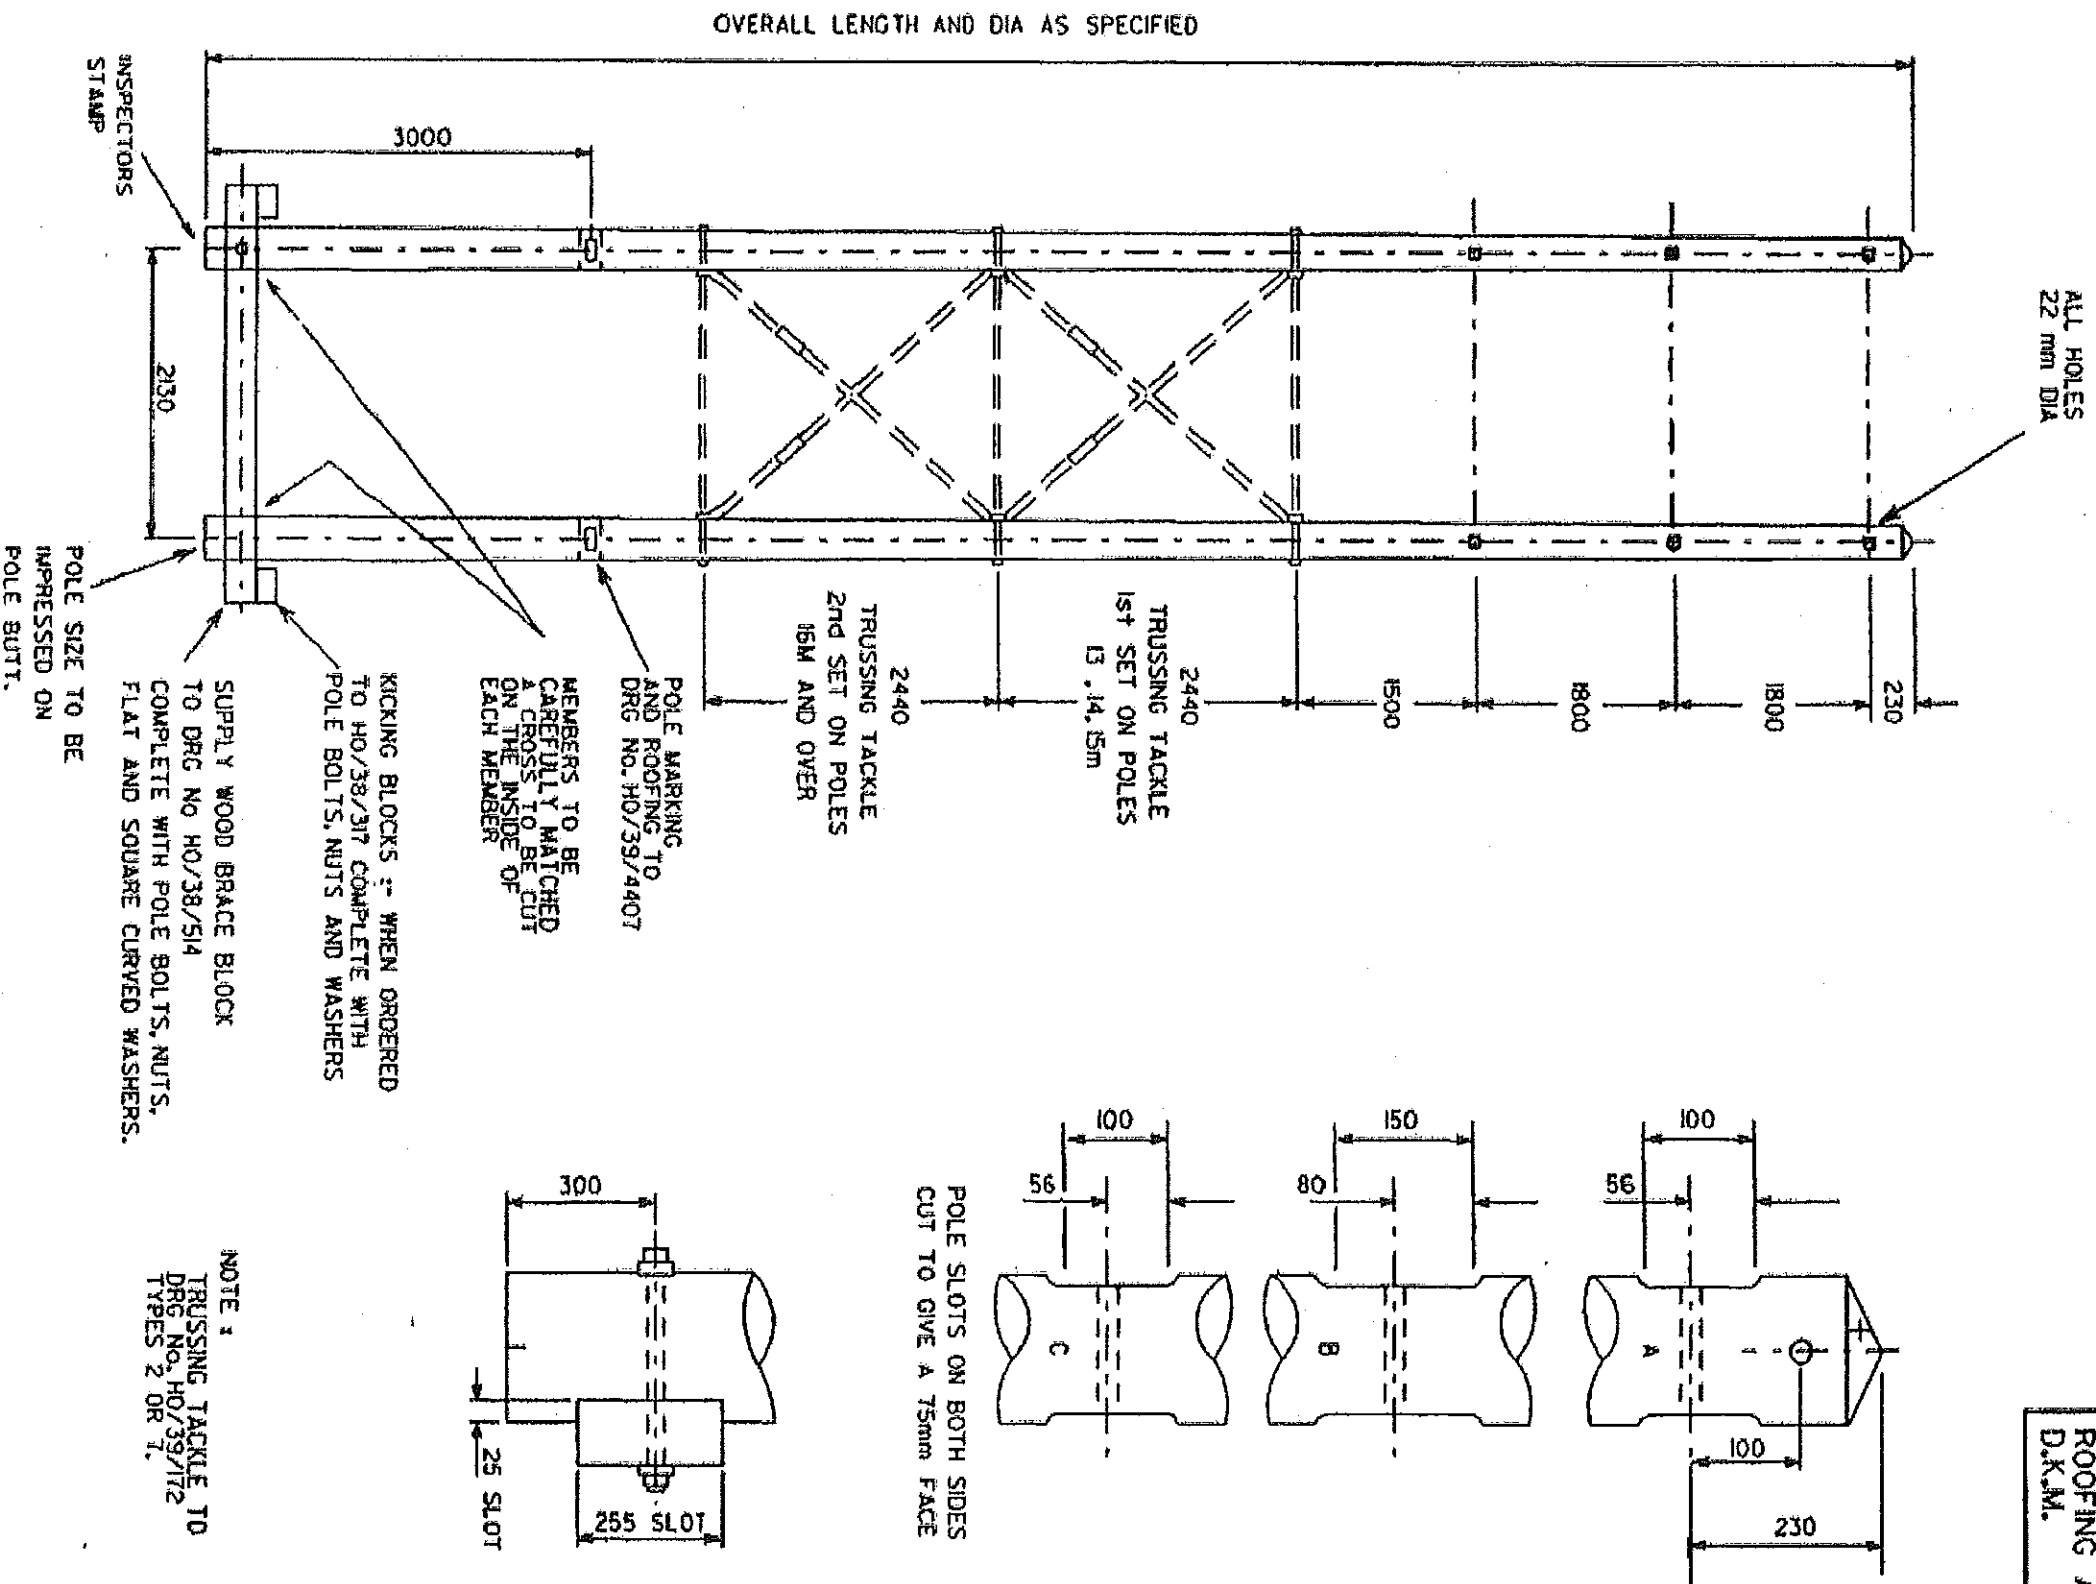

This drawing is protected by copyright and the information contained therein is confidential. The drawing may not be copied or the information contained therein may not be used or disclosed to a third party wholly or in part except with the written permission of, and in the manner prescribed by SOUTHERN ELECTRIC Pte © 1992



**SOUTHERN
ELECTRIC**

SCHEDULE:- P6004
33KV HEAVY CONSTRUCTION
SUPERSEDES DRG REF:- A6004-2

**POLE DRILLING, SCARFING AND MARKING
33KV DOUBLE CIRCUIT
SECTION 'H' POLE, 1800 SPACING**

Scale:-		Dimensions in millimetres	
Dtn. by:-	D.K.W.	Drawing no. HO/37/6004 sht 3 of 3 C.A.D. Reference, HO6004.37	
Ted. by:-	D.K.M.		
App. by:-	W.C.S.		

AAP

DATE PLOTTED 27-OCT-1993