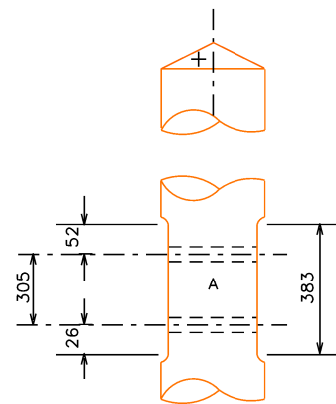
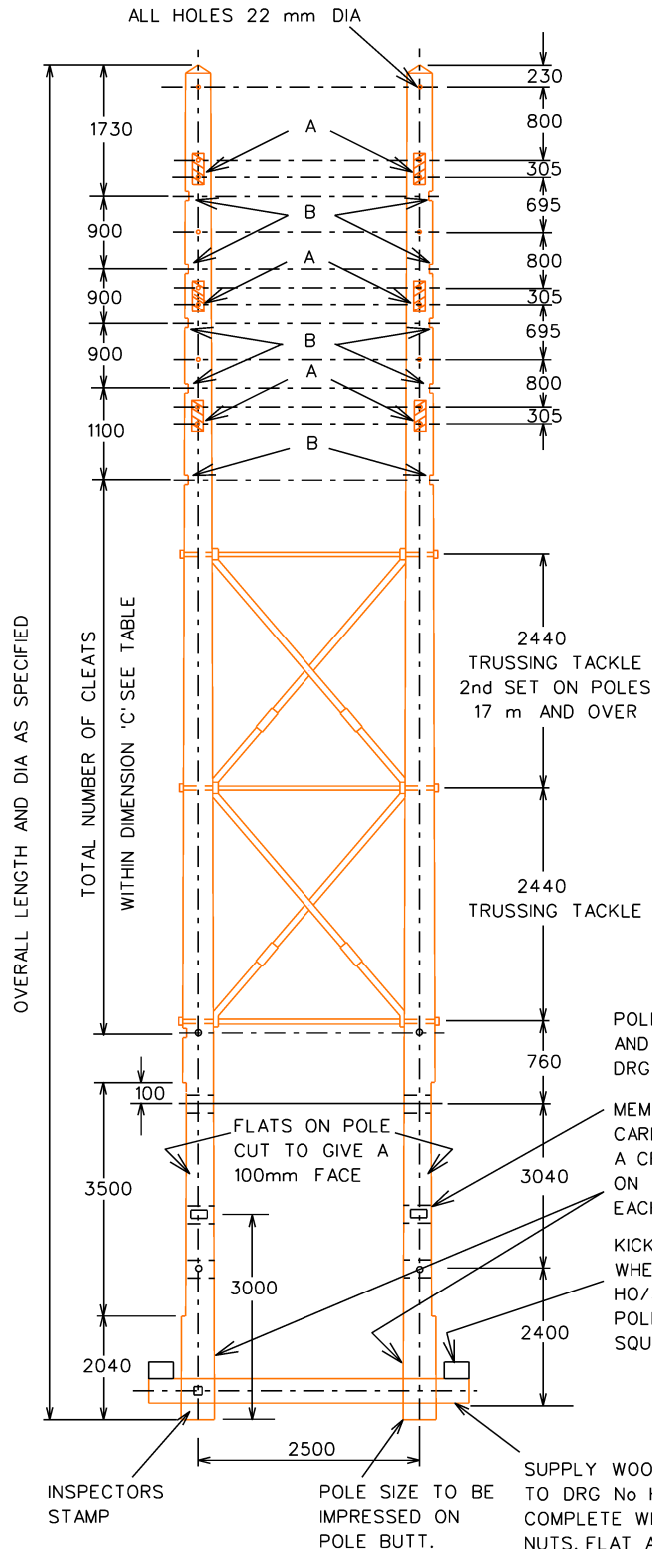
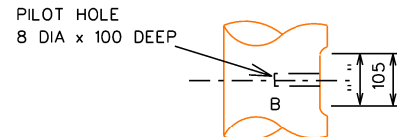
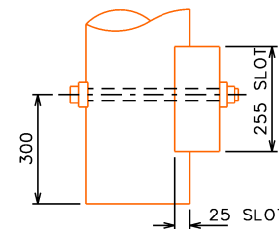


POLE SLOTS ON BOTH SIDES
CUT TO GIVE A 100mm FACEPILOT HOLE
8 DIA x 100 DEEPPOLE FLATS ON ONE SIDE
CUT TO GIVE A 100mm FACE
FOR ALL CLEAT POSITIONSPOLE MARKING
AND ROOFING TO
DRG No. HO/39/4407MEMBERS TO BE
CAREFULLY MATCHED
A CROSS TO BE CUT
ON THE INSIDE OF
EACH MEMBERKICKING BLOCKS:-
WHEN ORDERED TO DRG No.
HO/38/317 COMPLETE WITH
POLE BOLTS, NUTS, FLAT AND
SQUARE CURVED WASHERS

POLE LENGTH	DIM'N 'C'	TOTAL No OF CLEATS (EQUALLY SPACED)
14m	2470	2
15m	3470	3
16m	4470	4
17m	5470	5
18m	6470	6

SUPPLY WOOD BRACE BLOCK
TO DRG No HO/38/515
COMPLETE WITH POLE BOLTS,
NUTS, FLAT AND SQUARE
CURVED WASHERSSCHEDULE- P6005
33kV HEAVY CONSTRUCTION
SUPERSEDES DRG REF:- A6005-2SUPPLY:- TRUSSING TACKLE TO
DRG No. HO/39/172 TYPE 4 OR 9UNCONTROLLED COPY
SUBJECT TO REVISION
MASTER HELD AT HEAD OFFICE
Telephone\$\$\$\$elec\$\$\$\$\$

Revision:-

This drawing is protected by copyright and the information contained therein is confidential. The drawing may not be copied and the information contained therein may not be used, or disclosed to a third party wholly or in part except with the written permission of, and in the manner prescribed by SOUTHERN ELECTRIC plc c 1990 ee

SOUTHERN
Z V X Q Y W I QPOLE DRILLING SCARFING AND MARKING
33kV DOUBLE CIRCUIT
'H' TERMINAL POLE (CABLE)Scale:- N.T.S.
Dn. by:- D.K.W.
Tcd. by:- D.K.M.
Ckd. by:- W.C.S.
App. by:- W.C.S.Dimensions in millimetres
Drawing no.
HO/37/6005 5 OF 5
C.A.D. Reference H06005.37