




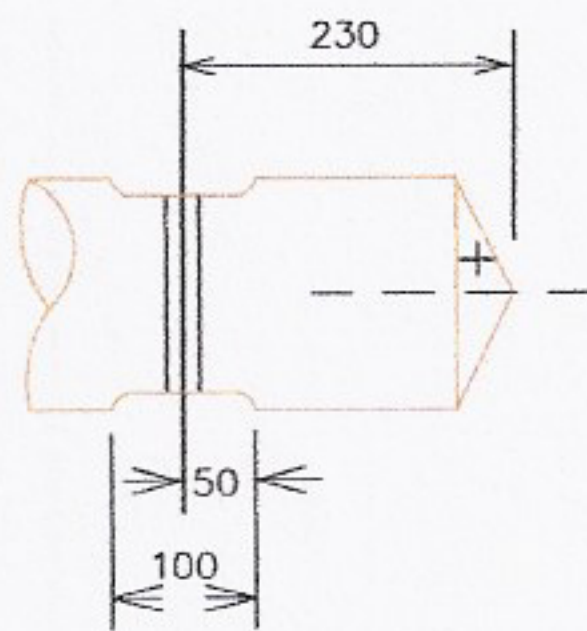

DETAIL 'A'

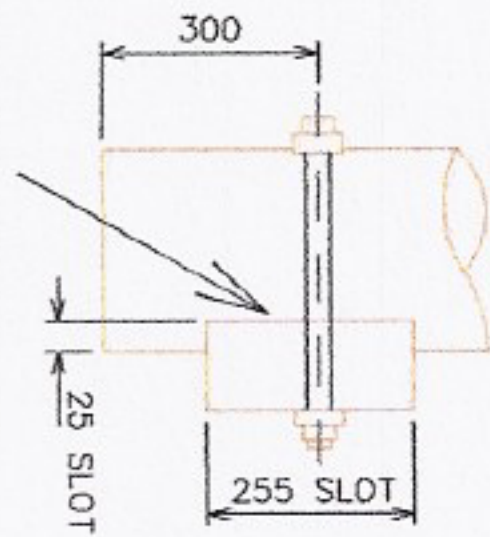

DETAIL 'B'

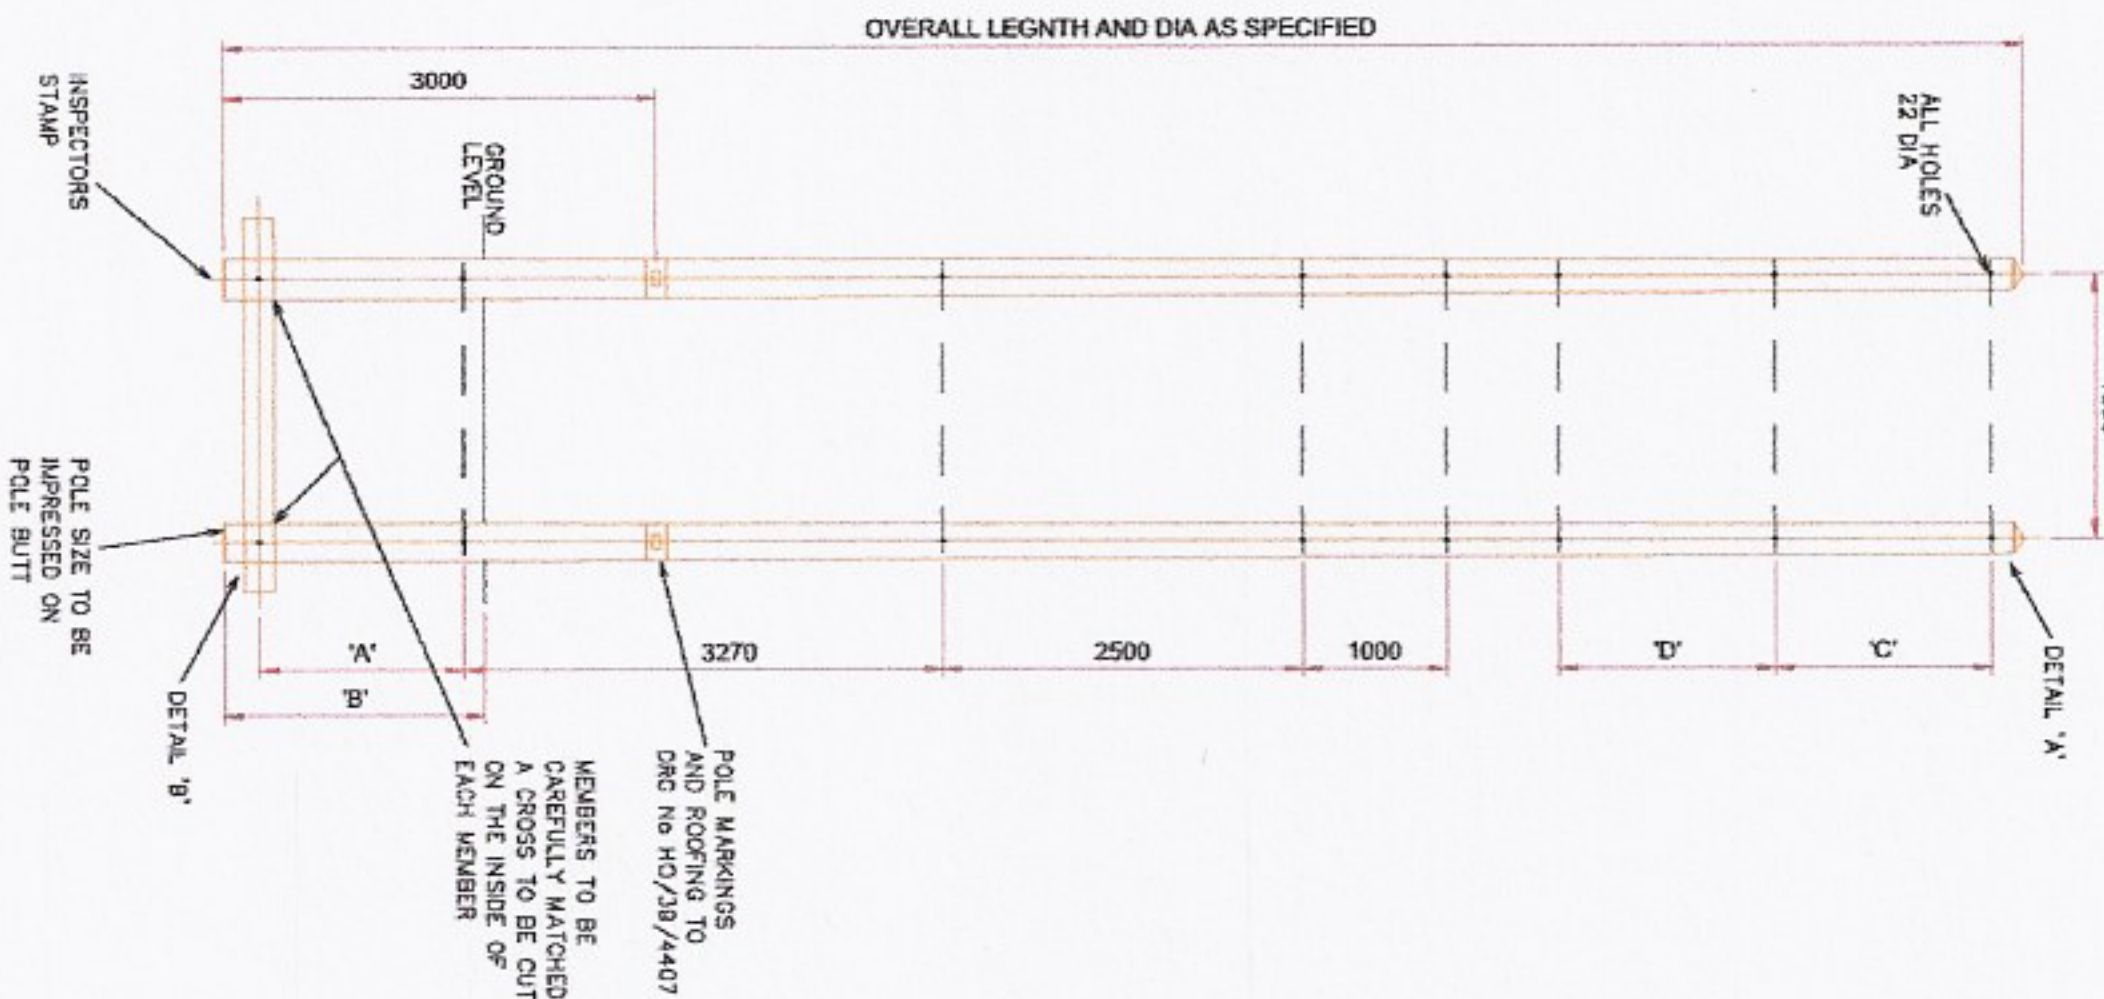

- GENERAL NOTE:
- ALL DIMENSIONS ARE IN MILLIMETRES UNLESS NOTED OTHERWISE
 - IF TOTAL POLE HEIGHT EXCEEDS 11 METRES ADDITIONAL CROSSBARS SUPPORTS MUST BE USED
 - IF TOTAL POLE HEIGHT EXCEEDS 15 METRES TWO ADDITIONAL CROSSBARS SUPPORTS MUST BE USED
 - IF TOTAL POLE HEIGHT EXCEEDS 15 METRES TWO ADDITIONAL CROSSBARS SUPPORTS MUST BE USED

- CON NOTE:
- ONLY COMPETENT / EXPERIENCED CONTRACTORS SHALL BE APPOINTED TO UNDERTAKE THIS WORK
 - THIS DRAWING IS TO BE READ IN CONJUNCTION WITH PROJECT SPECIFICATION AND ANY OTHER RELEVANT DOCUMENTS
 - CONTRACTOR SHALL CONSIDER ALL PHASES OF WORK AND ENSURE LIMITS OF APPROACH ARE ADHERED TO
 - CONTRACTOR SHALL ADHERE TO ALL ELECTRICITY COMPANIES OPERATIONAL PROCEDURES
 - CONTRACTOR SHALL HAVE ASSESSED RISKS AND USE SAFE METHODS OF WORKING TO COMPLY WITH COMPANY POLICY AND SAFETY LEGISLATION AND CONSTRUCTION
 - THE CONTRACTOR SHALL HAVE TAKEN DUE CONSIDERATION OF THE HAZARDS IDENTIFIED IN THE DESIGN PARTICULARLY WHEN WORKING AT HEIGHT AND ELECTROCUSSION AND SHALL HAVE IMPLEMENTED MITIGATION MEASURES TO REDUCE RISKS TO ACCEPTABLE LEVEL

DIMENSIONS				
POLE LENGTH	'A'	'B'	'C'	'D'
10-11m	1120	1800	N/A	N/A
12-13m	1120	1800	2000	N/A
14-15m	1420	2100	3000	N/A
16m	1420	2100	2500	2500
17m	1420	2100	3000	3000
18m	1420	2100	3500	3500

17.5m
Required.

LEGEND/ NOTES

REV	DESCRIPTION	DRN	APPD	DATE
0	ORIGINAL ISSUE - CH3913	-	-	25-01-17



Scottish & Southern
Electricity Networks

UNCONTROLLED COPY
SUBJECT TO REGION
MASTER HELD AT
WESTERN ROAD
TEL 0178 830 488

This drawing is protected by copyright and the information contained therein is confidential. The drawing may not be copied and the information contained therein may not be disclosed to a third party without the prior written permission of Scottish & Southern Electricity Networks. In the manner provided by SCOTTISH AND SOUTHERN ENERGY PLC © 2017

PROJECT NUMBER
STANDARD ARRANGEMENT

DRAWING TITLE

GENERAL ARRANGEMENT / ERECTION DIAGRAM
FOR H-POLE WITH CABLE TERMINATIONS
POLE DRILLING, SCARFING AND MARKING

SUITABILITY DESCRIPTION
FIT FOR CONSTRUCTION APPROVAL

CODE
S4

DRAWN
D.RANDALL

CHECKED
-

APPROVED
C.SMART

DRAWING NUMBER
MP / 37 / 2644

SHEET
2 / 3

SCALE (@A1)
1:50

REV
0

NOT FOR CONSTRUCTION
PROGRESS