


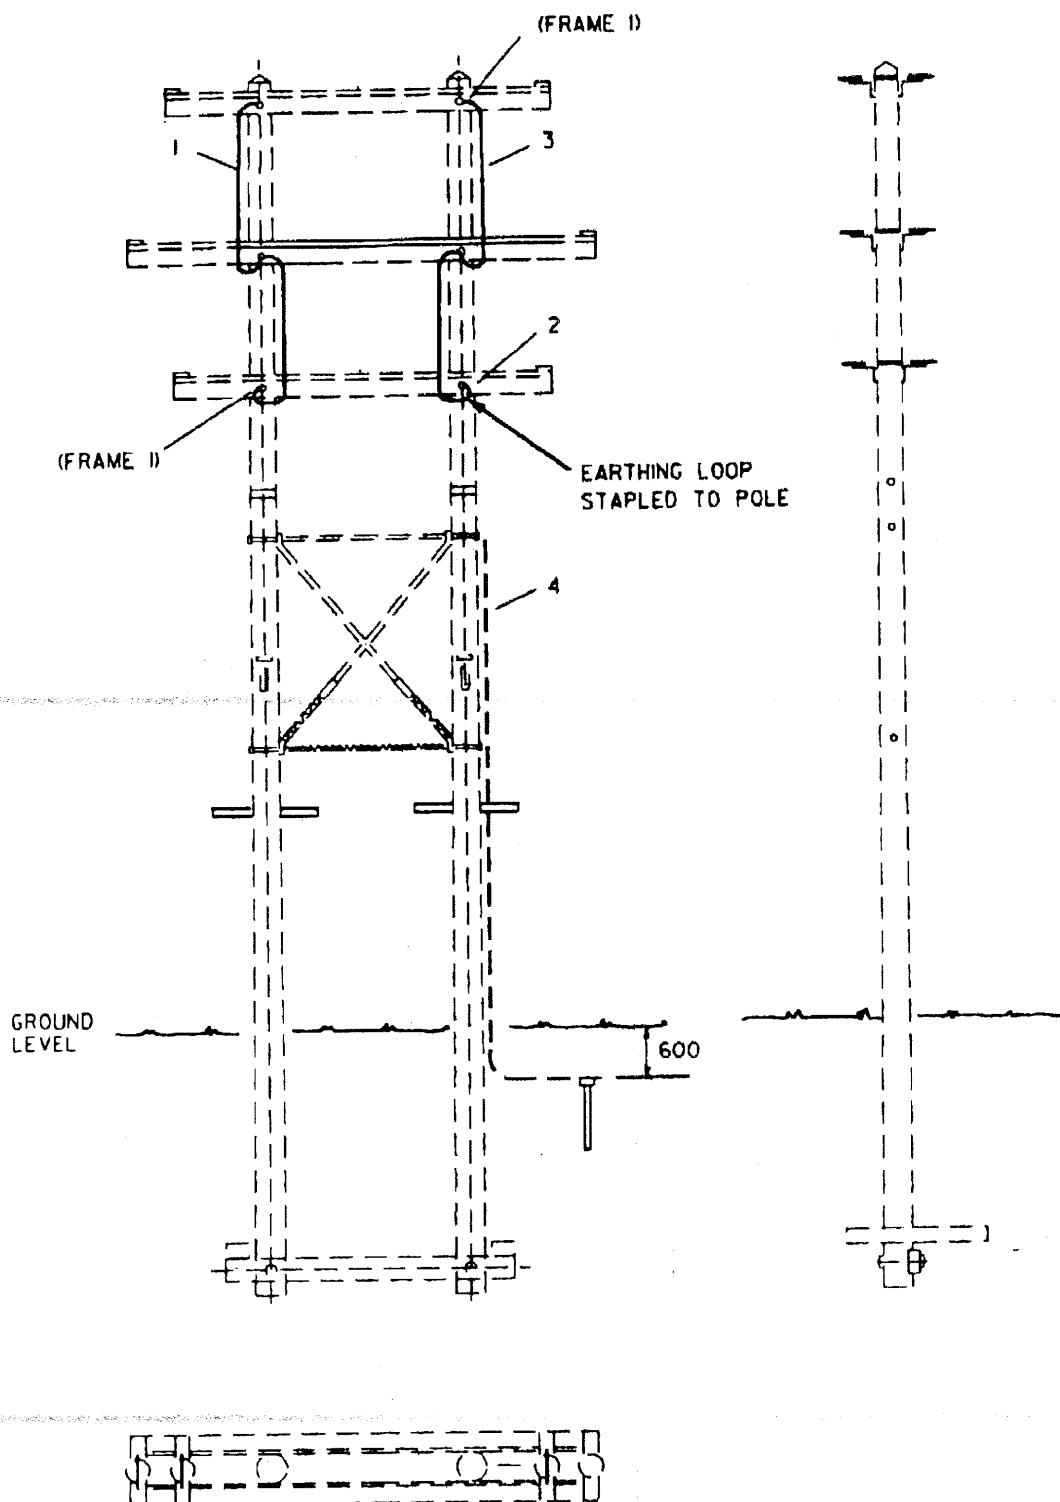

BONDING AND EARTHING CONNECTIONS
TO DRG NO. HO/37/4206 FRAME NUMBERS
AS SHOWN IN BRACKETS

SCHEDULE:- E6002
33kv HEAVY CONSTRUCTION
SUPERSEDES DRG REF:- A6002-1

This drawing is protected by copyright and the information contained therein is confidential. The drawing may not be copied and the information contained therein may not be used, or disclosed to a third party wholly or in part except with the written permission of, and in the manner prescribed by SOUTHERN ELECTRIC plc © 1992



**SOUTHERN
ELECTRIC**

**33kV DOUBLE CIRCUIT
INTERMEDIATE 'H' POLE 1800 PH. SPACING
BONDING DETAILS**

Scale:- N.T.S.
Drm. by:- D.K.W.
Tod. by:- D.K.M.
Ckd. by:- W.C.S.
App. by:- W.C.S.

Dimensions in millimetres

Drawing no.
HO/37/6002 SHT 2 OF 3
C.A.D. Reference. HO6002.37

