

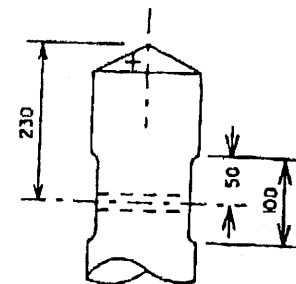


Original Issue
Date: FEB 97

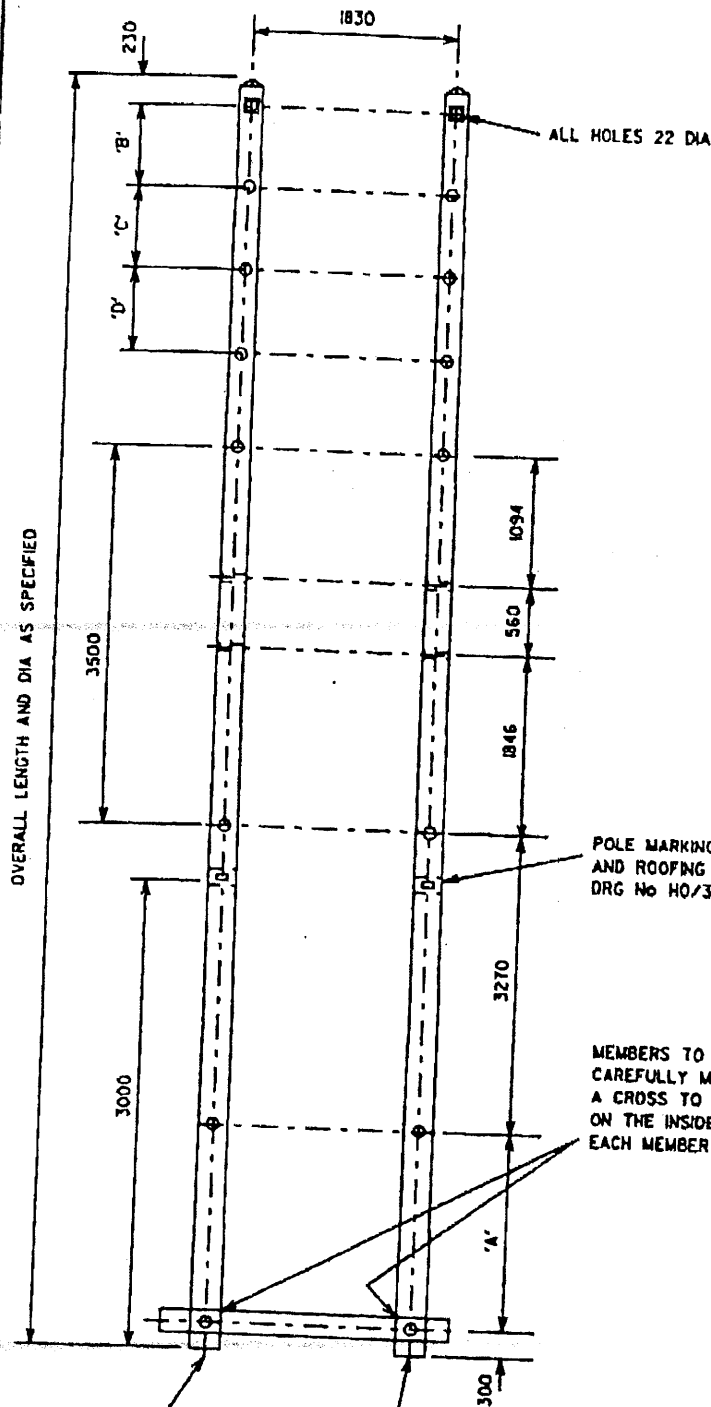

POLE SLOTS ON BOTH SIDES
CUT TO GIVE A 50mm FACE

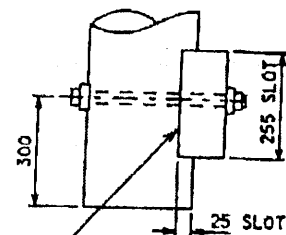

SUPPLY WOOD BRACE BLOCK
TO DRG No HO/38/513
COMPLETE WITH POLE BOLTS,
NUTS, FLAT AND SQUARE WASHERS

POLE LENGTH	DIMENSION			
	'A'	'B'	'C'	'D'
10-11m	1120	—	—	—
12-13m	1120	2040	—	—
14-15m	1420	2090	2090	—
16m	1420	2430	2430	—
17m	1420	2760	2760	—
18m	1420	2320	2320	2320

SCHEDULE- P2021
33kV HEAVY CONSTRUCTION

This drawing is protected by copyright and the information contained therein is confidential. The drawing may not be copied and the information contained therein may not be used or disclosed to third party wholly or in part except with the written permission and in the manner prescribed by SOUTHERN ELECTRIC plc ©1997



**SOUTHERN
ELECTRIC**

**POLE DRILLING SCARFING AND MARKING
33kV 'H' TERMINAL POLE (POLYMERIC CABLE)
HEAVY CONSTRUCTION**

Scale: N.T.S.
Drm. by: HMW
Tel. by:
Ckd. by: W.C.S.
App. by: W.C.S.

Dimensions in millimetres

Drawing no.
HQ37/2021 SHT 3 OF 3
C.A.D. Reference. HQ2021.37

