


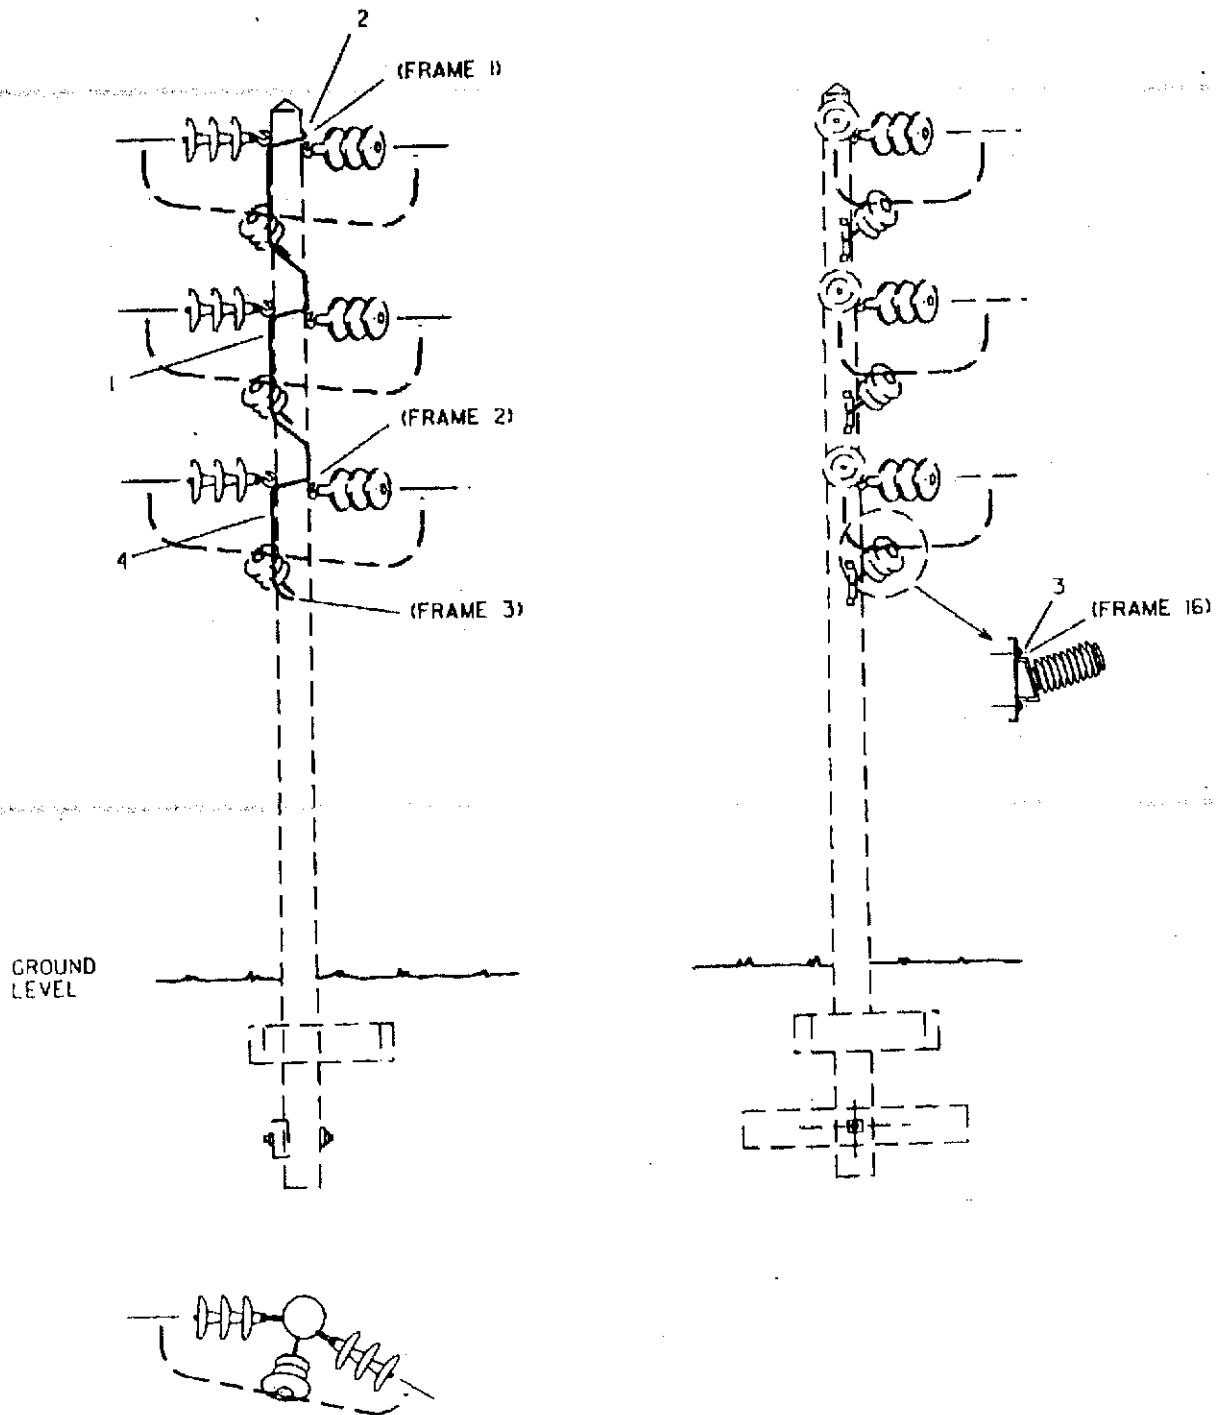

BONDING AND EARTHING CONNECTION
TO DR. No. HO/39/4206 FRAME NUMBER
AS SHOWN IN BRACKETS.

SCHEDULE:- E2009
33kV HEAVY CONSTRUCTION
SUPERSEDES DRG REF A2009-1

This drawing is protected by copyright and the information contained therein is confidential. The drawing may not be copied and the information contained therein may not be used or disclosed to a third party wholly or in part except with the written permission of, and in the manner prescribed by SOUTHERN ELECTRIC plc © 1992



**SOUTHERN
ELECTRIC**

**33kV SINGLE CIRCUIT (1800 SPACING)
SINGLE SECTION ANGLE POLE. VERTICAL
FORMATION ABOVE 10° BONDING DETAILS**

Scale:- N.T.S.
Dm. by:- D.K.W.
Yed. by:- D.K.M.
Ckd. by:- W.C.S.
App. by:- W.C.S.

Dimensions in millimetres

Drawing no.
HO/37/2009 SHT 2 OF 3
C.A.D. Reference. HO2009.37