


Original Issue
Date:- OCT 92

ISSUE 1
POLE MARKING &
ROOFING ADDED.
D.K.M. MAR 93

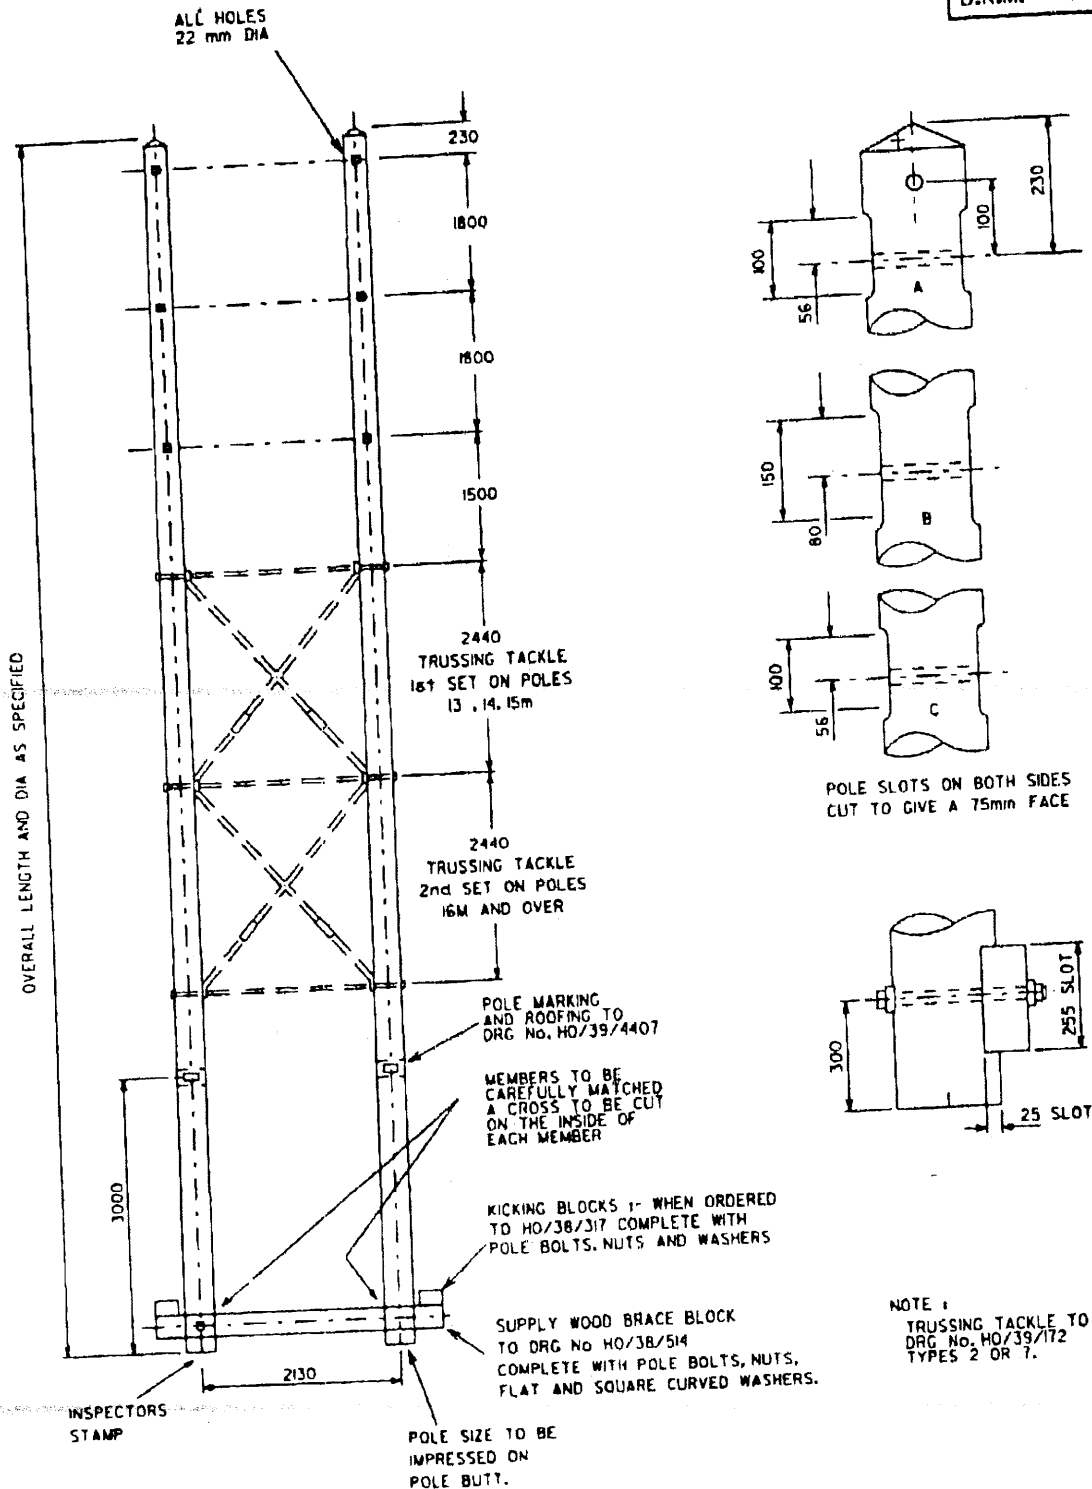

SCHEDULE:- P6004
33kv HEAVY CONSTRUCTION
SUPERSEDES DRG REF:- A6004-2

This drawing is protected by copyright and the information contained therein is confidential. The drawing may not be copied and the information contained therein may not be used, or disclosed to a third party wholly or in part except with the written permission of, and in the manner prescribed by SOUTHERN ELECTRIC plc © 1992



**SOUTHERN
ELECTRIC**

**POLE DRILLING, SCARFING AND MARKING
33kv DOUBLE CIRCUIT
SECTION 'H' POLE, 1800 SPACING**

Scale:- N.T.S.
Drm. by:- D.K.W.
Tcd. by:- D.K.M.
Ckd. by:- W.C.S.
App. by:- W.C.S.

Dimensions in millimetres

Drawing no.
HO37/6004 SHT 3 OF 3
C.A.D. Reference. HO6004.37

A4P

DATE PLOTTED 27-OCT-1993

