
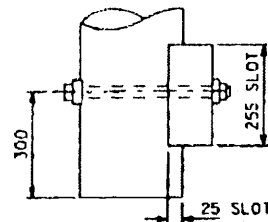
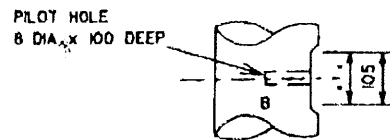
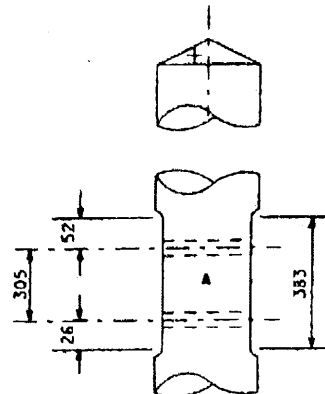


Original Issue
Date:- OCT 92
ISSUE 1
POLE MARKING &
ROOFING ADDED.
D.K.M. MAR 93

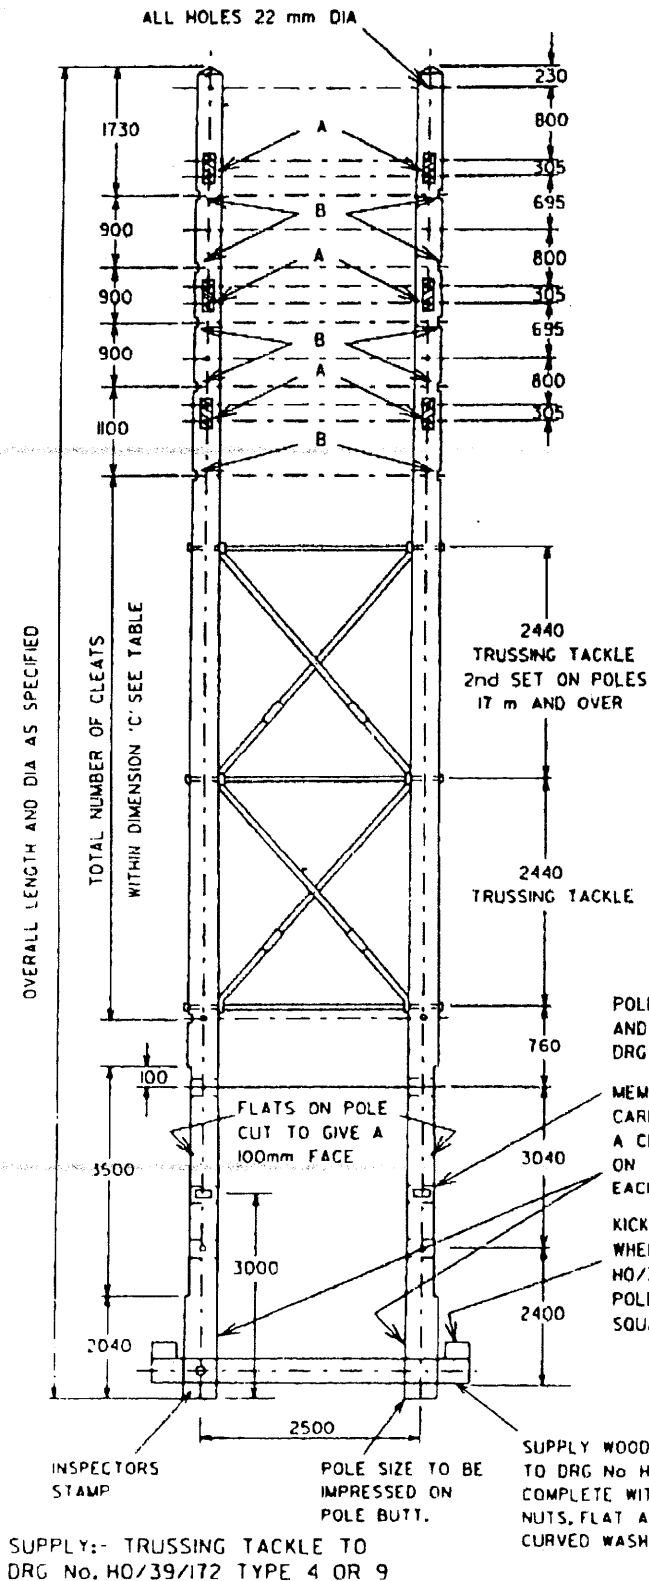

POLE MARKING
AND ROOFING TO
DRG No. HO/39/4407

MEMBERS TO BE
CAREFULLY MATCHED
A CROSS TO BE CUT
ON THE INSIDE OF
EACH MEMBER

KICKING BLOCKS:-
WHEN ORDERED TO DRG No.
HO/38/317 COMPLETE WITH
POLE BOLTS, NUTS, FLAT AND
SQUARE CURVED WASHERS

POLE LENGTH	DIM'N 'C'	TOTAL No OF CLEATS (EQUALLY SPACED)
14m	2470	2
15m	3470	3
16m	4470	4
17m	5470	5
18m	6470	6

SUPPLY WOOD BRACE BLOCK
TO DRG No HO/38/515
COMPLETE WITH POLE BOLTS,
NUTS, FLAT AND SQUARE
CURVED WASHERS

SCHEDULE- P6005
33kV HEAVY CONSTRUCTION
SUPERSEDES DRG REF:- A6005-2

**UNCONTROLLED COPY
SUBJECT TO REVISION
MASTER HELD AT HEAD OFFICE
Telephone 0628 584146**

Revision:-

This drawing is protected by copyright and the information contained therein is confidential. The drawing may not be copied and the information contained therein may not be used, or disclosed to a third party wholly or in part except with the written permission of, and in the manner prescribed by SOUTHERN ELECTRIC plc ©1993



**SOUTHERN
ELECTRIC**

**POLE DRILLING SCARFING AND MARKING
33kV DOUBLE CIRCUIT
'H' TERMINAL POLE (CABLE)**

Scale:- N.T.S.
Drm. by:- D.K.W.
Ycd. by:- D.K.M.
Ckd. by:- W.C.S.
App. by:- W.C.S.

Dimensions in millimetres

Drawing no.
HO/37/6005 SHT 5 OF 5
C.A.D. Reference. HO6005.37

