


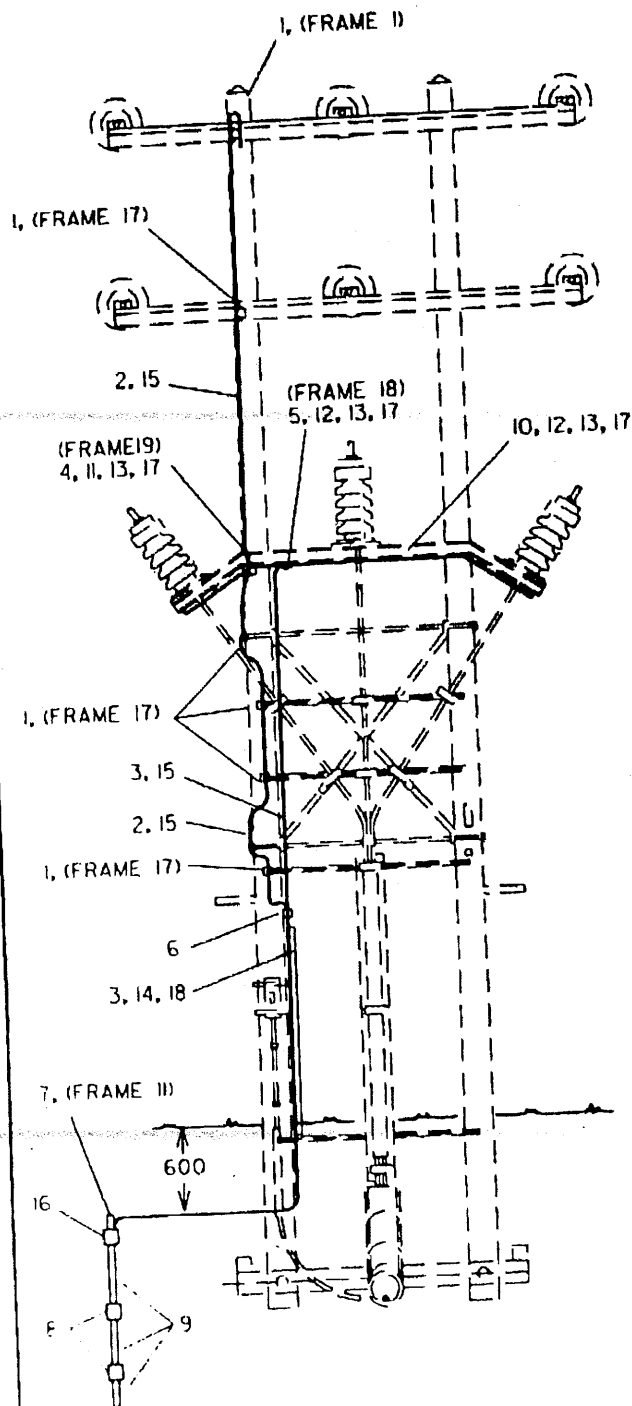

BONDING AND EARTHING CONNECTIONS
TO DRG No. HO/39/4206
AS SHOWN IN BRACKETS

SCHEDULE:- E2019
33kV HEAVY CONSTRUCTION
SUPERSEDES DRG REF:- A2019-1

GROUND
LEVEL

**UNCONTROLLED COPY
SUBJECT TO REVISION
MASTER HELD AT HEAD OFFICE
Telephone 0628 584146**

Revision:-

This drawing is protected by copyright and the information contained therein is confidential. The drawing may not be copied and the information contained therein may not be used, or disclosed to a third party wholly or in part except with the written permission of, and in the manner prescribed by SOUTHERN ELECTRIC plc ©1993



**SOUTHERN
ELECTRIC**

**33kV 'H' TERMINAL POLE (300mm² CABLE)
EARTHING DETAILS**

Scale:- N.T.S.
Des. by:- D.K.W.
Tel. by:- D.K.M.
Ckd. by:- W.C.S.
App. by:- W.C.S.

Dimensions in millimetres

Drawing no.
HO/37/2019 SHT 2 OF 5
C.A.D. Reference. HO2019.37

DATE PLOTTED 27-OCT-1993

