


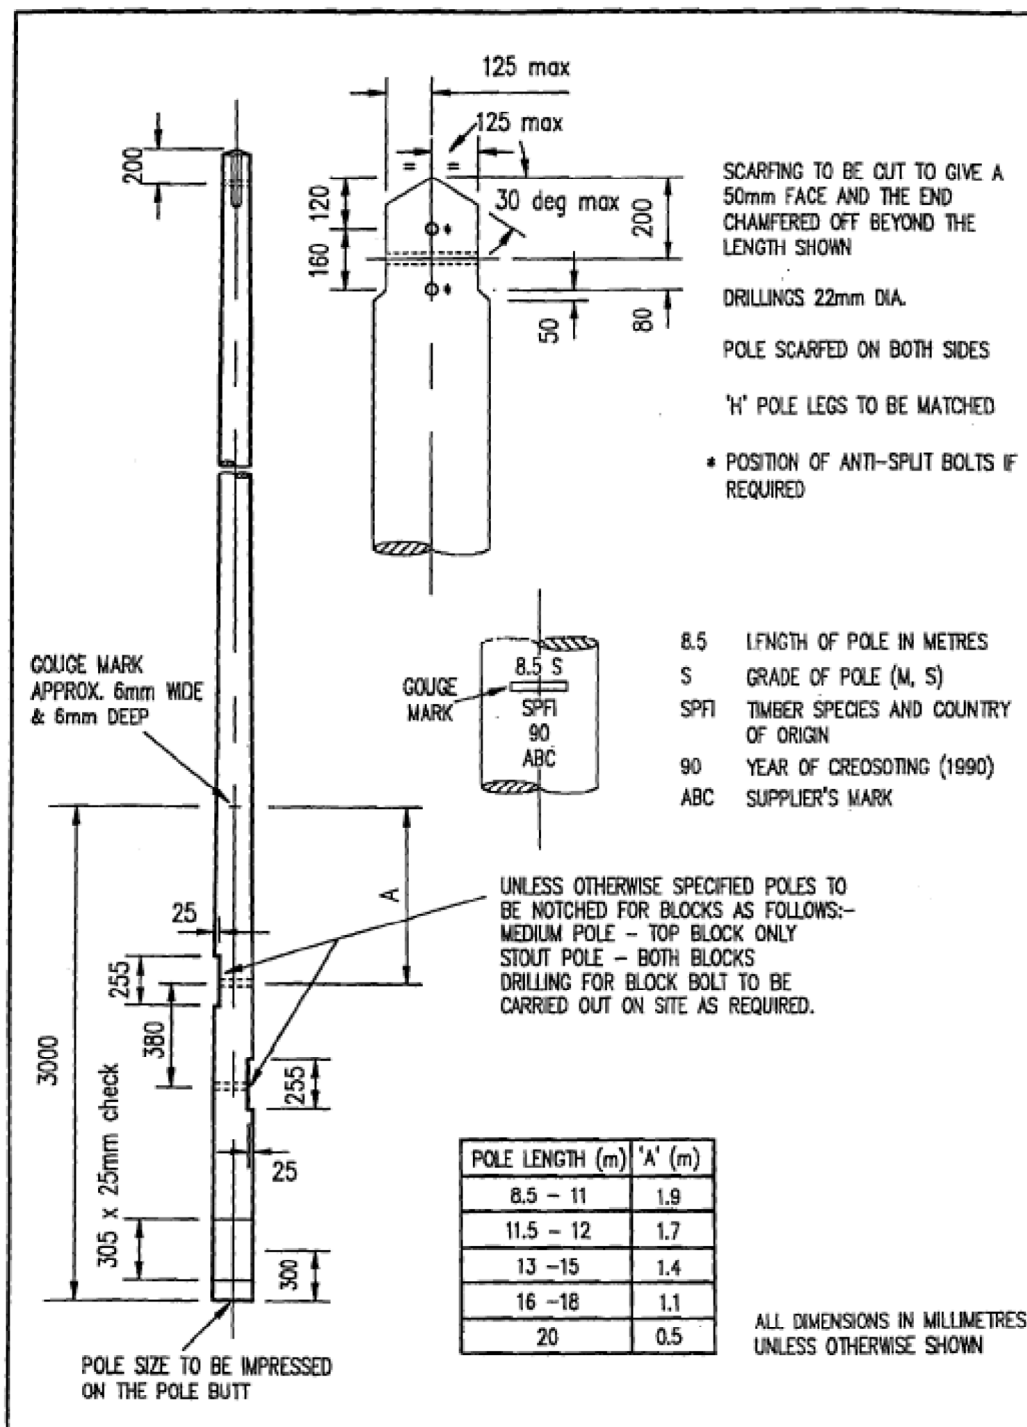

Date	12.09.91	Title			
Drawn	W.J.B.	'H' POLE MEMBER DRILLING, SCARFING & MARKING			
Checked					
Approved		Project	11 & 33KV WOOD POLE OVERHEAD LINE SPECIFICATION	Drawing Number	501/1109/0206
Scale		ShL No.		Rev.	2

HE

PERTH