


38.043

ISSUED
3 JUL 1996
1/0 23

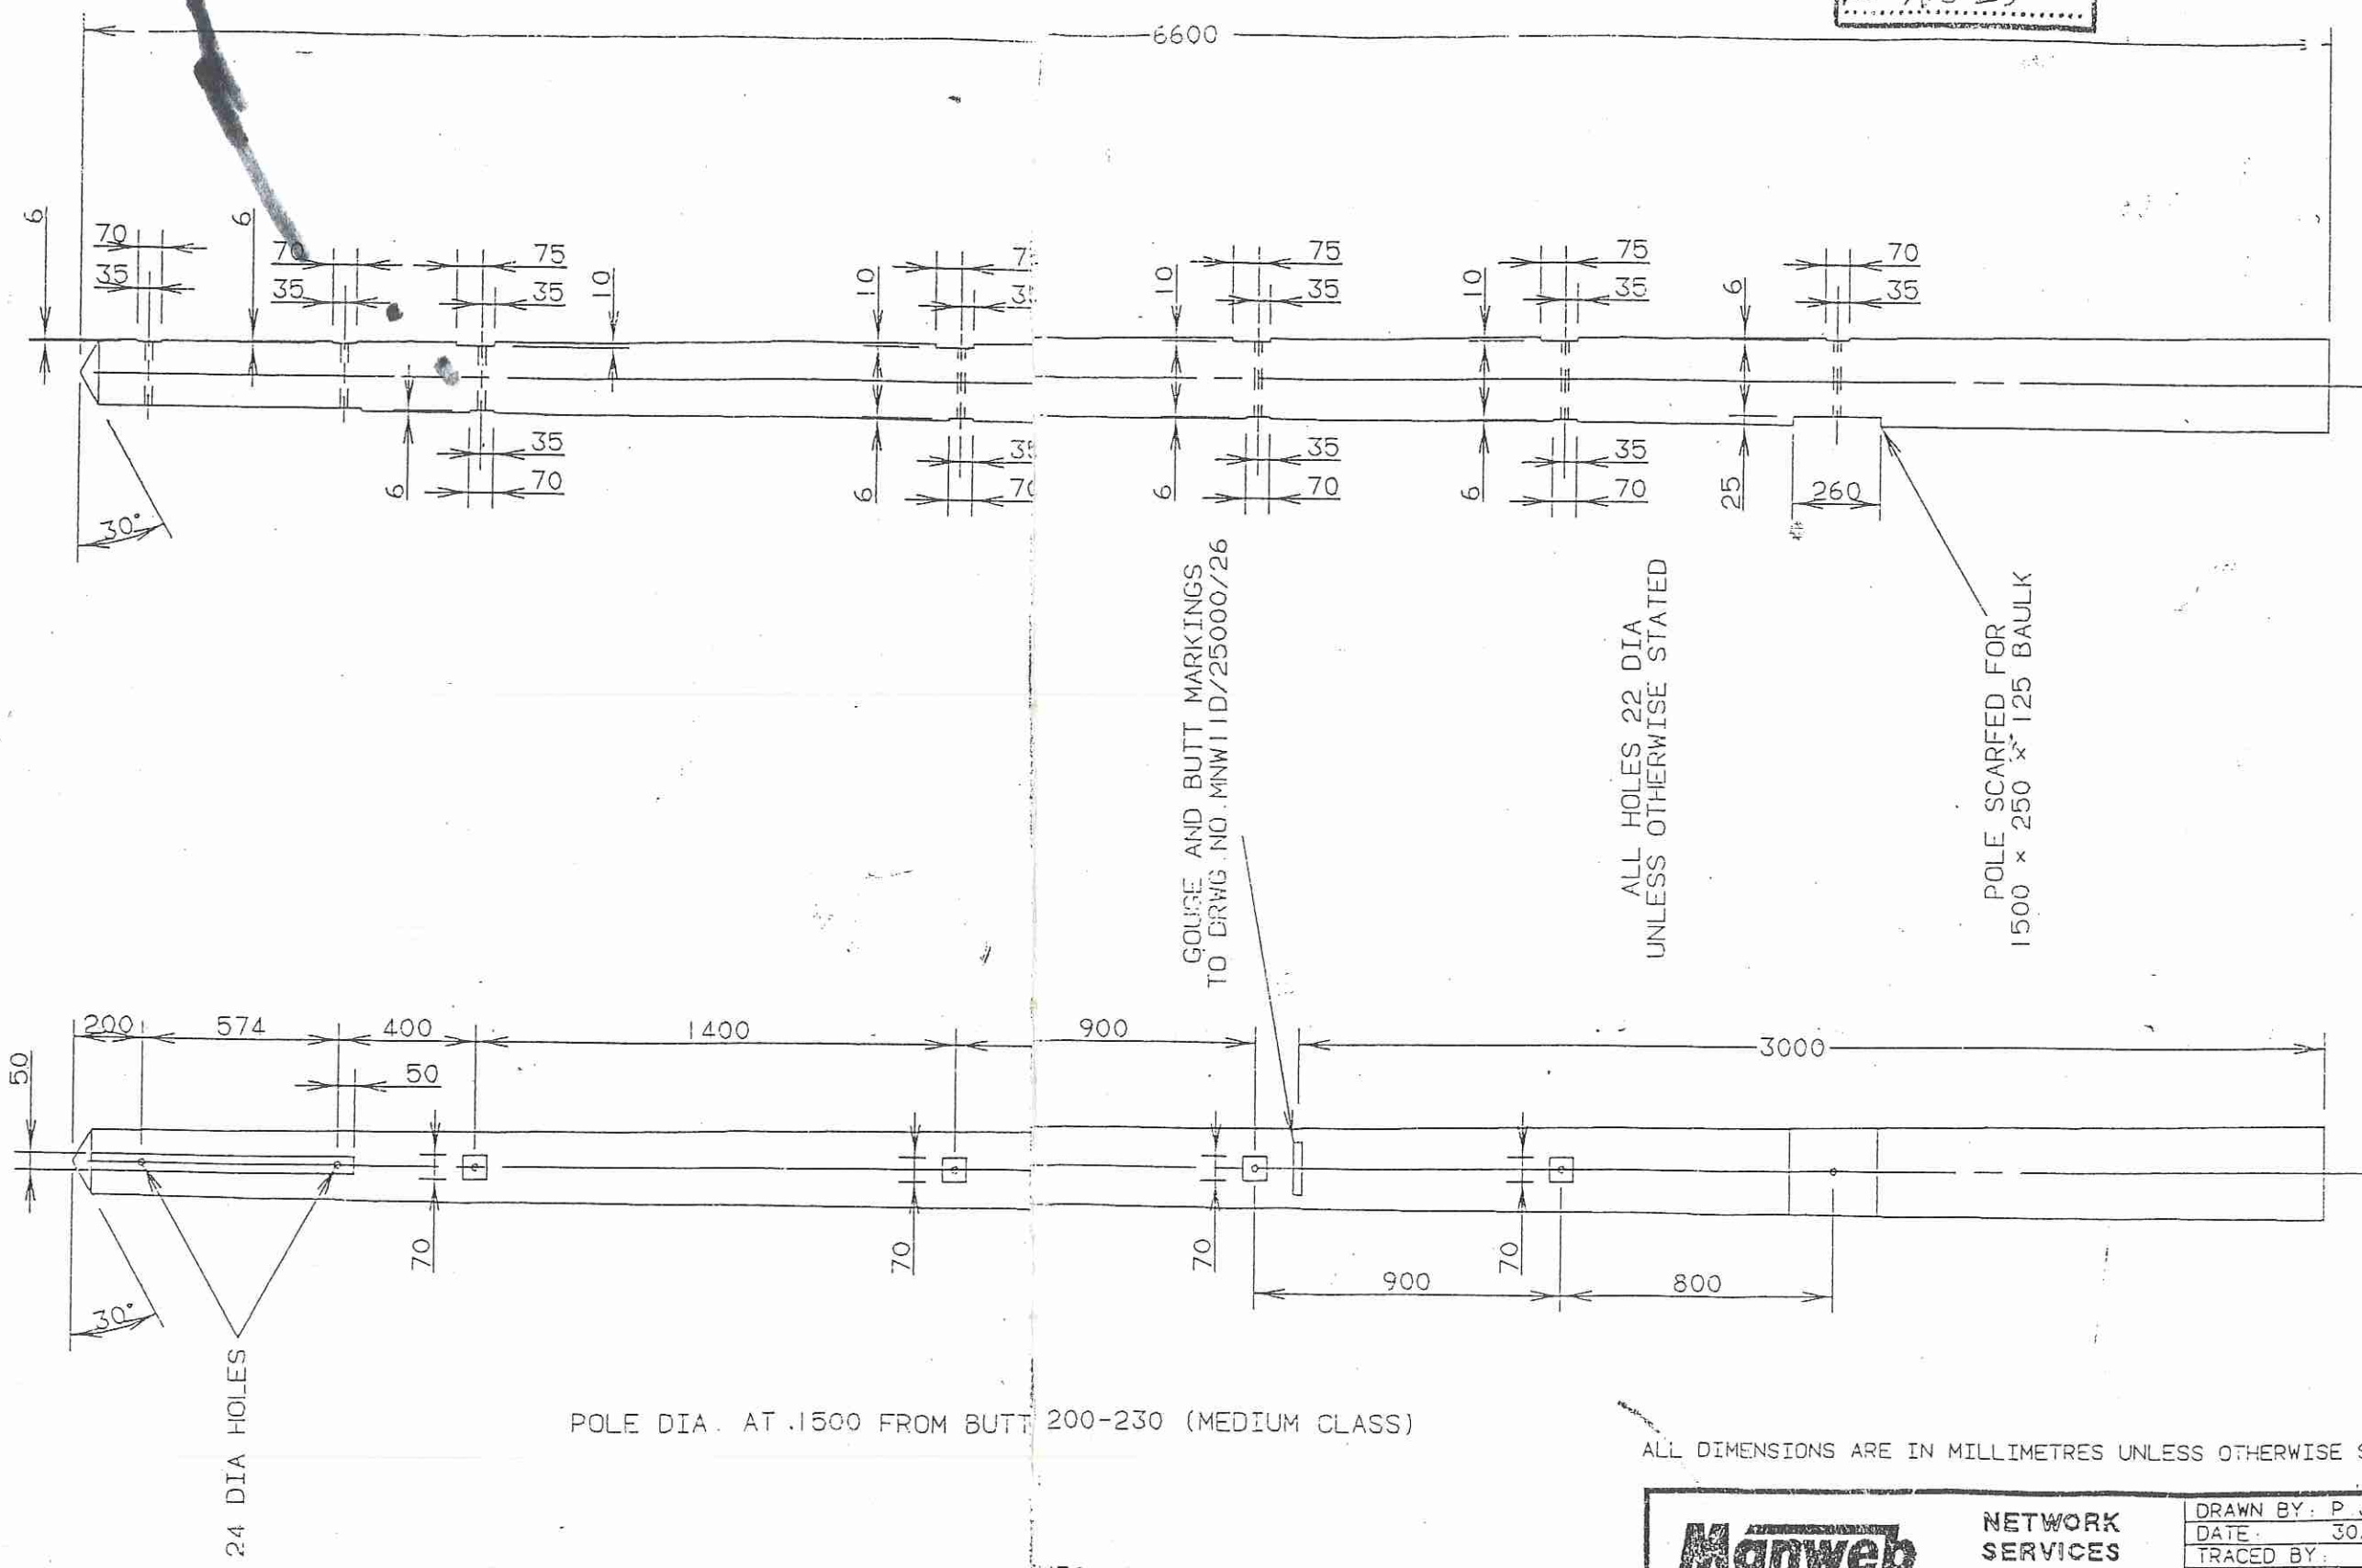

POLE DIA. AT 1500 FROM BUTT 200-230 (MEDIUM CLASS)

ALL DIMENSIONS ARE IN MILLIMETRES UNLESS OTHERWISE STATED

THIS DRAWING SUPERSEDES MNW 51690

Manweb NETWORK SERVICES DIVISION
DRAWN BY: P. J. H.
DATE: 30/09/94
TRACED BY:
JOB No:
APP'D BY: P. DUMAYNE

OVERHEAD LINE STANDARD
FABRICATION DETAILS OF
33kV SINGLE POLE WITH U/G CABLE TERMINATION
MNW 11D 12001 - 082 A3 SCALE 1:20

A
POLE LENGTH
WAS 6574
R.J.C. 2-5-95