


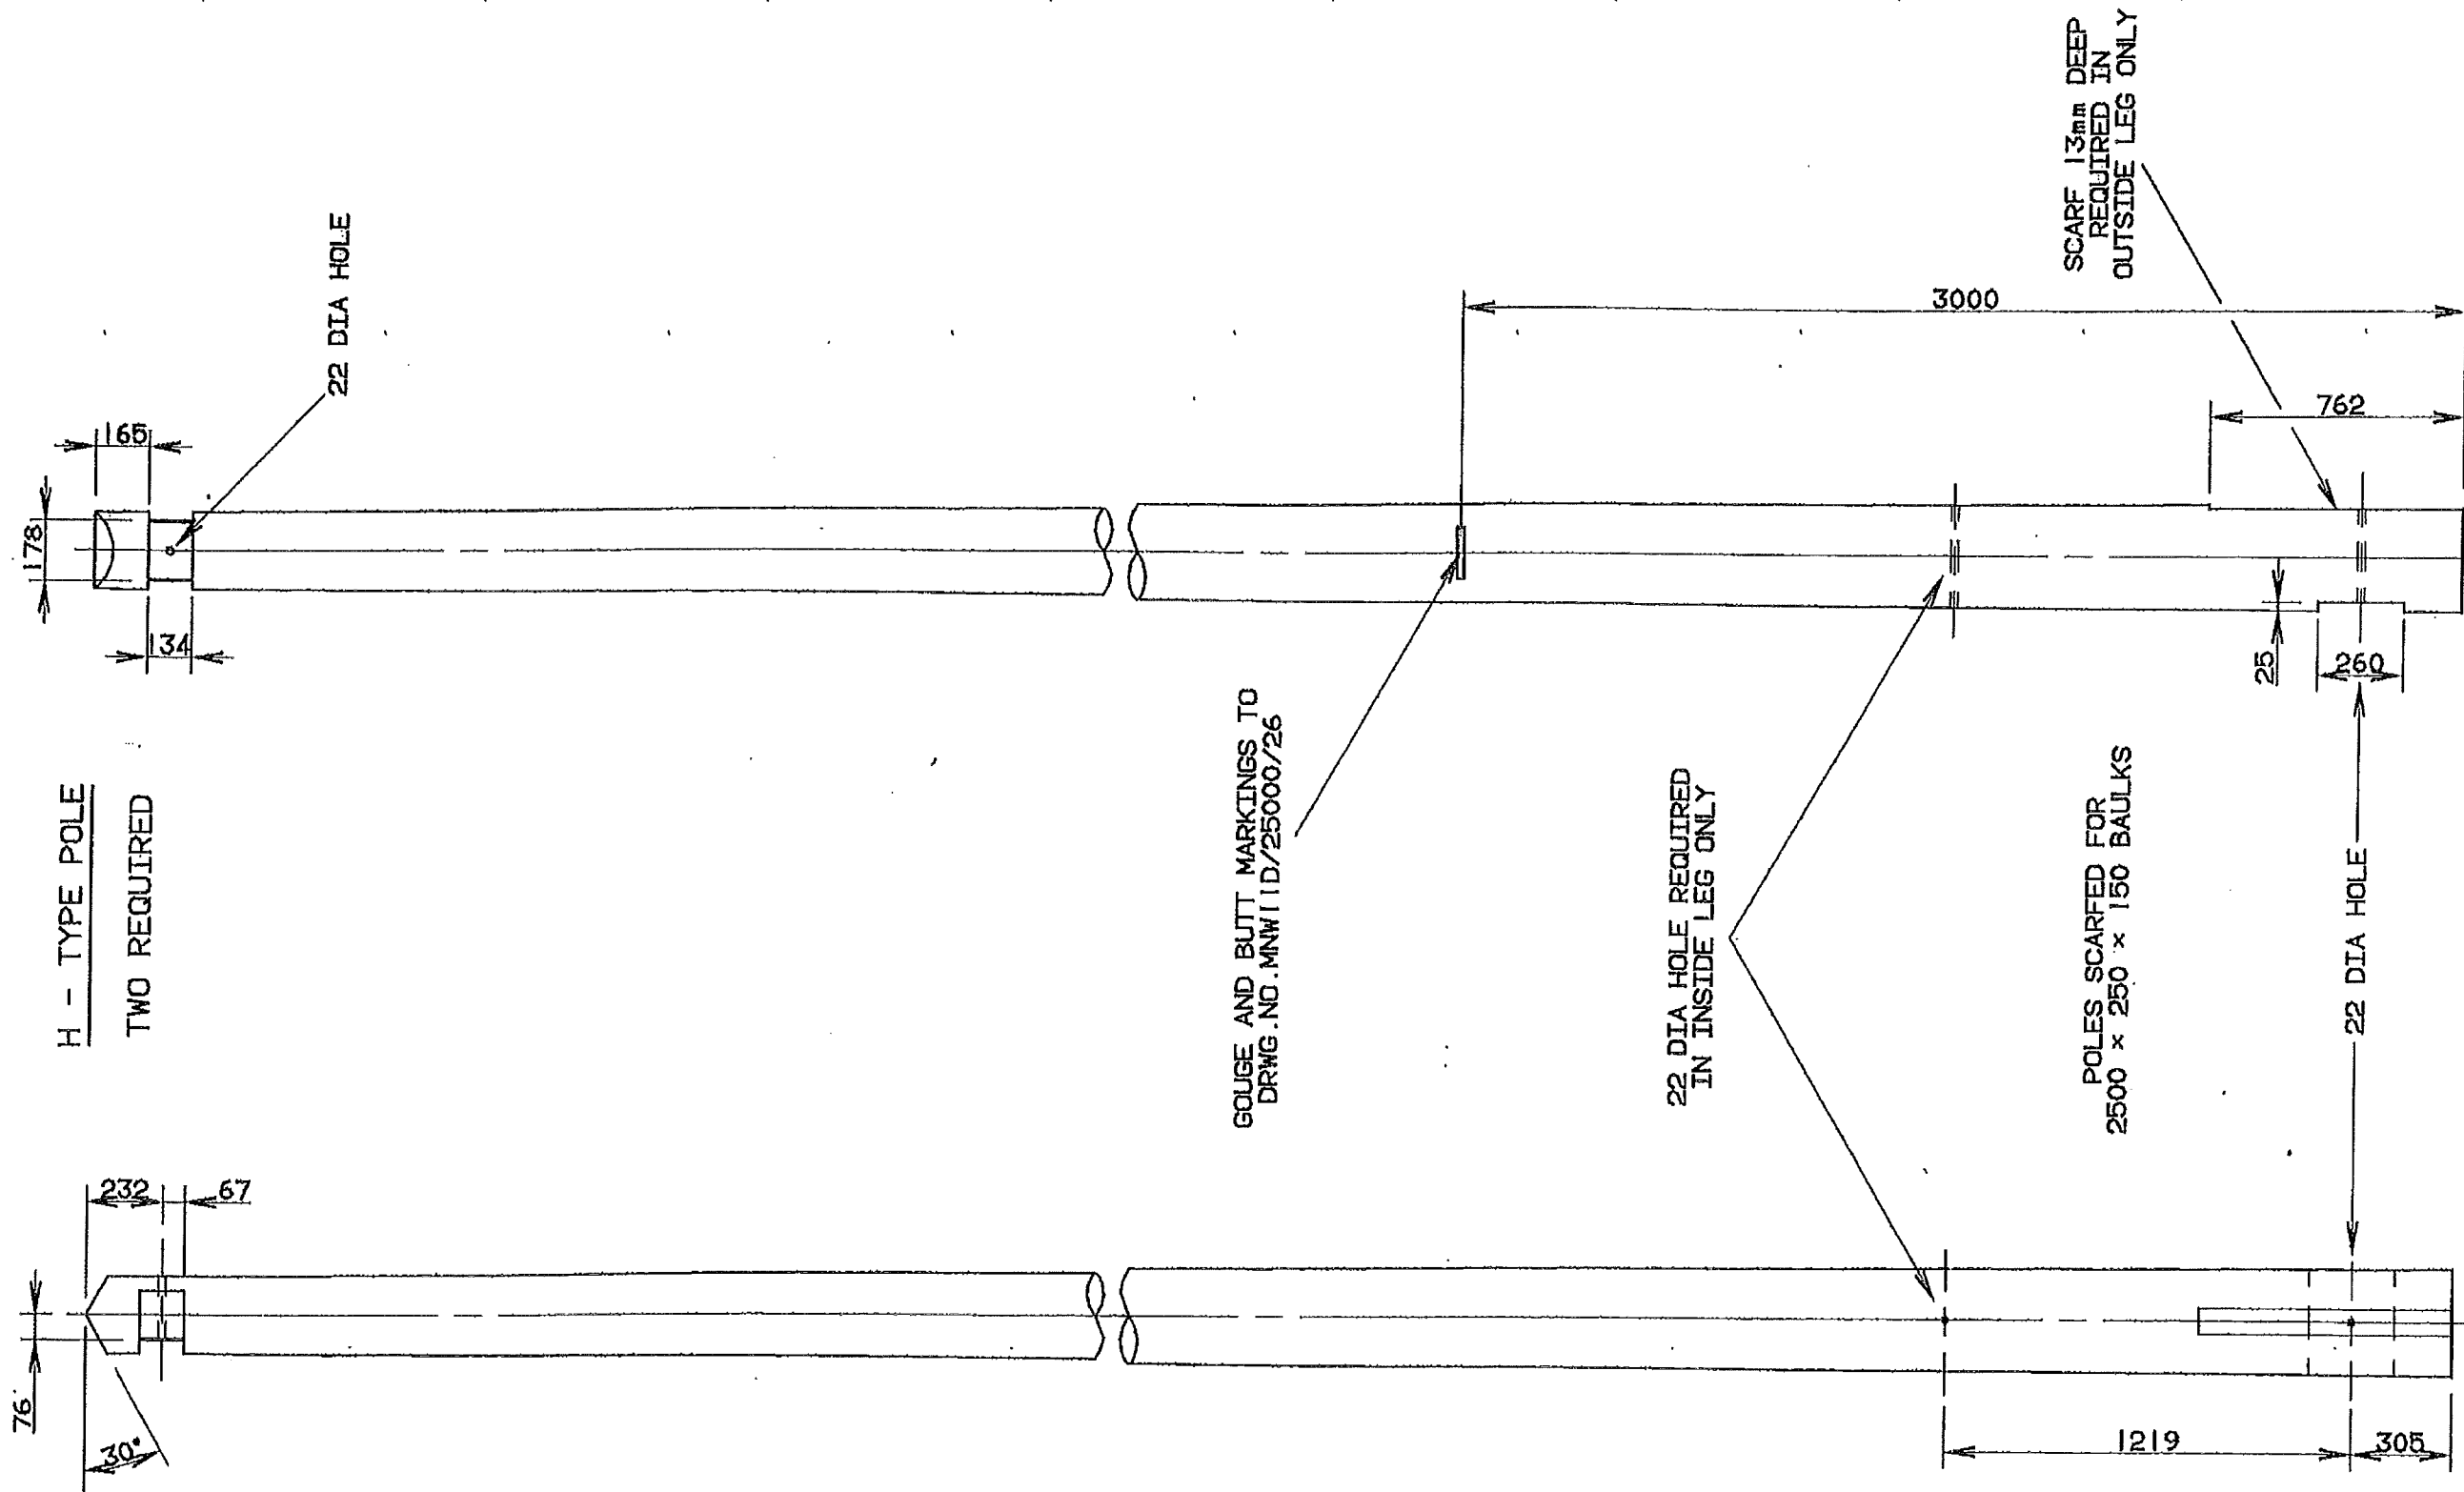

H - TYPE POLE
TWO REQUIRED

THIS DRAWING SUPERSEDES MNW0/2821/W

ALL DIMENSIONS ARE IN MILLIMETRES UNLESS OTHERWISE STATED

Manweb

NETWORK
SERVICES
DIVISION

DRAWN BY: P.J.H.
DATE: 30/09/94
TRACED BY:
JOB No:
APP'D BY: P.DUMAYNE

OVERHEAD LINE STANDARD
FABRICATION DETAILS OF
33kV H - TYPE SECTION POLE

MNW 11D 12001 - 083 A3

SCALE: 1:20