


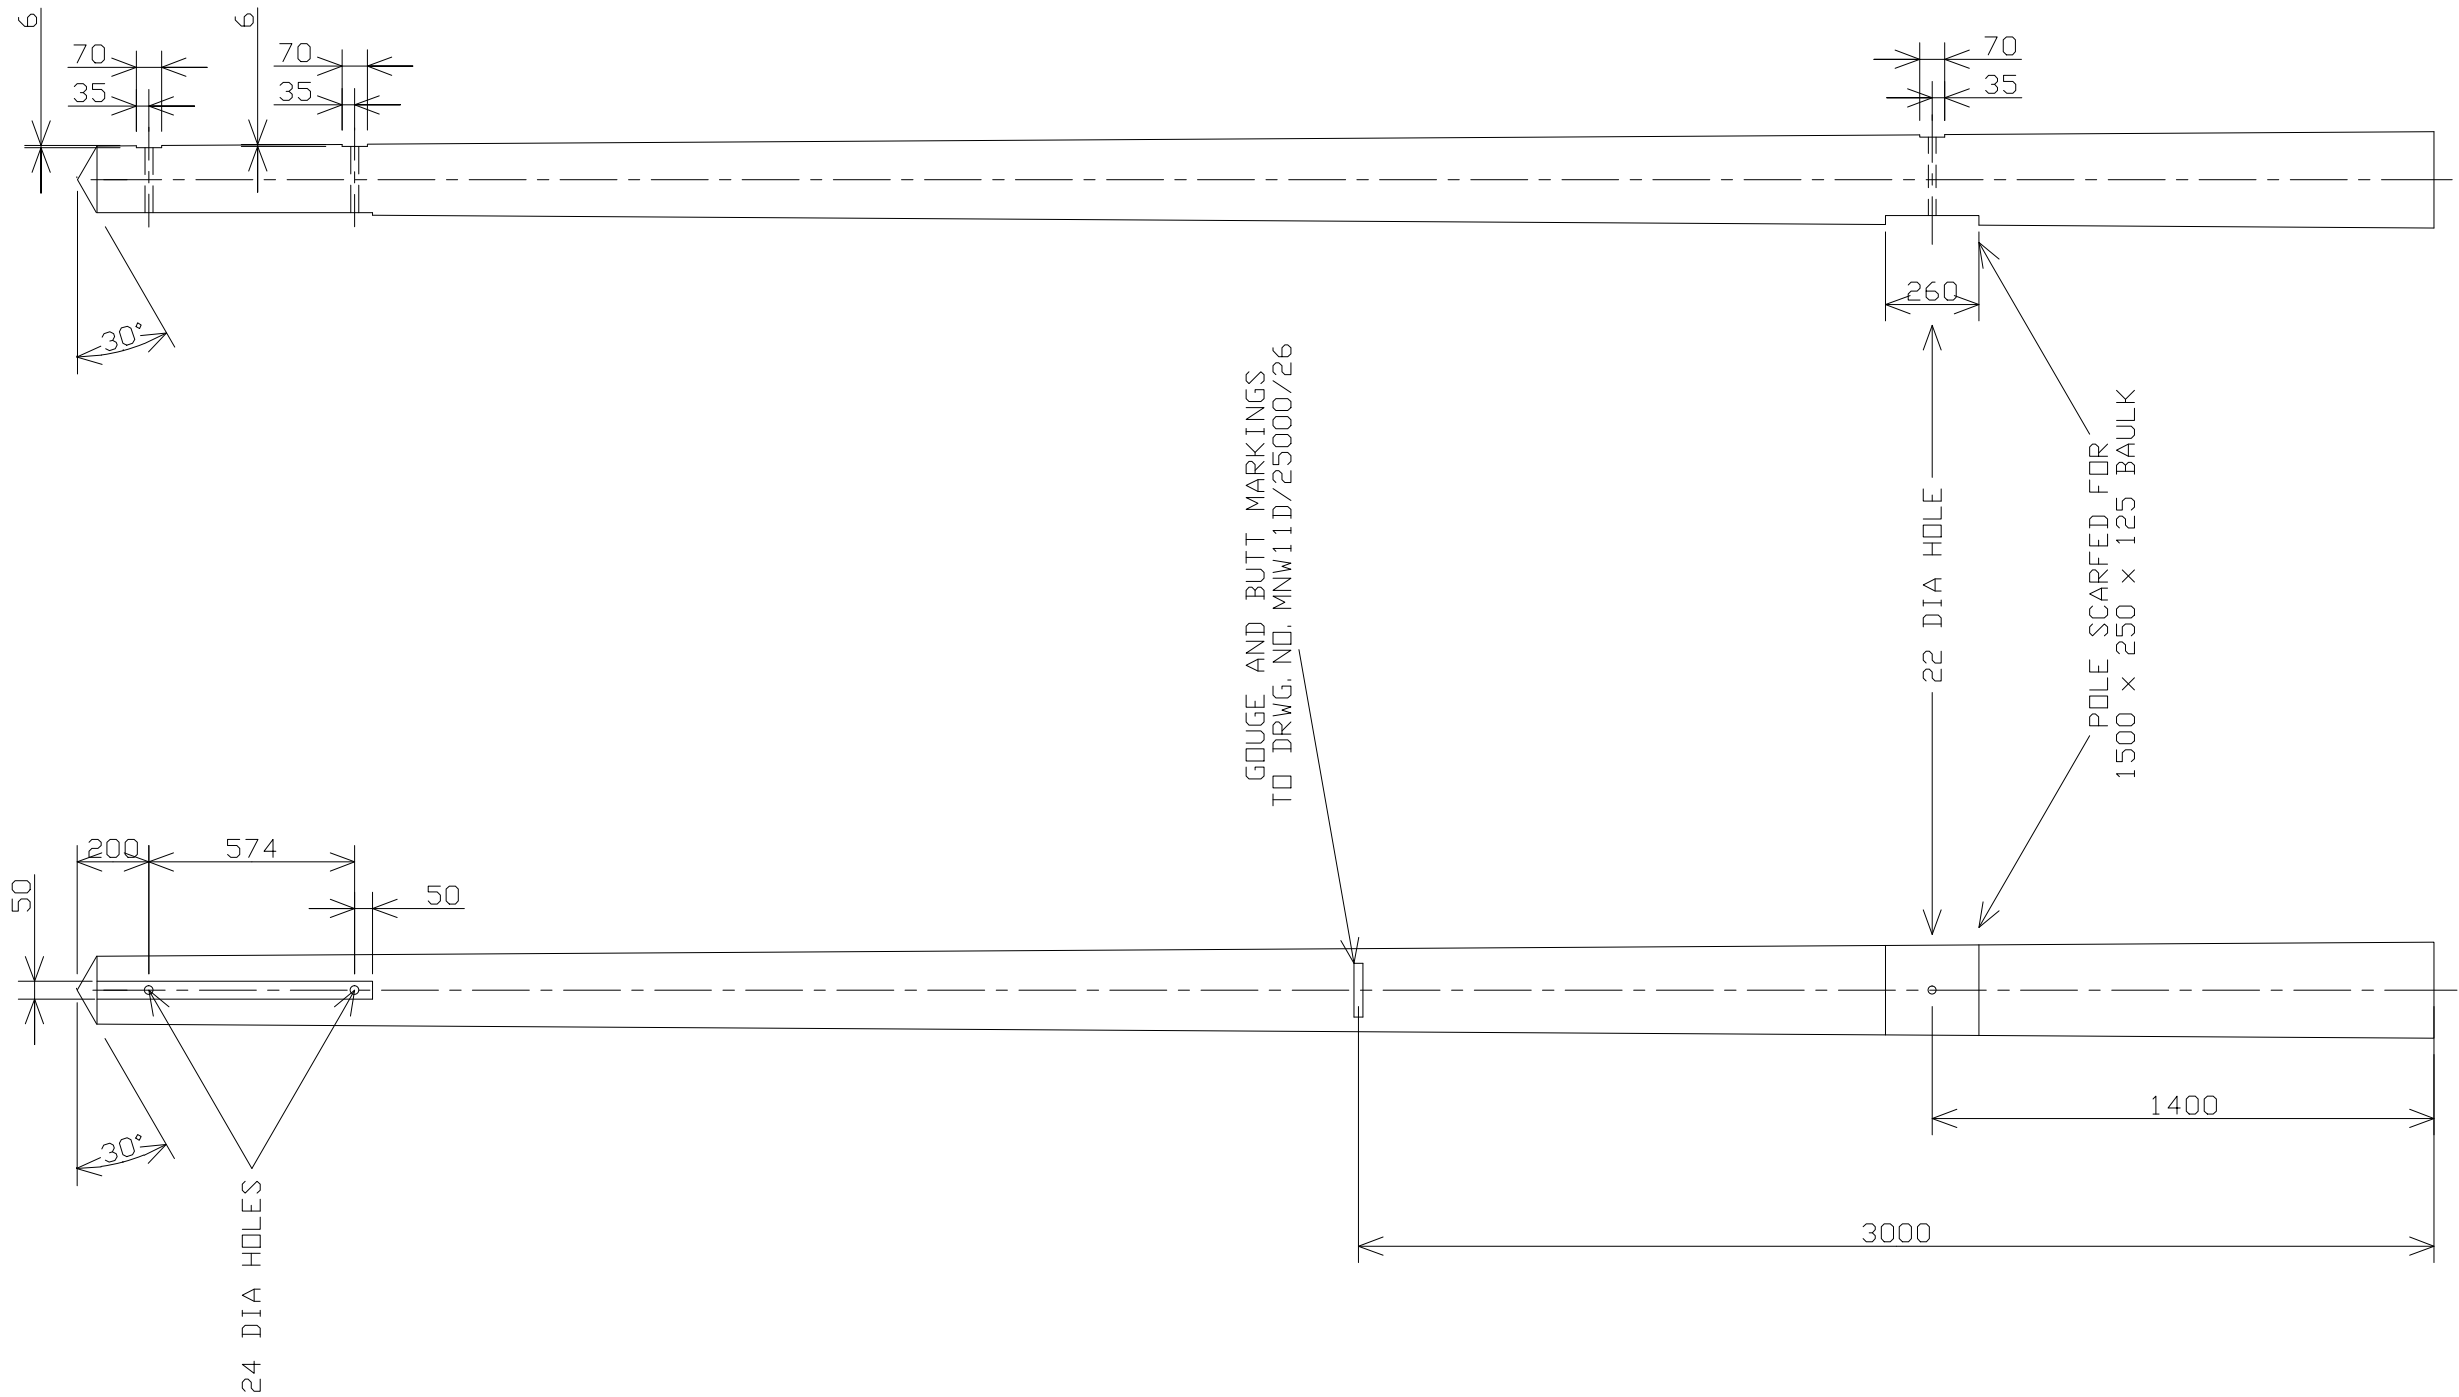

ALL DIMENSIONS ARE IN MILLIMETRES UNLESS OTHERWISE STATED

FOR INSTALLATION DETAIL SEE GENERAL ARRANGEMENT DRWG. NO. MNW11D12001-056

Manweb

**NETWORK
SERVICES
DIVISION**

DRAWN BY: R. J. COLES
DATE: 30/09/94
TRACED BY:
JOB No:
APP' D BY: P. DUMAYNE

OVERHEAD LINE STANDARD
FABRICATION DETAILS OF
33kV LEAD IN POLE, O/H SUBSTATION ENTRY

MNW 11D 12001 - 084 A3

SCALE: 1: 20