


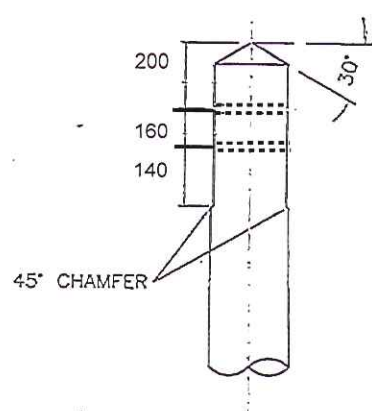

# H - TYPE POLE

TWO REQUIRED  
L.H. POLE SHOWN

SCARFING TO BE CUT TO GIVE  
A 50mm FACE ON BOTH FACES  
OF POLE AND THE END  
CHAMFERED OFF BEYOND  
THE LENGTH SHOWN

POLE SCARFED ON BOTH SIDES  
DRILLINGS 22mm DIA

DIMENSIONS SHOWN ARE FOR 12 METRE POLE

FOR 13 METRE POLE 1 X EXTRA DRILLING REQUIRED 1000mm ABOVE POINT 'A'

FOR 14 METRE POLE 2 X EXTRA DRILLINGS REQUIRED 1000mm & 2000mm ABOVE  
POINT 'A'

FOR 15 METRE POLE 3 X EXTRA DRILLINGS REQUIRED 1000mm, 1900mm & 2800mm  
ABOVE POINT 'A' - DIMENSION 'B' TO BE INCREASED TO 2600mm TO ALLOW FOR  
INCREASED PLANTING DEPTH



FOR 16 METRE POLE 4 X EXTRA DRILLINGS REQUIRED 1000mm, 2000mm, 2900mm  
& 3800mm ABOVE POINT 'A' - DIMENSION 'B' TO BE INCREASED TO 2600mm TO  
ALLOW FOR INCREASED PLANTING DEPTH

FOR 17 METRE POLE 5 X EXTRA DRILLINGS REQUIRED 1000mm, 2000mm, 3000mm,  
4900mm & 5800mm ABOVE POINT 'A' - DIMENSION 'B' TO BE INCREASED TO  
2600mm TO ALLOW FOR INCREASED PLANTING DEPTH

FOR POLE SIZES ABOVE 17 METRE SPEN WILL ADVISE

12-14 METRE POLE PLANTING DEPTH 2.2 M

15-17 METRE POLE PLANTING DEPTH 2.4 M

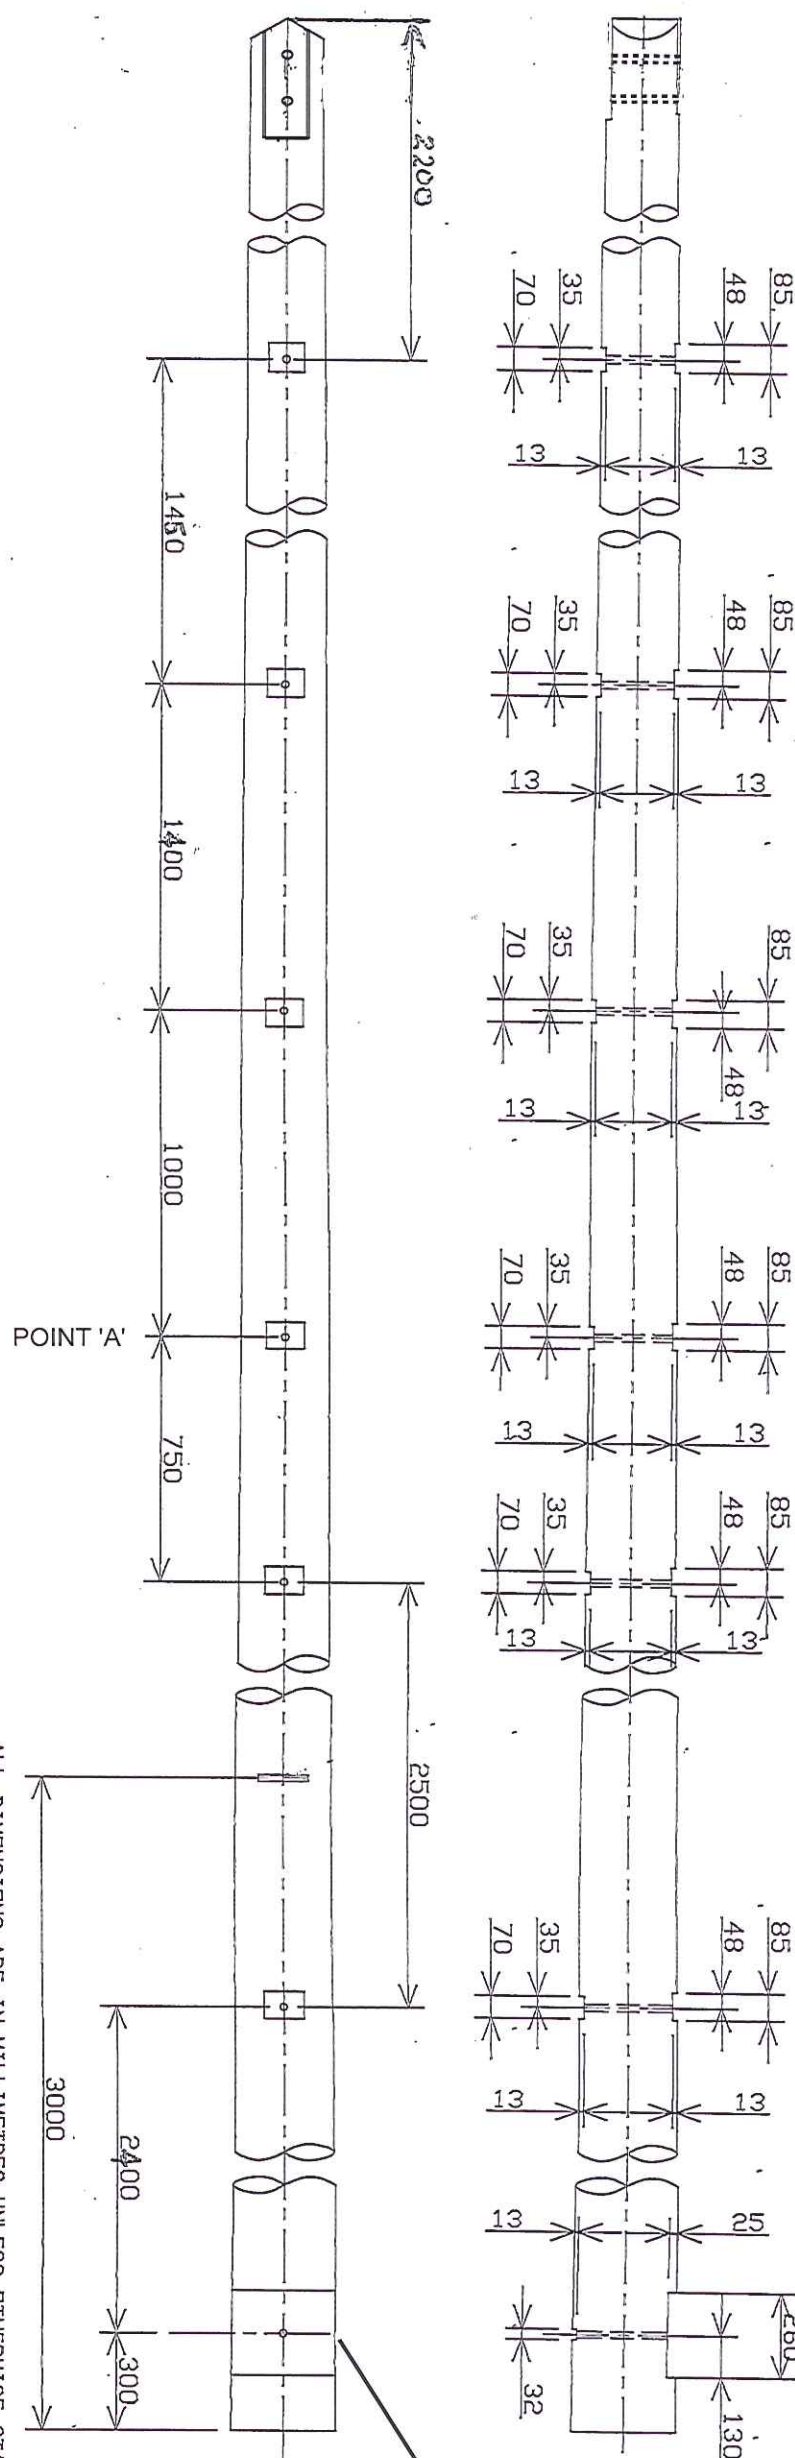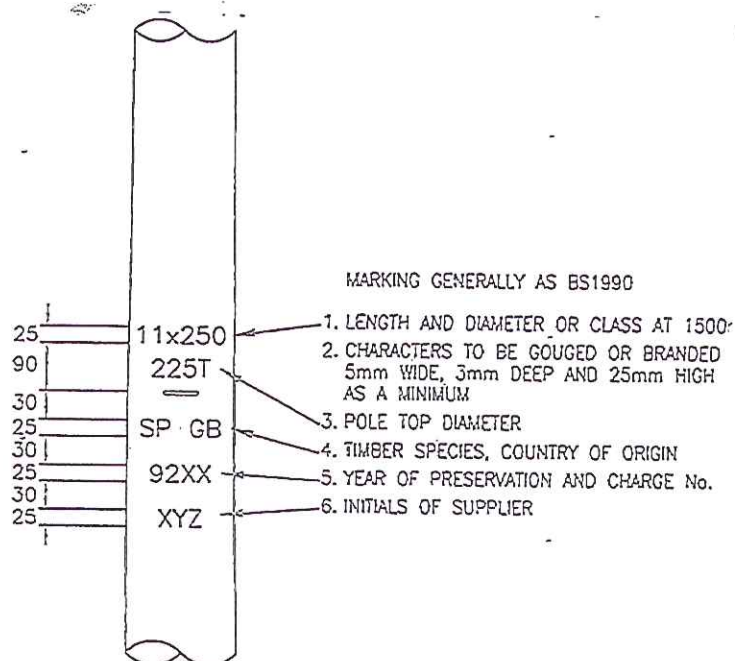

ALL DIMENSIONS ARE IN MILLIMETRES UNLESS OTHERWISE STATED

POLES SCARFED FOR 2500 X 250 X 125 BAULK

ALL HOLES 22 DIA UNLESS OTHERWISE STATED



DRG No. MNW/L34/13/001

**33kV MATCHED 'H' POLE FOR L33/4 CONSTRUCTION 200mm  
POPLAR AAAC CONDUCTOR  
(NON SEVERE WEATHER AREA)**