




ScottishPower
Energy Networks

Uncontrolled Copy

Specification for 11kV And 33kV Overhead
Lines of Unearthed Construction on Single and
“H” Type Wood Poles.

OHL-03-099
Issue 1

Figure 19 Single Pole Double Terminal (Drawing SP4000578)

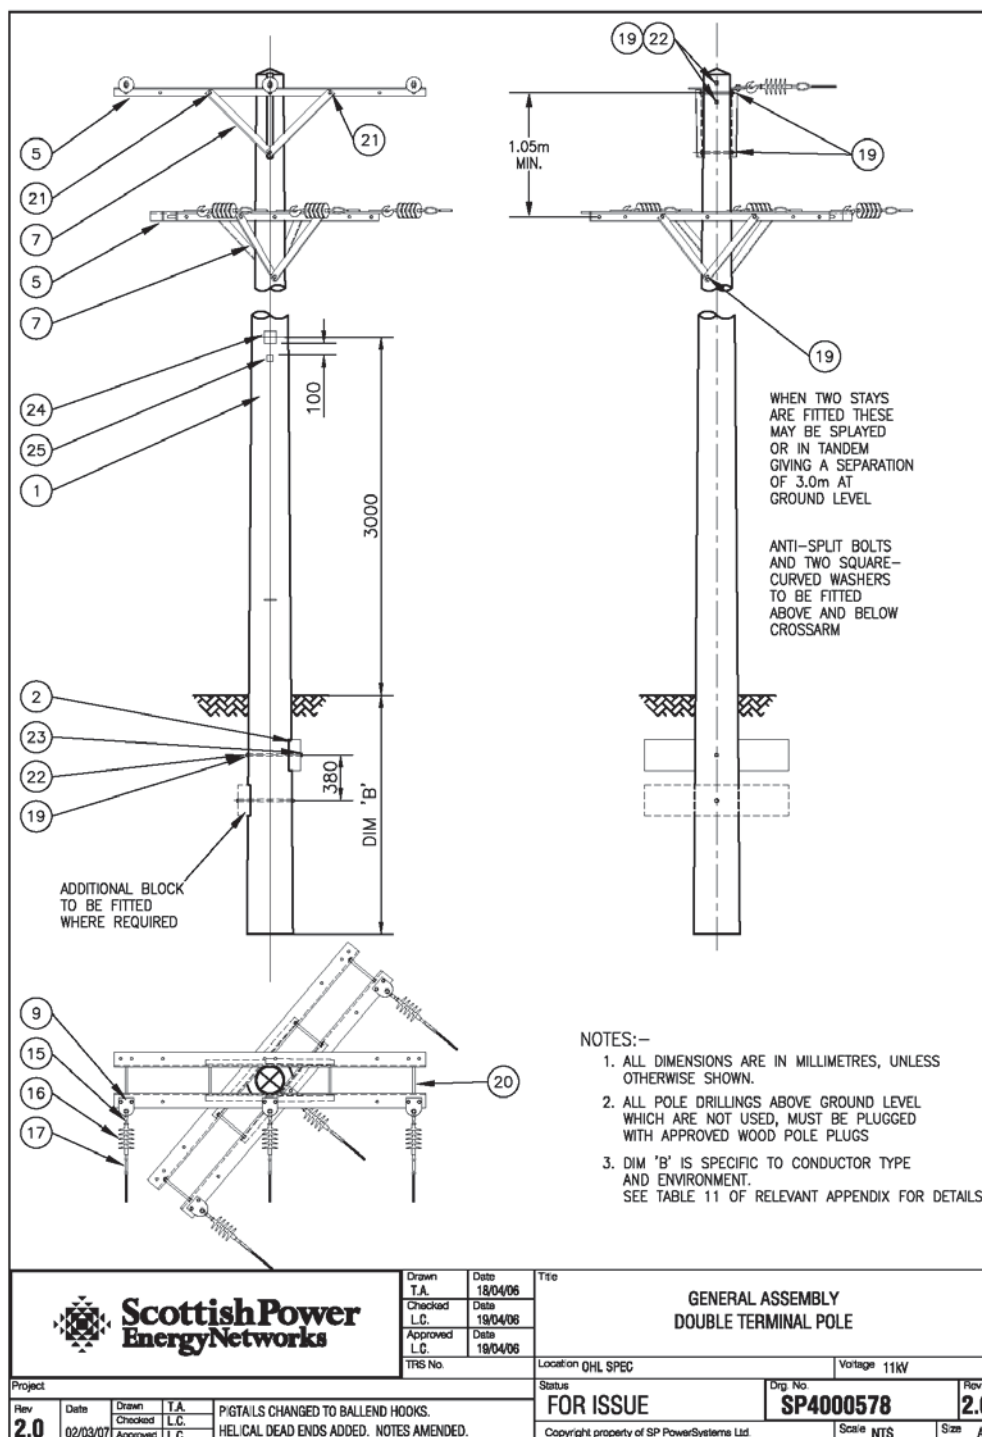



Specification for 11kV And 33kV Overhead Lines of Unearthed Construction on Single
and “H” Type Wood Poles.

OHL-03-099
Issue 1

ScottishPower
EnergyNetworks

General Assembly Single Pole Double Terminal (Drawing SP4000578)

ITEM	NUMBER	DESCRIPTION	ENATS, BS or OTHER REFERENCE	DRAWING NUMBER	COMMODITY CODE NO.
01	1	Wood Pole	ENATS 434001	-	-
02	1 or 2	Pole Block	ENATS 439103 Type 2	SP4019020	C43810342
05	4	Terminal Crossarm Member	ENATS 439522	SP4018401	C43811080
07	8	Crossarm Strut	ENATS 439526	SP4017649	C43811070
09	6	Terminal Strap	ENATS 439528	SP4017664	C43811074
15	6	Ball End Hook	BS3288 Fig 12 Ref 15/32	-	C43238026
16	6	Tension Insulator	ENATS 43-93	-	C43200548
17	6	Helical Dead End Assembly	ENATS 43-92	-	-
19	5 or 6	M20 Pole Bolt (HYS) and Nut. Length to suit Pole diameter	ENATS 43- 96 Clause 4.2 (Grade 8.8 HYS)	-	-
20	8	M20 Tie Rods	ENATS 439608 Type 2 or 3	-	C43811060
21	20	M20 x 60mm Assembly Bolt and Nut	ENATS 43- 96 Clause 4.2	-	C43602072
22	1 or 2	M20 Square Curved Washer	ENATS 439605	-	C43602025
23	1 or 2	M20 Square Flat Washer	ENATS 439604	-	C43602050
24	1 or 2	Safety Sign English Bilingual	-	-	C06294004 C06293900
25	As Required	Pole Numbers	-	-	-
	As Required	Hardwood Plugs	ENATS 439516	-	-