


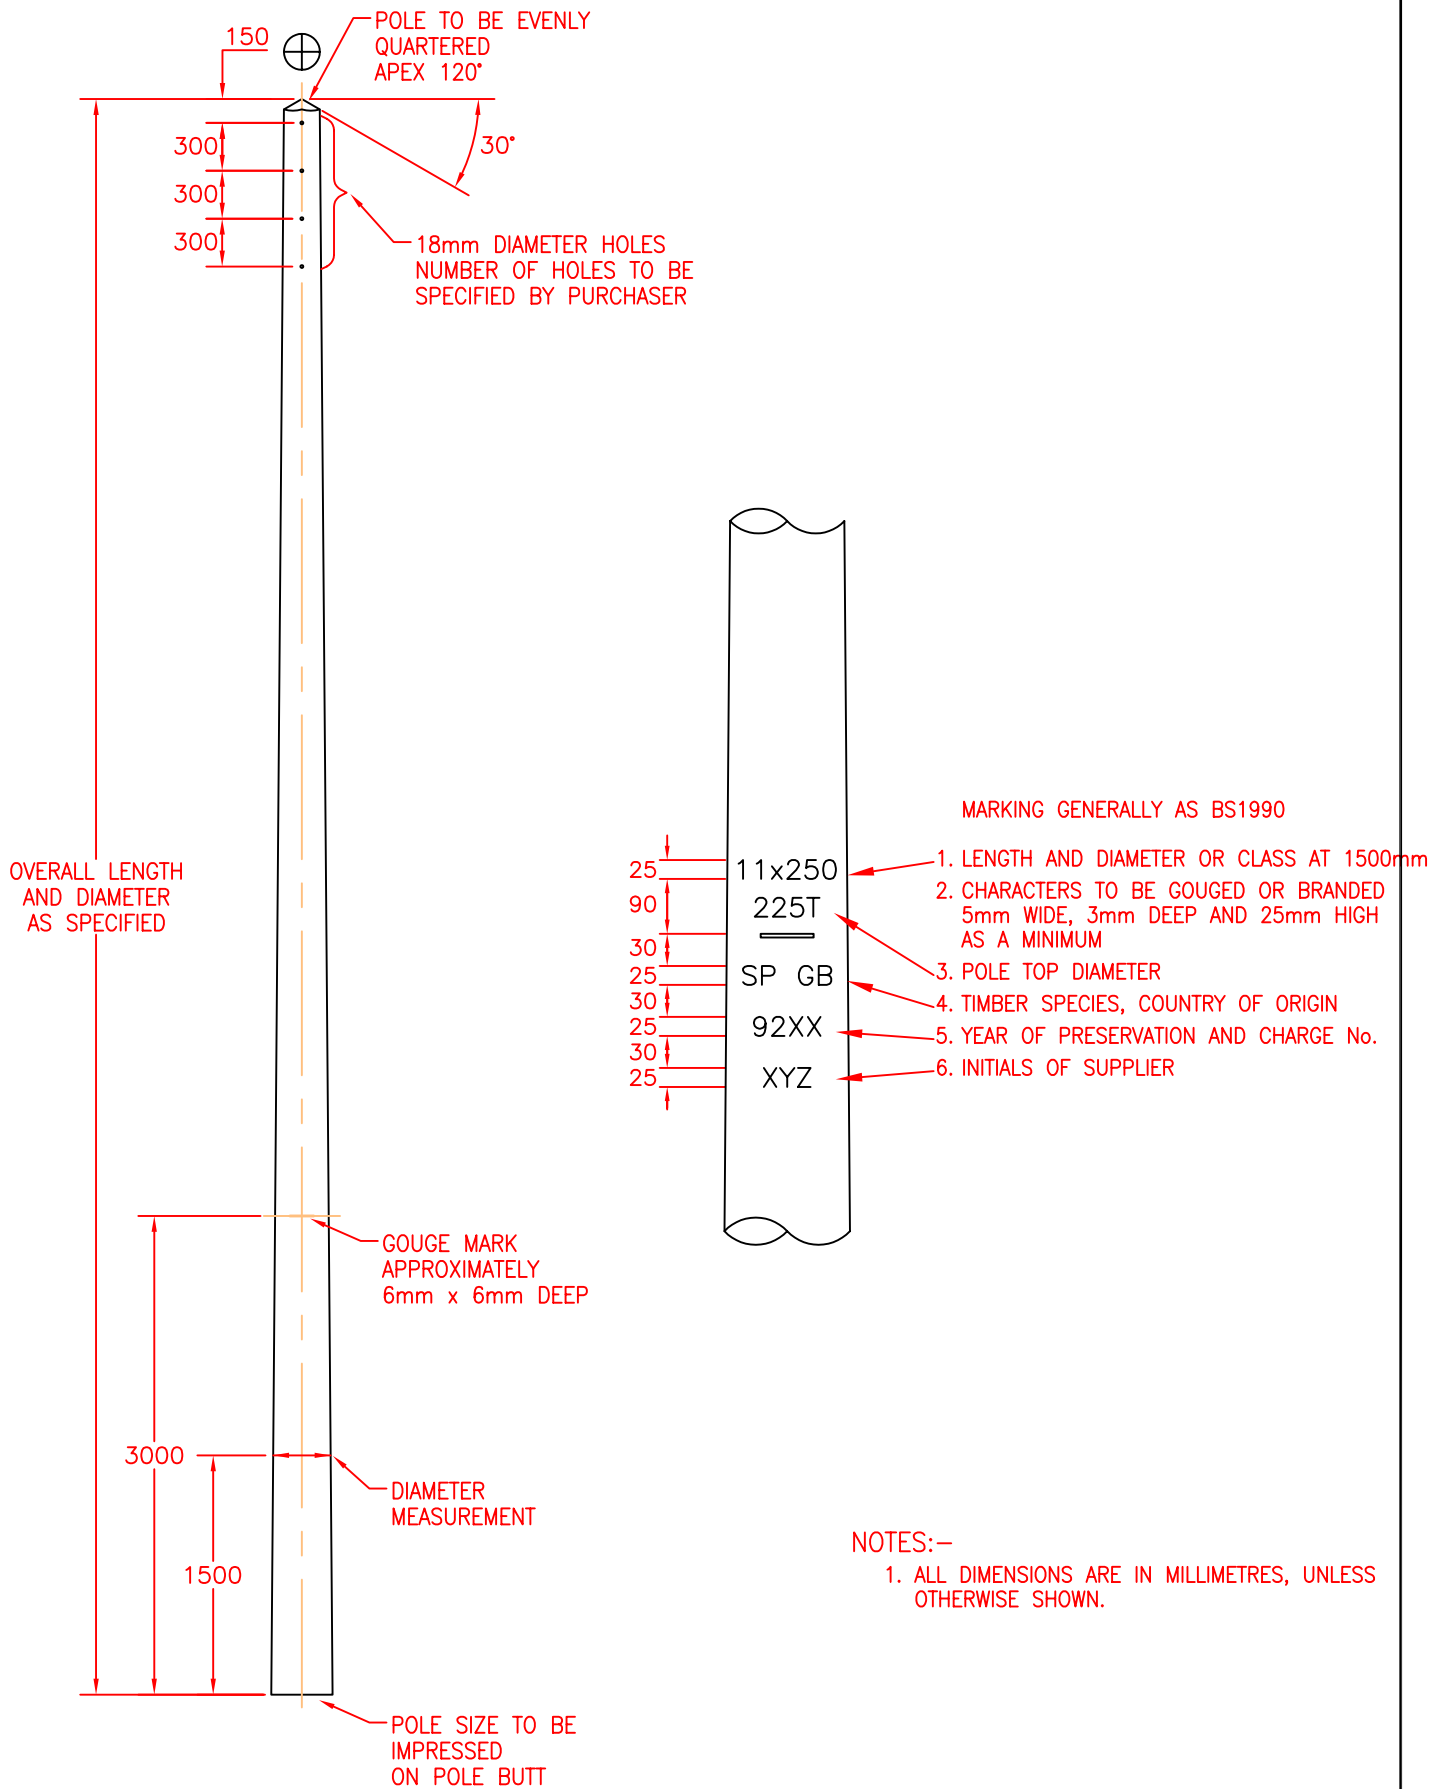

System Design, Drawing Office, 3 Prenton Way, Prenton, CH43 3ET
Telephone 0151 6092491

Drawn TA	Date 24/08/06
Checked DJB	Date 24/08/06
Approved DK	Date 24/08/06

Title

DRILLINGS AND MARKINGS OF WOOD POLES FOR L.V. BARE WIRE OVERHEAD LINES

Location SP STANDARDS

Status

FOR ISSUE

Drg. No.

SP4007757

Rev.

2.0

© Copyright property of SP PowerSystems Ltd.

Scale

Size A4