

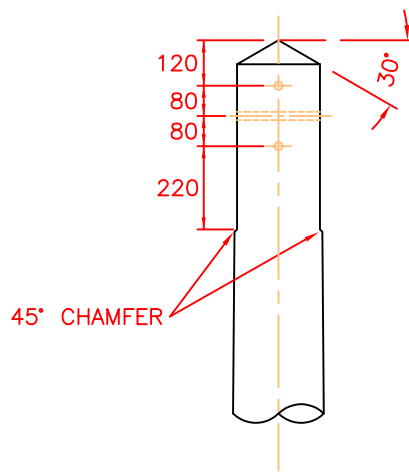


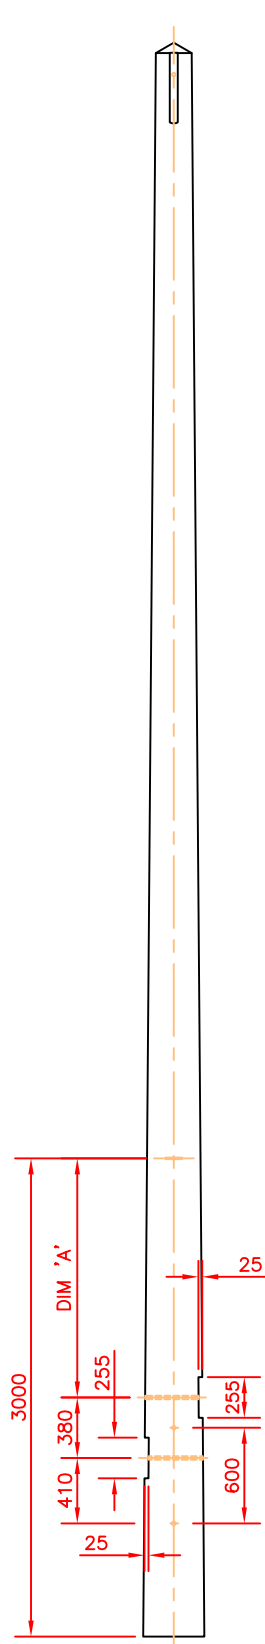

SCARFING TO BE CUT TO GIVE
A 50mm FACE ON BOTH FACES
OF POLE AND THE END
CHAMFERED OFF BEYOND
THE LENGTH SHOWN

POLE SCARFED ON BOTH SIDES
DRILLINGS 22mm DIA

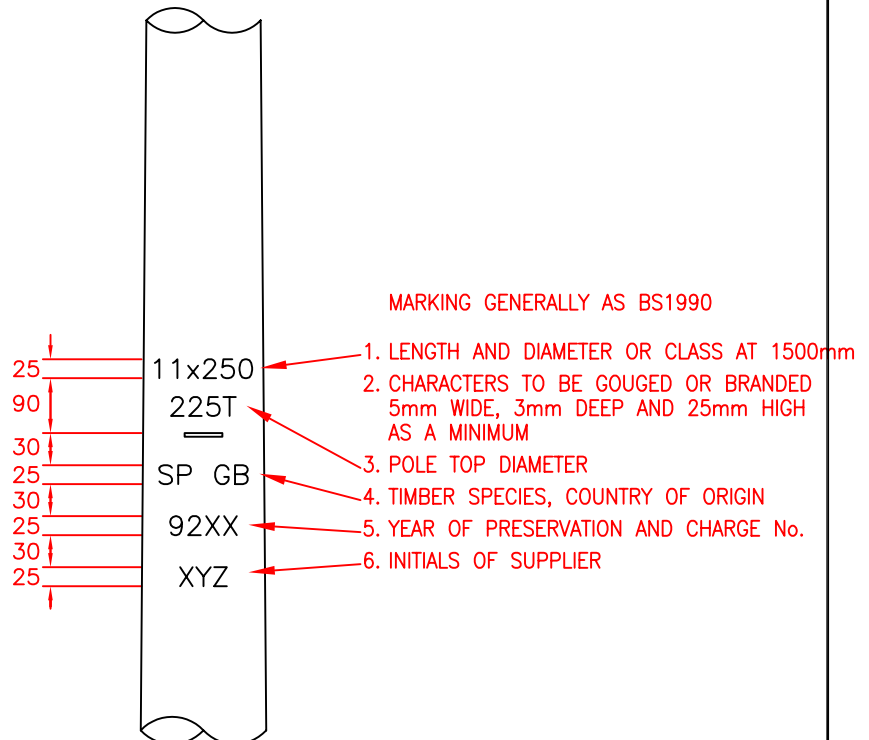

MARKING GENERALLY AS BS1990

NOTES:-

- ALL DIMENSIONS ARE IN MILLIMETRES, UNLESS OTHERWISE SHOWN.
- ALL POLE DRILLINGS ABOVE GROUND LEVEL WHICH ARE NOT USED, MUST BE PLUGGED WITH APPROVED WOOD POLE PLUGS

POLE LENGTH (m)	DIM 'A' (m)
8.5 - 11.0	1.3
11.5 - 14.0	1.1
15.0 - 17.0	0.7
18.0 - 24.0	0.5

POLE SIZE TO BE IMPRESSED
ON POLE BUTT



System Design, Drawing Office, 3 Prenton Way, Prenton, CH43 3ET
Telephone 0151 6092491

Drawn TA	Date 11/10/06
Checked DJB	Date 12/10/06
Approved LC	Date 13/10/06

Title

33KV HEAVY CONSTRUCTION
'H' POLE MEMBER
DRILLING, SCARFING AND MARKING

Location OHL SPEC

Status

FOR ISSUE

Drg. No.

SP4009851

Rev.

2.0

© Copyright property of SP PowerSystems Ltd.

Scale

Size A4