

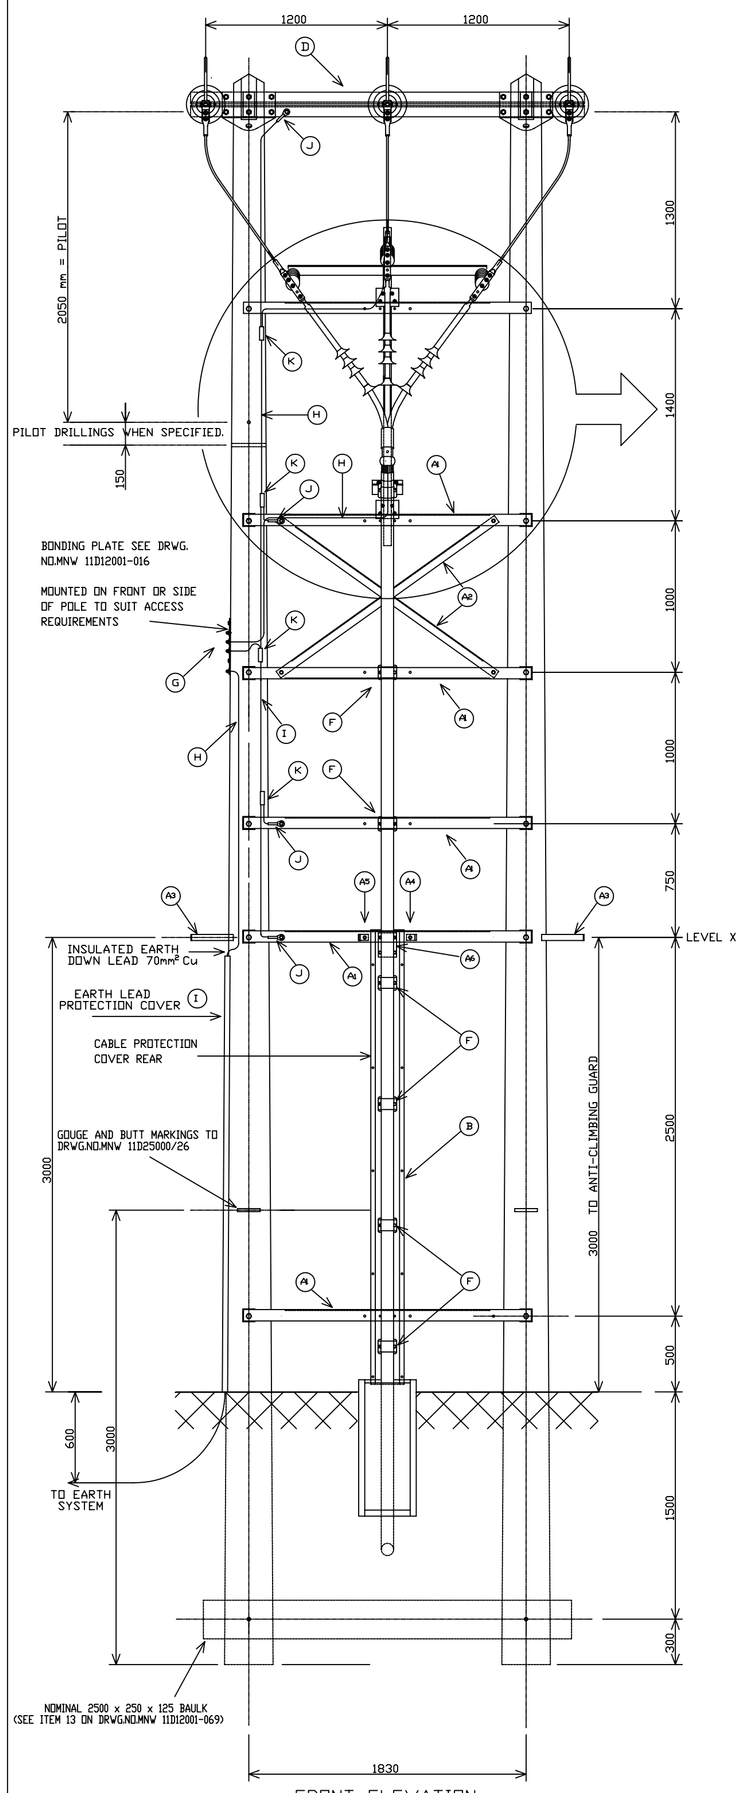



FRONT ELEVATION
(PROTECTIVE COVER REMOVED)
ARRANGEMENT FOR 'H' TYPE CABLE SHOWN.

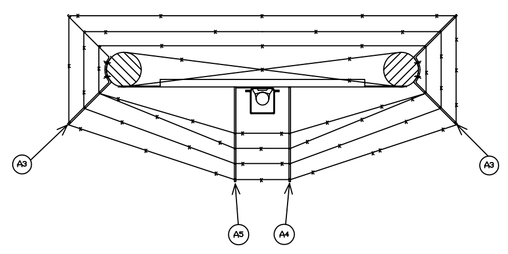


PLAN @ LEVEL X

10.5M CONSTRUCTION SHOWN

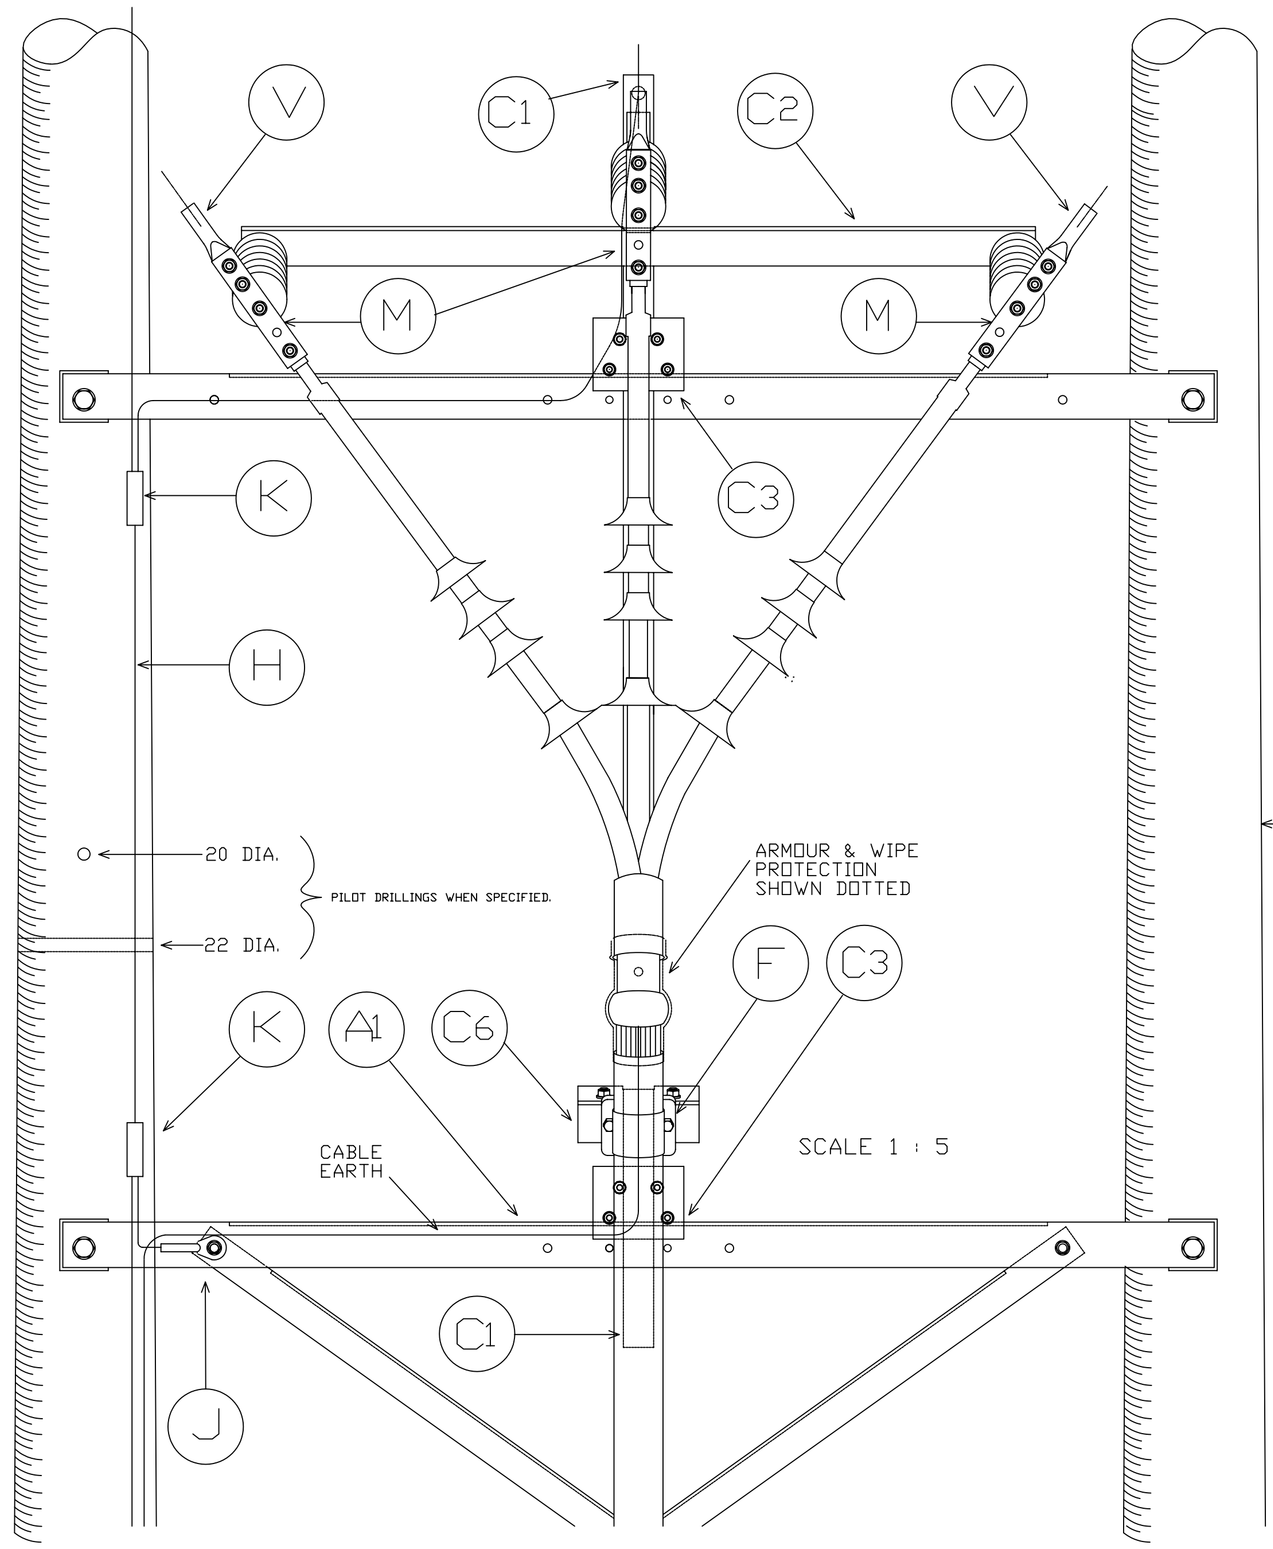

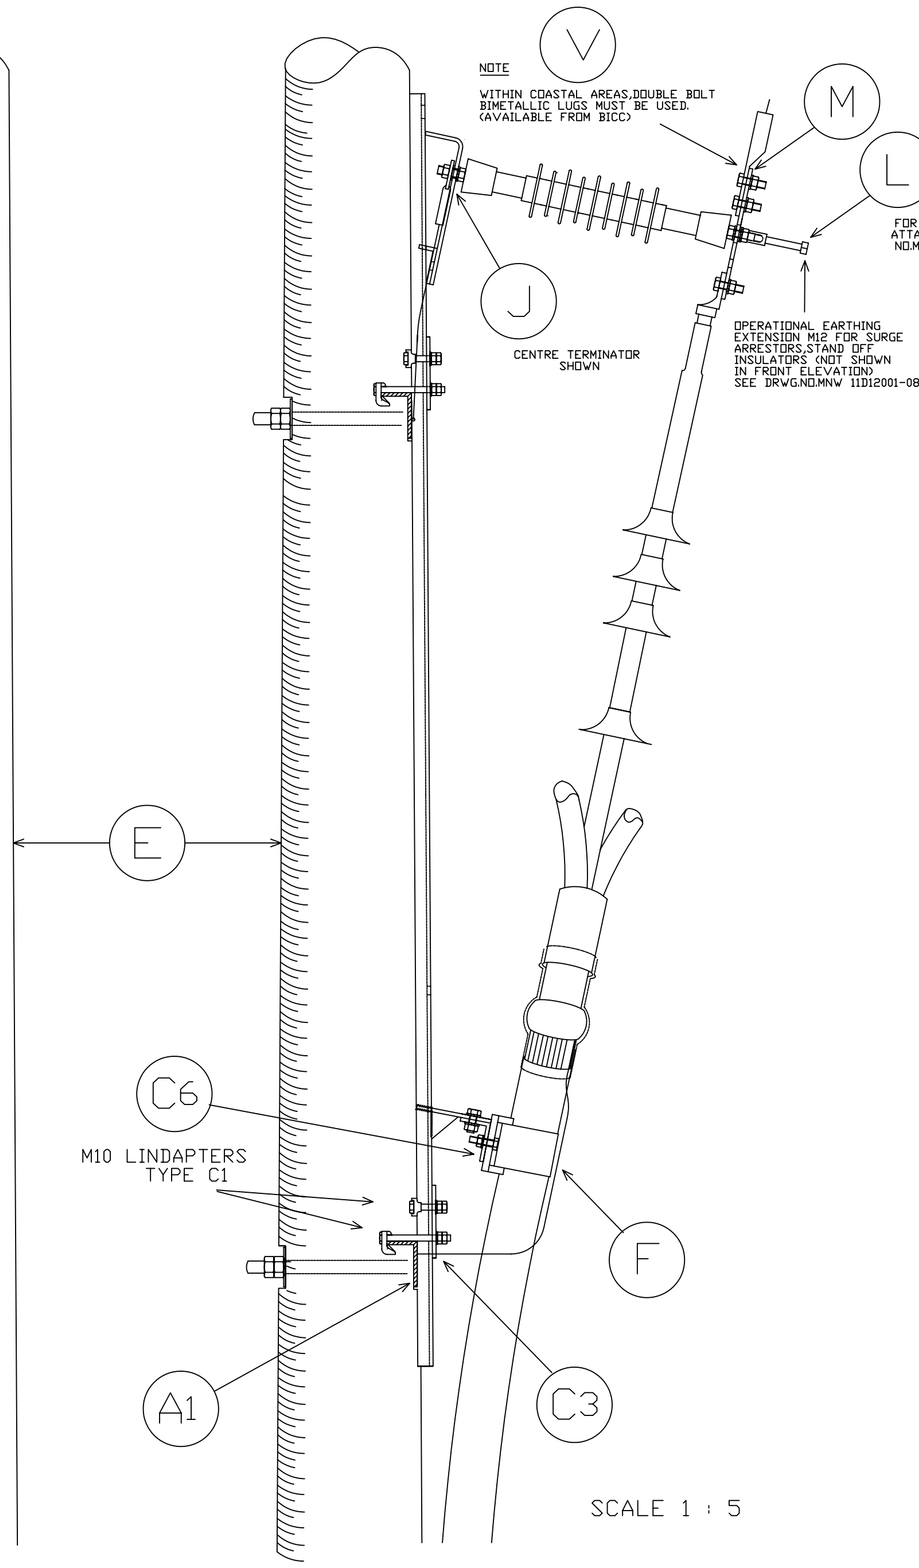

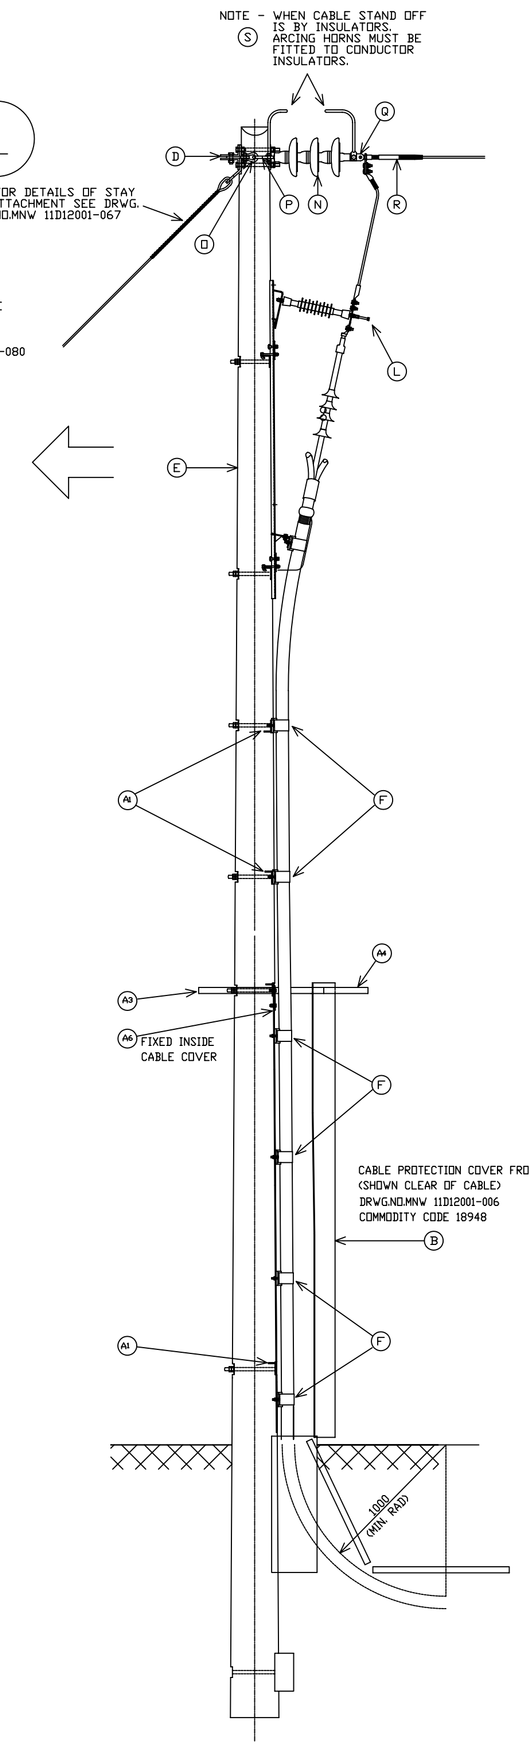

SECTION THROUGH CENTRE CONDUCTOR

(A) STEELWORK ITEMS TO DRWG.NO.MNW 11D12001-042 ---------- COMMODITY CODE 18960 (+ 18963 FOR ADDITIONAL HEIGHT STEELWORK)
(B) PROTECTIVE COVER TO DRWG.NO.MNW 11D12001-006 ---------- COMMODITY CODE 18948
(C) CRUCIFORM STEELWORK ITEMS TO DRWG.NO.MNW 11D12001-079 ---------- COMMODITY CODE 18964
(D) TERMINAL POLE CROSSARM STEELWORK SET TO DRWG.NO.MNW 11D12001-041 ------- COMMODITY CODE 18946
(E) TERMINAL H-POLE FABRICATION DETAILS TO DRWG.NO.MNW 11D12001-072
(F) B.I.C.C. MULTICLEAT REF 378-04 ---------- COMMODITY CODE 18968
(G) BONDING PLATE TO DRWG.NO.MNW 11D12001-16 ---------- COMMODITY CODE 17361
(H) CABLE BOND CONDUCTOR/P.V.C.INSULATED EARTH DOWNLEAD CONDUCTOR 70mm ---- COMMODITY CODE 12928
(I) EARTH LEAD PROTECTION COVER ---------- COMMODITY CODE 18956
(J) COMPRESSION LUG ---------- COMMODITY CODE 19125
(K) CRIMPET ---------- COMMODITY CODE 19212
(L) OPERATIONAL EARTHING EXTENSION TO DRWG NO. MNW11D12001-080---------- COMMODITY CODE 17362
(M) CONNECTION BAR FOR 33kV O/D TERMINATIONS DRWG.NO.MNW 11D12001-040 ------ COMMODITY CODE 14235
(N) TENSION INSULATOR 70KN (9 REQUIRED) ---------- COMMODITY CODE 17570 OR 17588
(O) 'D' SHACKLE REF:NO. 15/29 (3 REQUIRED) ---------- COMMODITY CODE 17970
(P) BALL ENDED EYE LINK REF:NO. 15/30 (3 REQUIRED) ---------- COMMODITY CODE 17971
(Q) SOCKET CLEVIS ADAPTOR REF:NO. 15/31 (3 REQUIRED) ---------- COMMODITY CODE 17972
(R) DEADEND EYE TERMINATION KIT FOR 100mm ACSR/150mm ACSR (3 REQUIRED) ----- COMMODITY CODE 17888/17910
(S) ARCING HORNS ---------- COMMODITY CODE 17973 & 17974
(T) DANGER OF DEATH SIGNS TO DRWG NO.53312 (BILINGUAL) & 53313 ---------- COMMODITY CODE 75978
(ENGLISH) FOR DETAILS OF POSITIONING SEE DRWG NO.MNW11D 12001-066 ------- COMMODITY CODE 75977 } NOT SHOWN
(U) POLE NUMBERS FOR DETAILS OF POSITIONING SEE DRWG NO.MNW11D 12001-066 --- COMMODITY CODE *****
(V) DOUBLE BOLT LUG FOR 150MM A.C.S.R. (3 REQUIRED)---------- COMMODITY CODE 17916

NOTE THIS DRAWING SHOWS A 3 CORE CABLE. THE ARRANGEMENT IS EQUALLY APPLICABLE TO THE USE OF 3 SINGLE CORE CABLES IN TREFOIL.

ALL DIMENSIONS ARE IN MILLIMETRES UNLESS OTHERWISE STATED

© Manweb plc

E	DRAWING MODIFIED TO LATEST SPEC.	P.J.HUMPHRAY 30/09/94
D	NEW TITLE BLOCK.	R.J.COLES. 18-8-93
C	POLE MODS' BAULK SCARFING & PILOT DRILLING.	R.J.COLES. 10-3-92
B	ITEM'N'INCLUDED ON SHEDULE OF PARTS.	R.J.COLES. 11-2-92
A	MODIFICATIONS TO CRUCIFORM FABRICATION	R.J.COLES. 13-11-91

Manweb NETWORK SERVICES DIVISION

DRAWN BY: R.J.COLES
DATE: 24-5-91
TRACED BY:
JOB No:
APPROVED BY: M.L.H.

OVERHEAD LINE STANDARD

ARRANGEMENT OF 33KV 'H' TYPE TERMINAL POLE WITH U/G CABLE
(ALL TERMINATOR ARRANGEMENTS)

MNW11D 12001/043 A0 SCALE: 1:20 & 1:5