

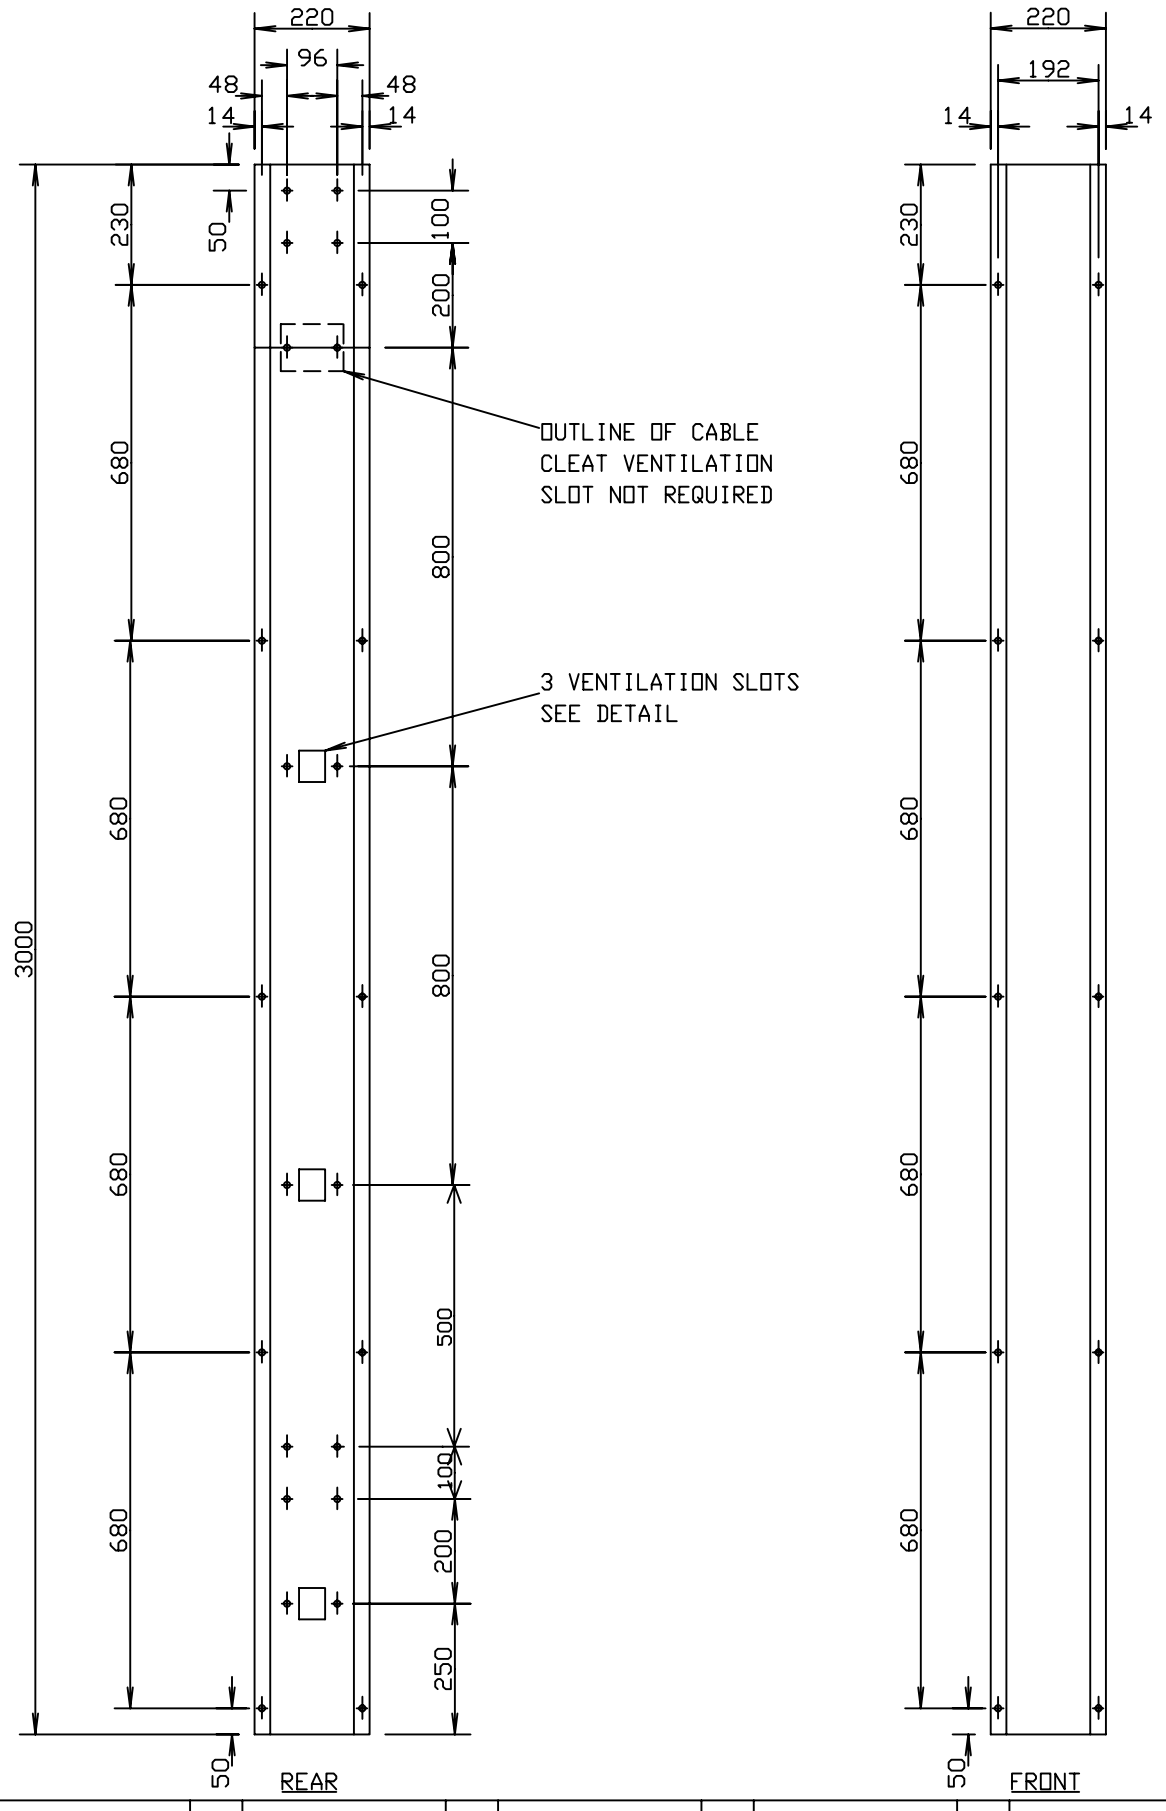


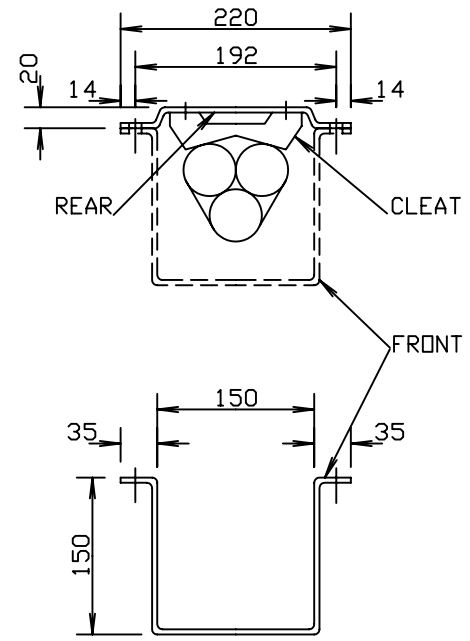

MATERIAL - 5 THICK GRP

PLAN OF CABLE PROTECTION
COVER AND CLEAT

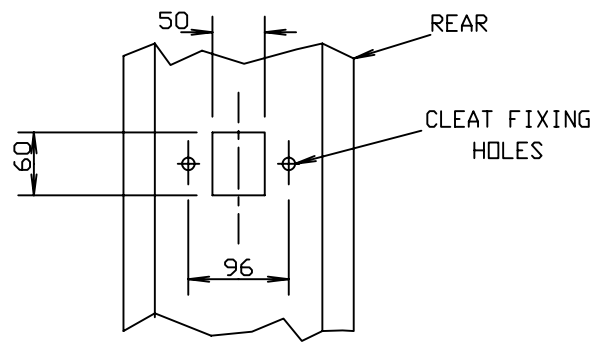

DETAIL OF VENTILATION SLOT SCALE: -1: 5

NOTES

1, MATERIAL 5mm THICK GRP
2, ALL HOLES 12 DIA
3, CABLE COVER TO BE SUPPLIED WITH 10 GALVANISED M10×25mm LONG SETBOLTS WITH HEX. NUT & 2 WASHERS

COMMODITY CODE 18948

ALL DIMENSIONS ARE IN MILLIMETRES UNLESS OTHERWISE STATED

© Manweb plc

E	NEW TITLE BLOCK ADDED.	P. J. H. 28/07/94
D	2-ADDITIONAL HOLES FOR SINGLE POLE MOUNTING. NEW TITLE BLOCK.	R. J. C. 24/04/91
C	MODIFIED & REDRAWN, LENGTH WAS 2900.	B. B. G. 07/10/87

Manweb NETWORK SERVICES DIVISION

DRAWN BY:	B. B. G.
DATE:	07/10/87
TRACED BY:	
JOB No:	
APPROVED BY:	M. L. H.

OVERHEAD LINE STANDARD

33kV TERMINAL POLE (NEW DESIGN)
CABLE CLEAT & PROTECTIVE COVER

MNW 11D 12001-006 A2 | SCALE: 1: 10