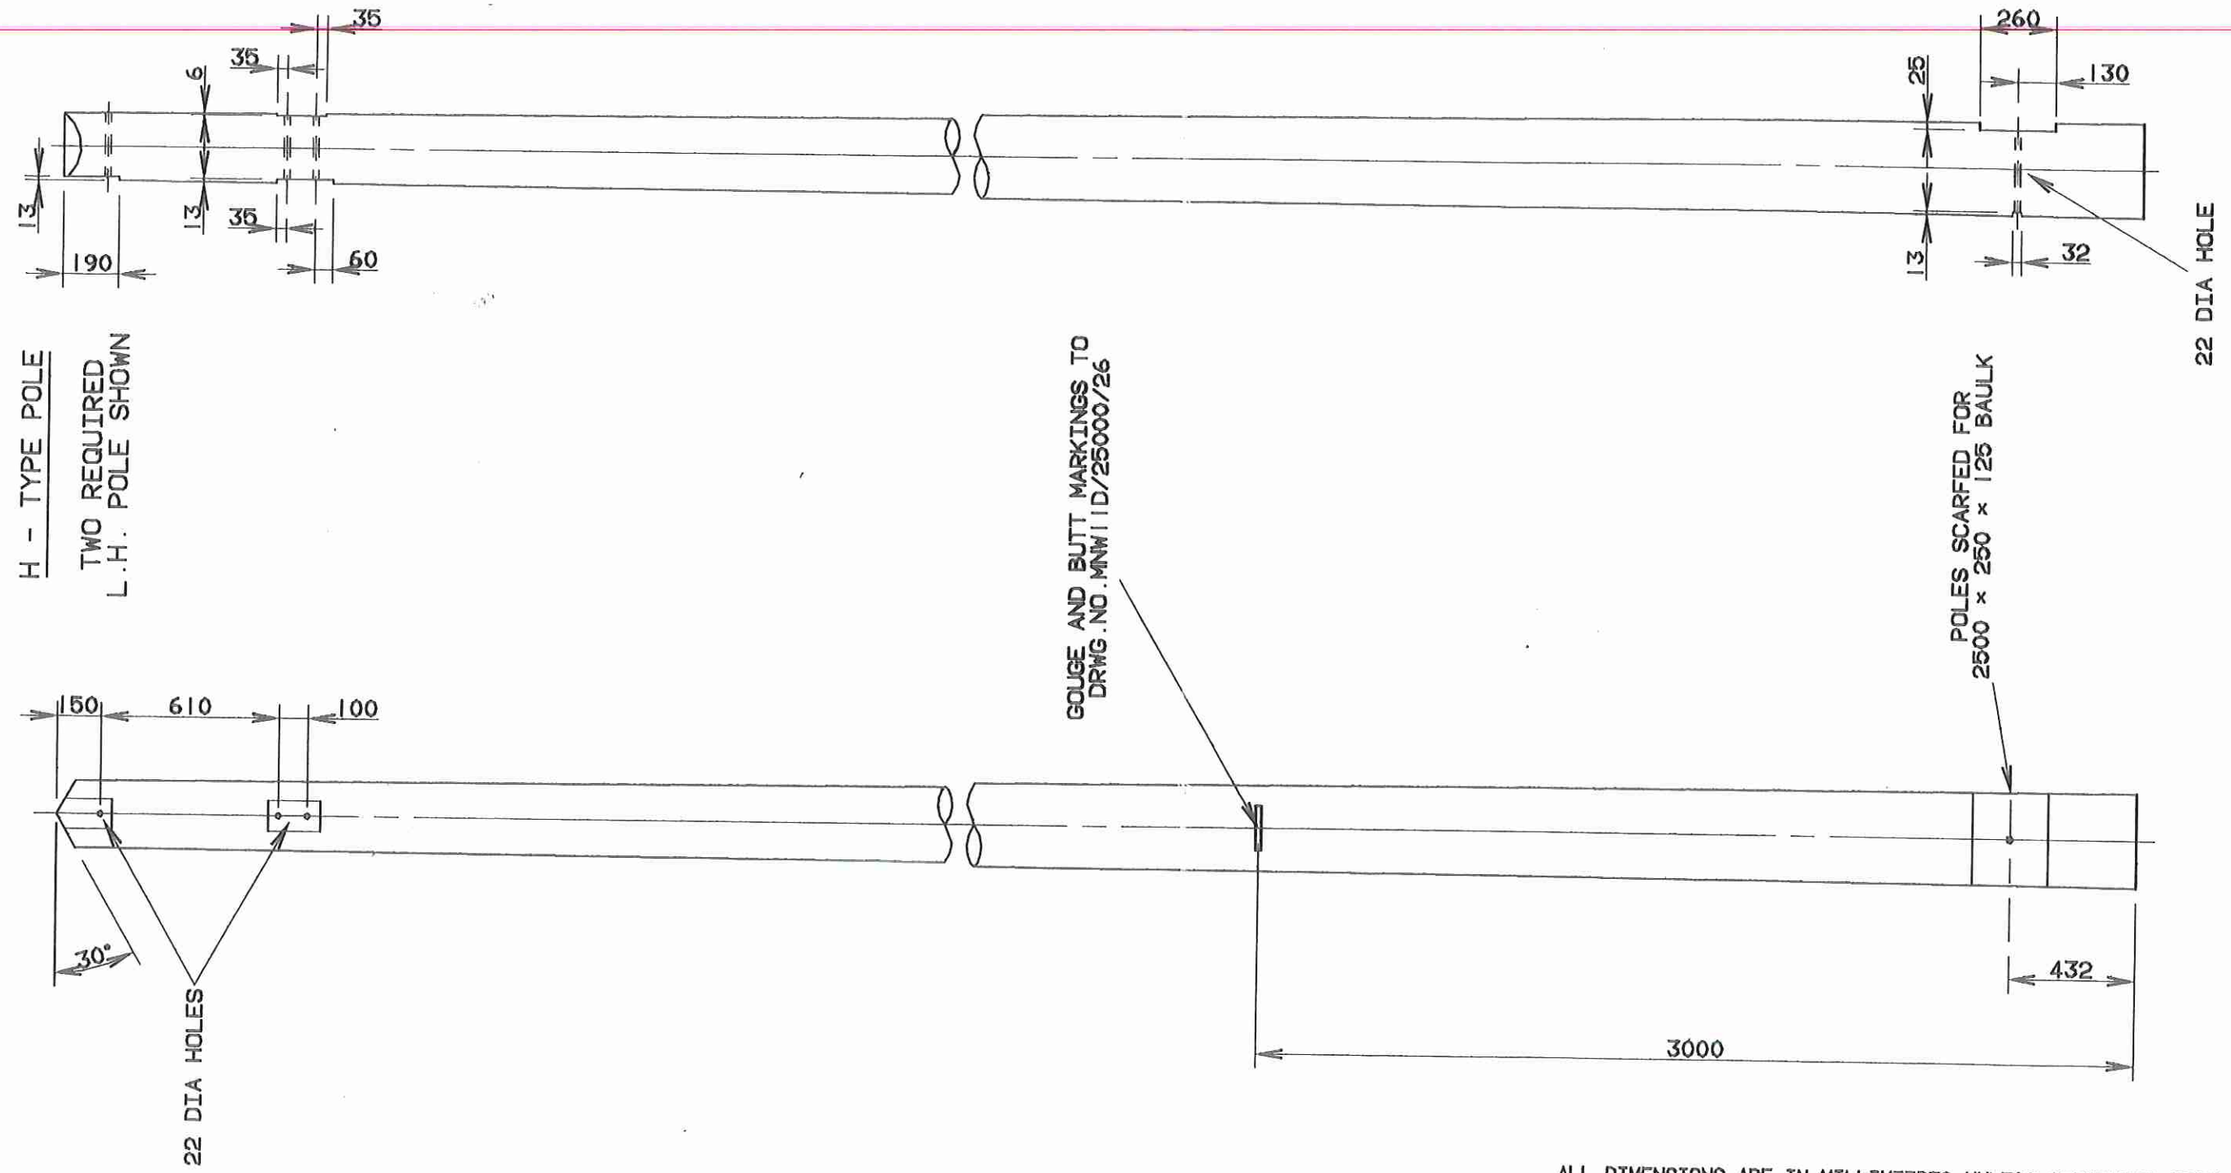


ALL DIMENSIONS ARE IN MILLIMETRES UNLESS OTHERWISE STATED

Manweb NETWORK SERVICES DIVISION

DRAWN BY: P.J.H.
DATE: 30/09/94
TRACED BY:
JOB No:
APP'D BY: P.DUMAYNE

OVERHEAD LINE STANDARD

FABRICATION DETAILS OF 33kV TERMINAL H - POLE, O/H SUBSTATION ENTRY

MNW 11D 12001 - 073 A3

SCALE: 1:20

© Manweb plc