


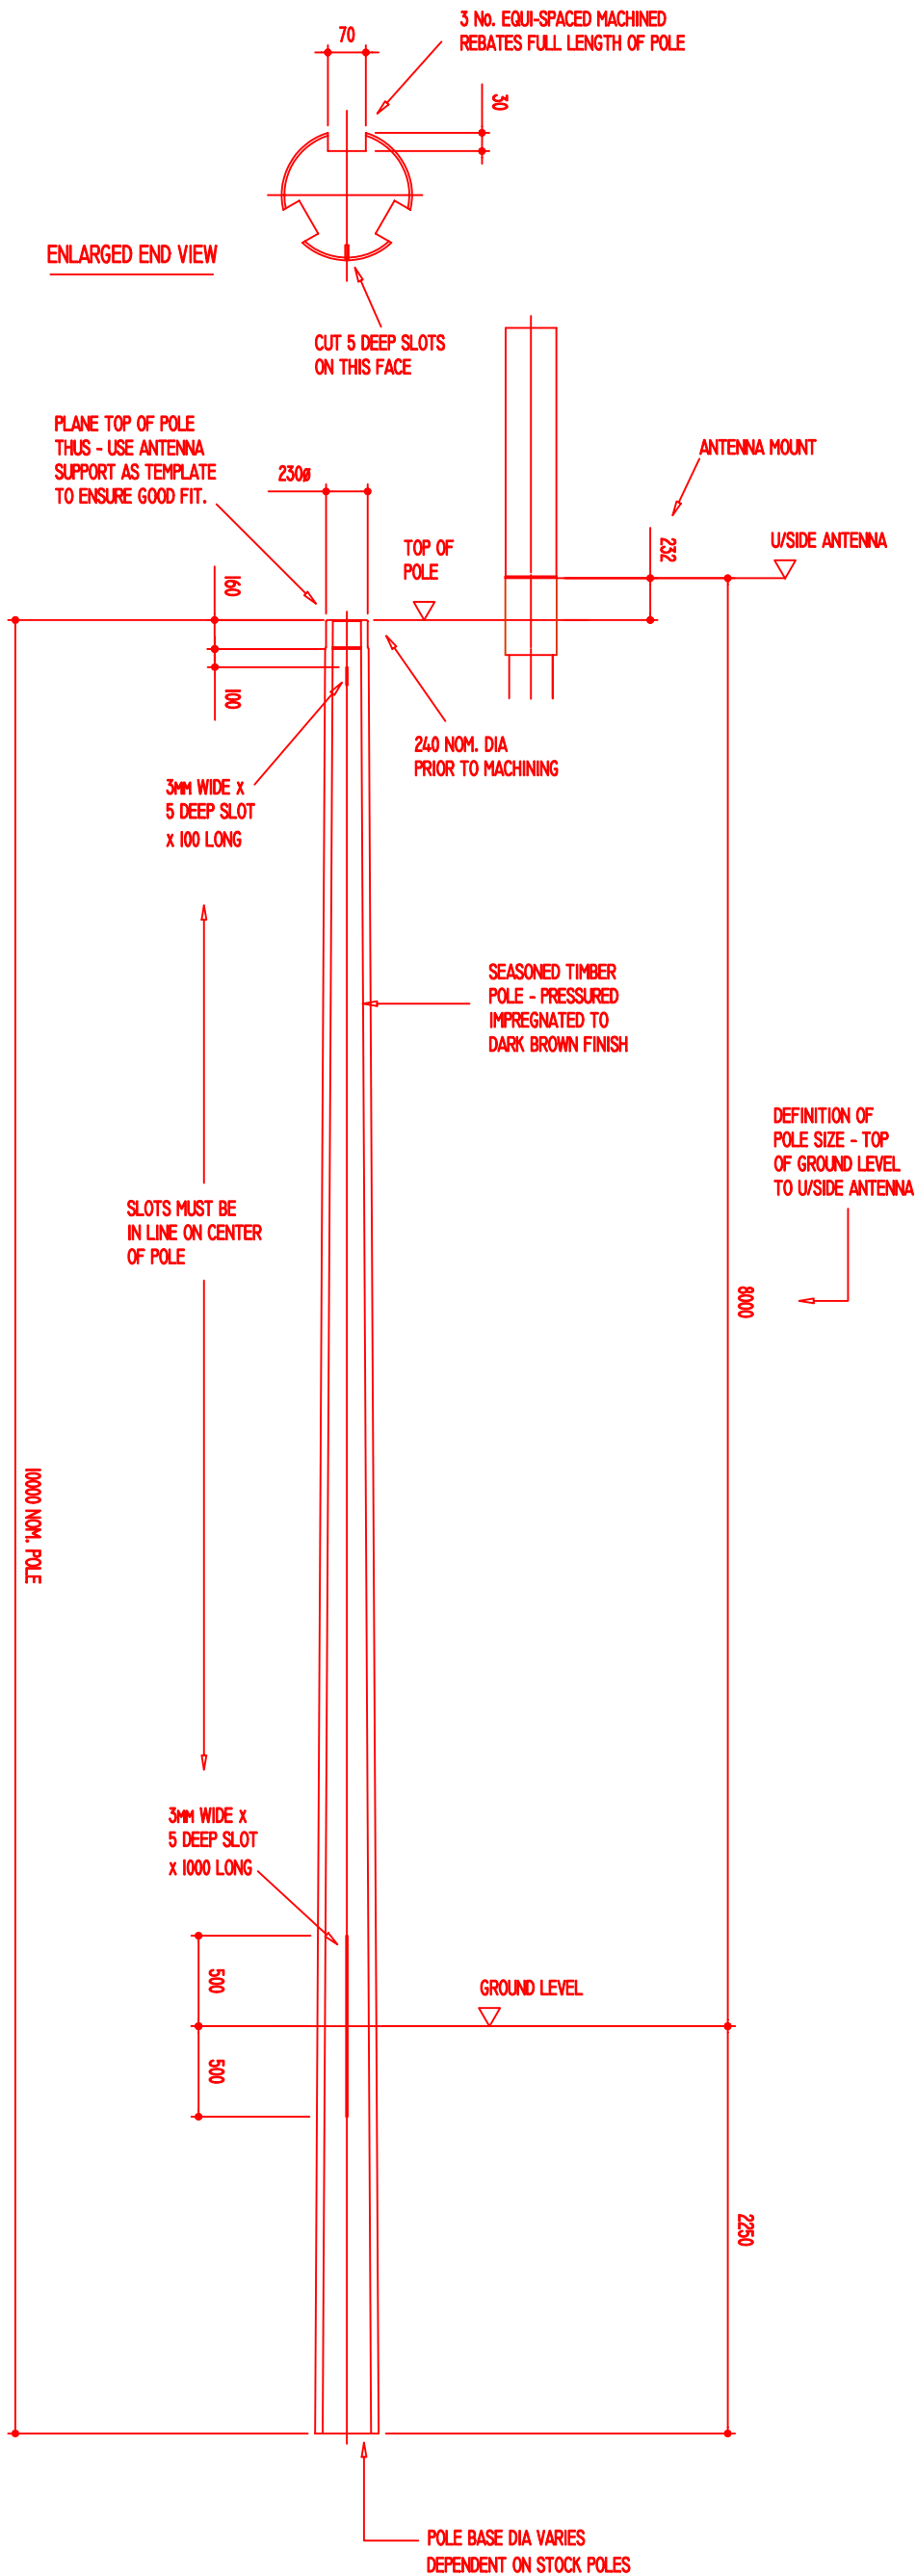

ORIGINAL DRG. SIZE				ITEM REF		QUANTITY		TITLE/NAME, DESIGNATION, MATERIAL, DIMENSION ETC			ARTICLE NO./REFERENCE		SCALE	
A3				DRAWN BY MC		CHECKED BY NK		APPROVED BY - DATE			FILENAME		DATE	
2004				MASTS TOWERS & ANTENNAS LTD.		THE OLD POWER STATION, THE SLADE, TONBRIDGE, KENT. TN9 1HR		TEL. 01732 770813 FAX. 01732 368067			TITLE WALDON TELECOM		MACHINING DETAILS OF 8M TIMBER POLE FOR VODAFONE ANTENNAS	
COPYRIGHT MTA LTD				MTA/WT/12951/06		REV. A								