


A schematic diagram of a suspension bridge. At the top, the text "LINE CONDUCTORS" is centered. Below it, a horizontal line represents the bridge deck. Above the deck, there are two vertical lines representing the main suspension cables. These cables are supported by two large vertical pillars (pylons) in the center. From each pylon, several diagonal lines (stays) extend down to the deck. At the ends of the bridge, there are two smaller vertical pillars. The text "STAYS" is centered below the diagram.

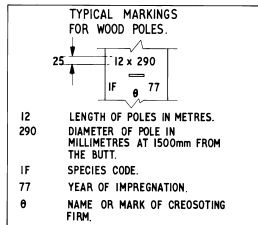

I. ALL HOLES TO BE 22mm DIA UNLESS OTHERWISE STATED.

II. 75x6x6mm GUDGE MARK 3000mm UP FROM BUTT ON INSIDE OF LEGS.

III. BUTT TO BE SAWN OFF SQUARE TO THE AXIS OF THE POLE

IV. POLE TO BE MARKED AS PER. INSET.

V. IT IS ESSENTIAL THAT THE DRILLINGS ARE TO BE MADE TO COMPLETE ARE ACCURATE AND DEAD CENTRE.


VI. LEGS OF 'N' POLE TO BE CAREFULLY MATCHED.

VII. THE FOLLOWING INFORMATION TO BE IMPRESSED ON END GRAIN OF BUTT OF POLE :-

a) LENGTH AND DIAMETER OF POLE

b) POLE NUMBER IN ACCORDANCE WITH SCHEDULE.

NOTE:- THE PERSONAL MARK OF THE POLE INSPECTOR WILL BE IMPRESSED ON THE BUTT

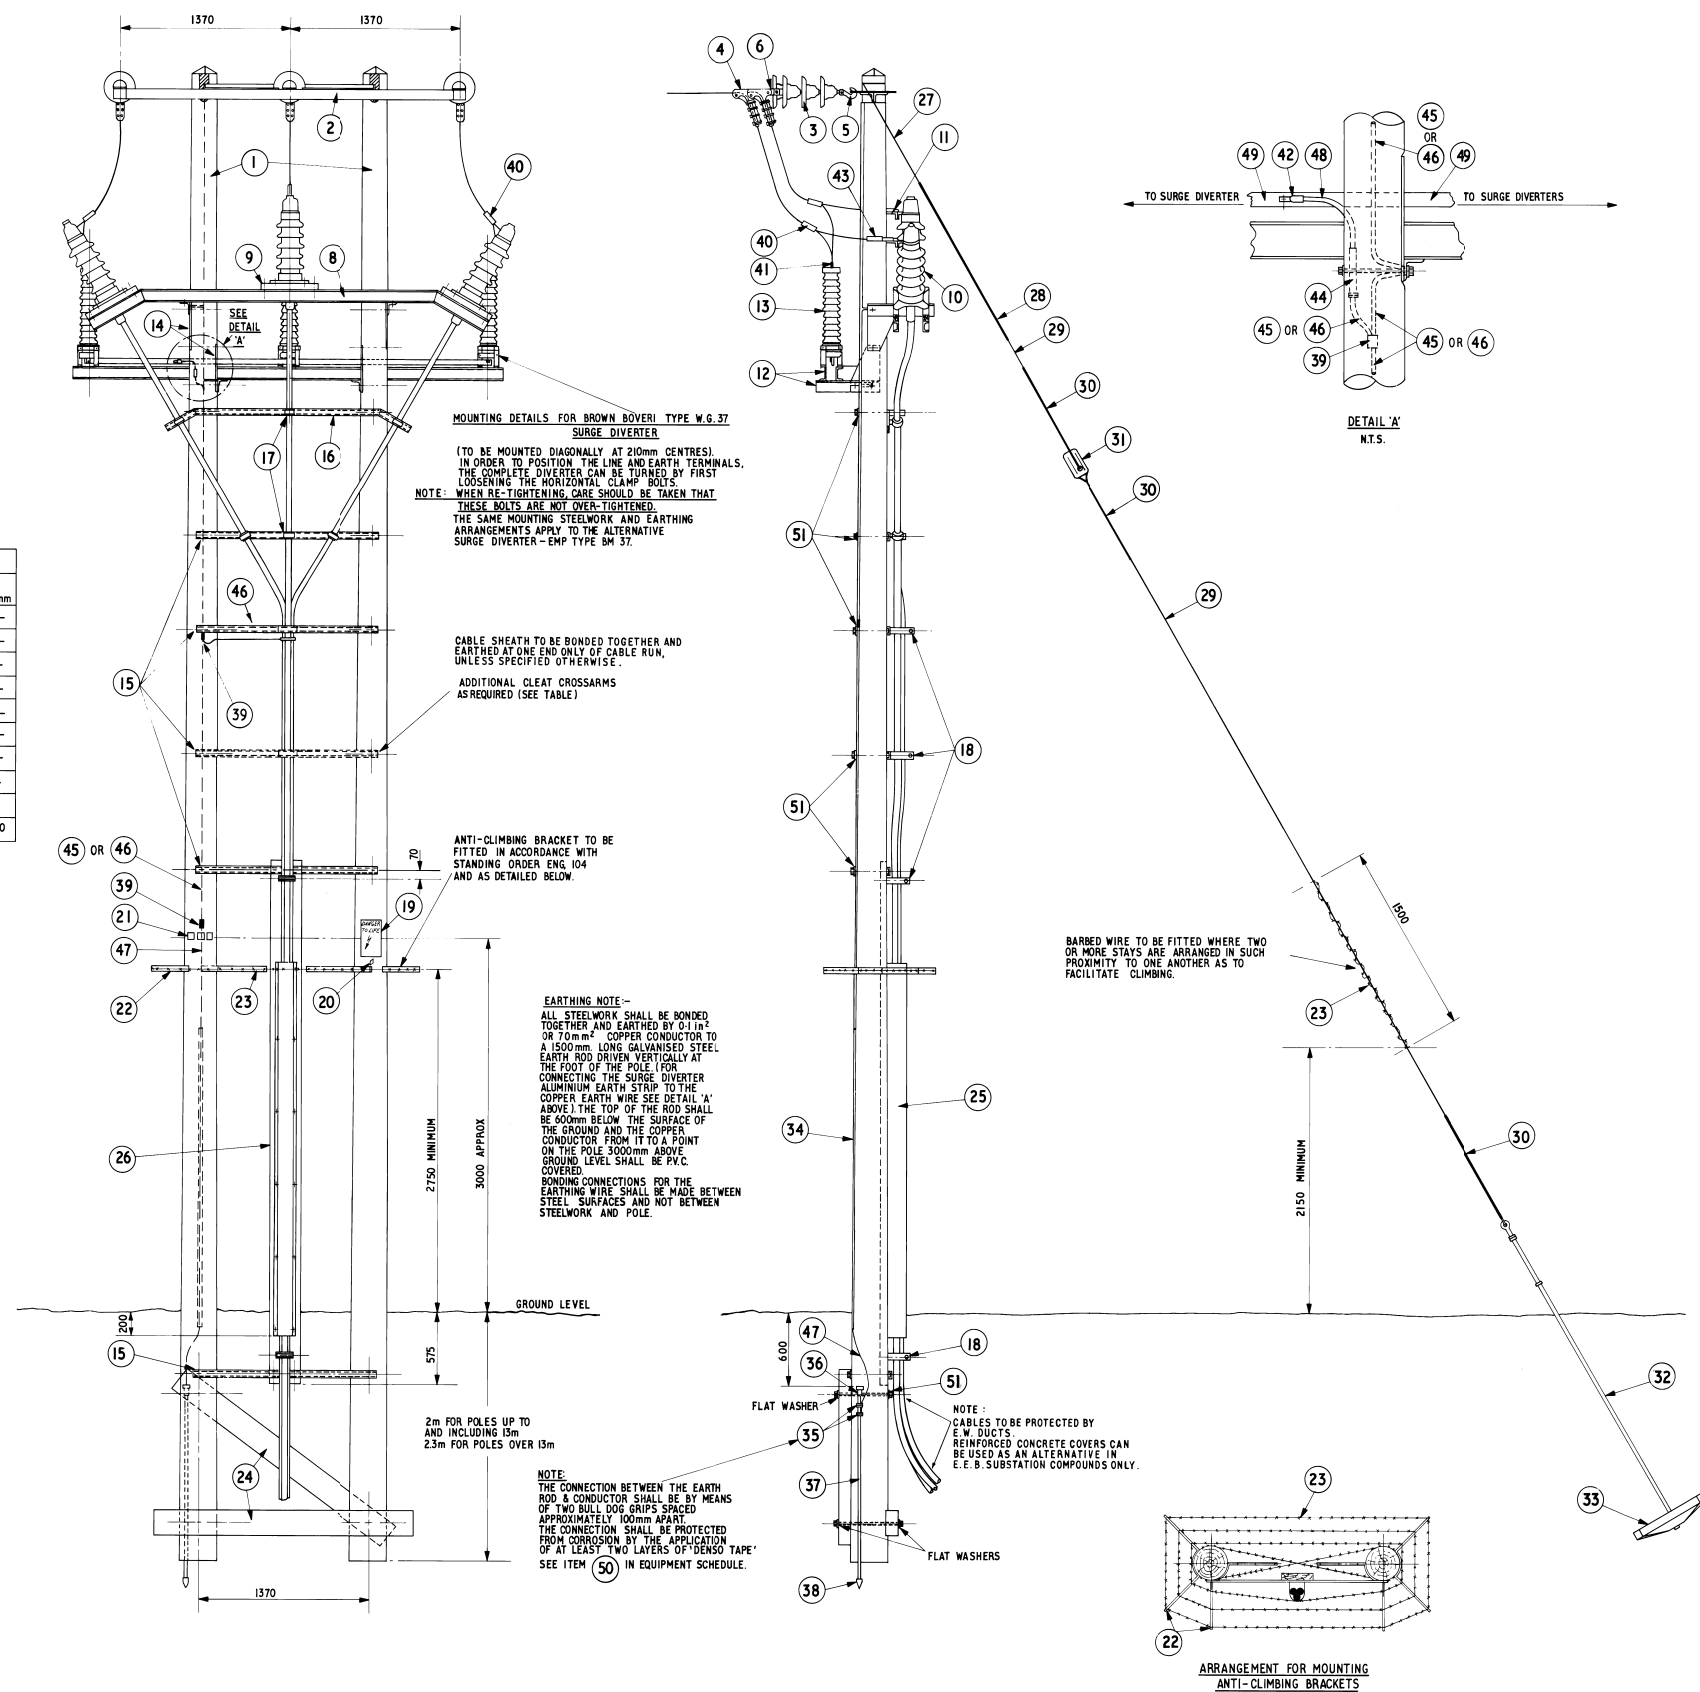

EQUIPMENT SCHEDULE		
ITEM No.	DESCRIPTION	DRG. No.
1	POLE	SPECIFICATION
2	CROSSARM	S.18634 B
3	10" (254mm) DISC INSULATOR	S.1904 2 S
4	CONDUCTOR TERMINATING CLAMP	S.20202 C
5	BALL ENDED HOOK	S.19003 V
6	SOCKET TONGUE	S.18640 X
7		
8	SEALING END SUPPORTING BRACKET	S.18250 P
9	SEALING END BATTENS	—
10	SEALING END	—
11	SEALING END CONNECTOR PLATE	S.01056 R
12	SUPPORTING STEELWORK FOR SURGE DIVERTERS	S.18222 Z
13	SURGE DIVERTER	18 0 50 F
14	GUSSET PLATE	S.19221 C
15	BACKBOARD AND CLEAT CROSSARM	S.18632 J
16	CLEAT SUPPORTING CHANNEL	S.18635 S
17	SINGLE WIRE CABLE CLEAT (NEOPRENE INSERT)	S.18412 C
18	TREFOIL CABLE CLEAT (SINGLE BOLT FIXING)	S.18405 E
19	DANGER NOTICE	S.19214 V
20	NUMBER / LETTER PLATE	S.19217 18
21	PHASE IDENTIFICATION PLATES	S.19217 97
22	ANTI-CLIMBING BRACKET	S.19231-33
23	BARBED WIRE	S.18916 R
24	CABLE BLOCK, 2100 x 200 x 100 mm	S.19977 X
25	BRACE GLUG, 3003mm LONG	S.18059 J
26	WOOD BACKBOARD, 4200 x 250 x 50mm	S.18933 F
27	POLE TOP MAKE OFF	S.18054 Q
28	LINE SPLICE	S.19426 E
29	STAY WIRE	S.19432 C
30	GUY GRIP DEAD END	S.19984 E
31	STAY INSULATOR	S.19427 N
32	22 mm DIA ADJUSTABLE STAY ROD.	S.1962M
33	STAY BLOCK.	S.19391K
34	PVC EARTH WIRE GUARD 2400mm LONG	S.18065 G
35	BULL DOG GRIP (2 No. REQ.)	S.18942 Z
36	COUPLING	S.19355F
37	1500mm LONG EXTENSIBLE EARTH ROD.	S.19355Y
38	DRIVING POINT	S.19355P
39	COPPER CRIMPIT	S.19357 G
40	CABELOG CRIMPIT	2107X
41	ALUMINIUM LUG	21215 N
42	ALUMINIUM LUG	21131 P
43	BI-METAL LUG	2121G
44	BI-METAL STRAP	20968 F
45	RECOVERED 0.1in(7/136) H.D. BARE COPPER	21288 S
46	70mm ² (19/2.14) S.D. BARE ANNEALED COPPER	05299 Q
47	70mm ² (19/2.14) P.V.C. COVERED ANNEALED COPPER	05300 X
48	100mm ² (17/4.39) BARE ALUMINOUM	05657 S
49	ALUMINIUM STRIP (40x5mm AL ALLOY-EGE-H 108 S 2898)	05130M
50	"DENS'O" TAPE, 50mm WIDE	14095 V
51	CURVED WASHER FOR M20 DIA. BOLTS	12891 R
52		S.09190 R

eastern electricity 

ENGINEERING DIVISION

33kV TERMINAL POLE
SEALING END
ARRANGEMENT.

1:20

5/BI007

C