


FOR 200mm C.S.R.
MAXIMUM SPAN
BARE CONDUITS 1.5m
PVC COVERED W/ JOINTS 2.5m
MAXIMUM ANGLE OF DEVIATION

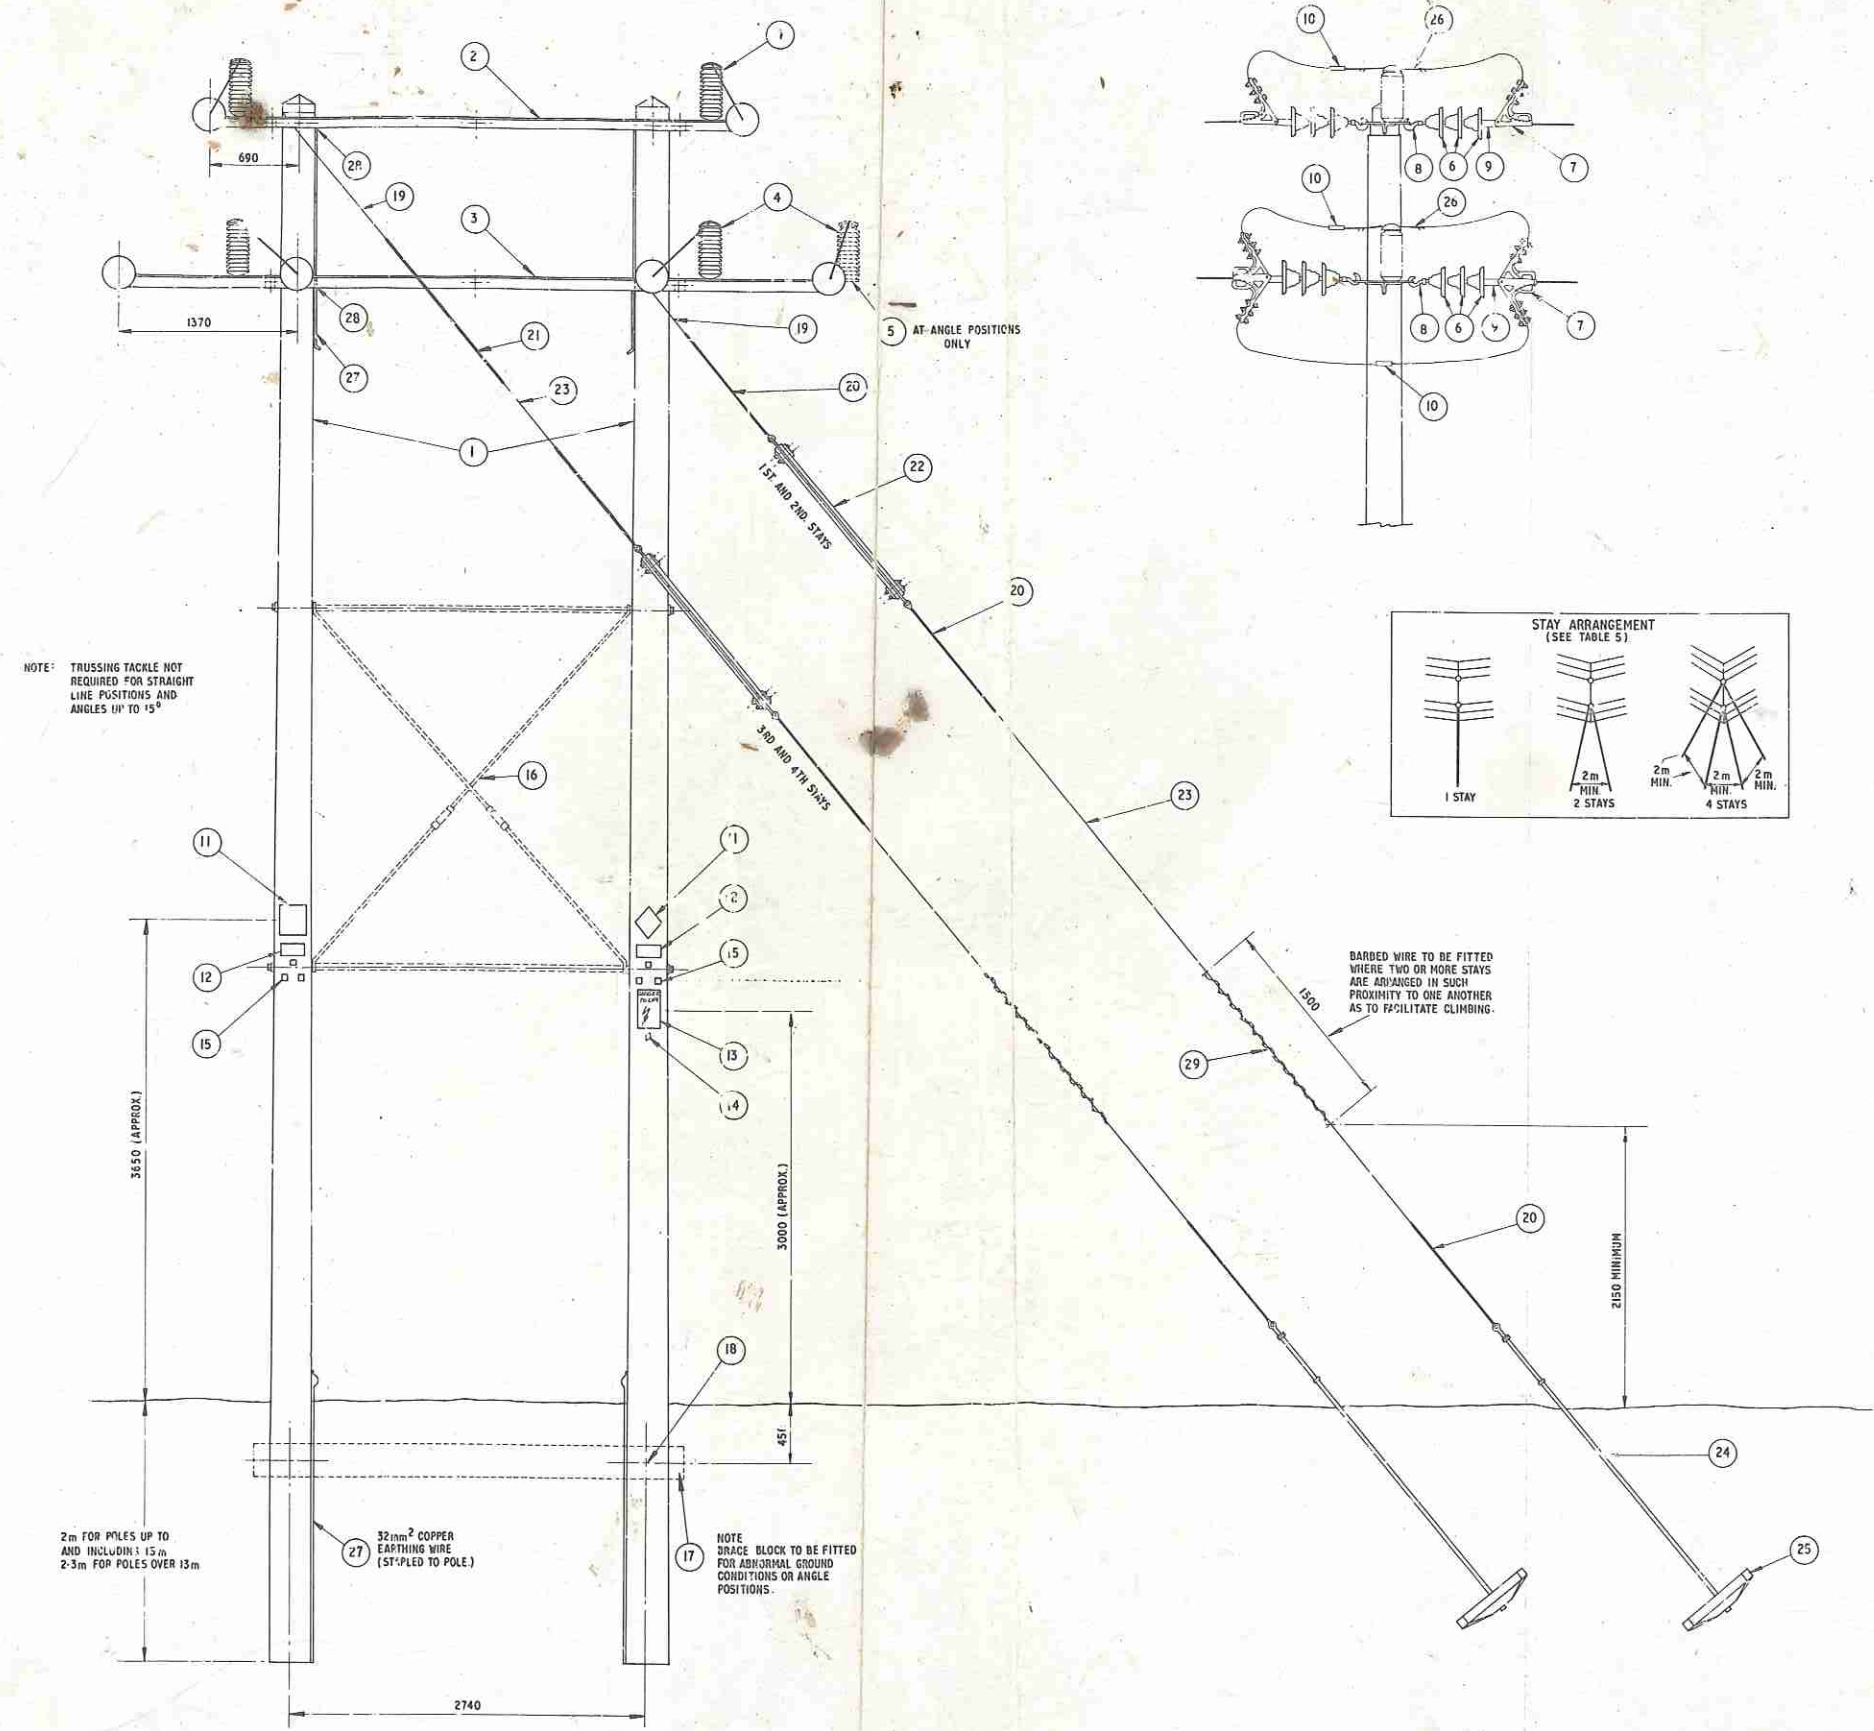

A	19.1.00	REF. 30017-12-200 DIMEN- 1000 1000 300 4/19	1000 1000 300 4/19	1000 1000 300 4/19
Hour	Date	Location	C.A.T.	EDP
eastern electricity				
CHIEF ENGINEER'S DEPARTMENT				
33kV DOUBLE CIRCUIT (UNEARTHED) ANGLE / SECTION POLE.				
SCALE 1:20				
DRAWING NO. 5/D1094				