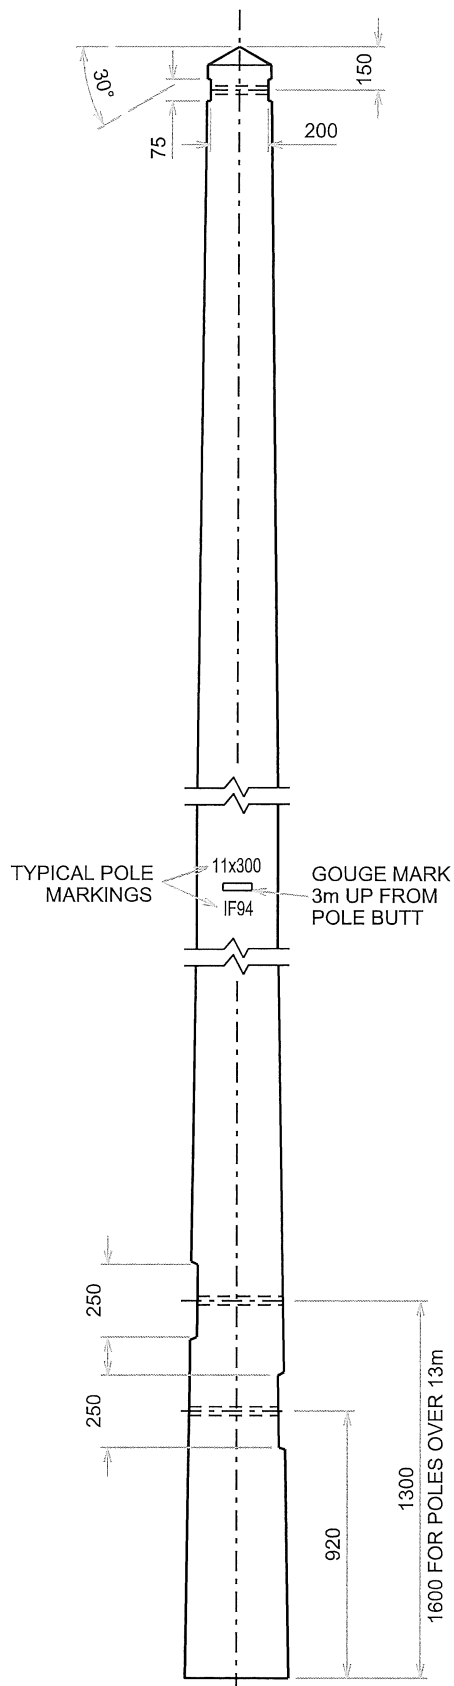


NOTES

1. ALL HOLES SHALL BE 22mm DIA. UNLESS STATED OTHERWISE.
2. HOLES TO BE DRILLED TO TEMPLATE, ACCURATE AND DEAD CENTRE.
3. THE TWO LIMBS COMPRISING THE "H" POLE SHALL BE MATCHED BY THE SUPPLIER.

All dimensions in millimetres

Section H Pole, Max Deviation 60°
11/33kV Heavy Construction Lines

© UK Power Networks 2014

DRN. June 1994	DRAWING NUMBER	ISSUE
CKD.	EDS 01-9000.09	1
APP.		