


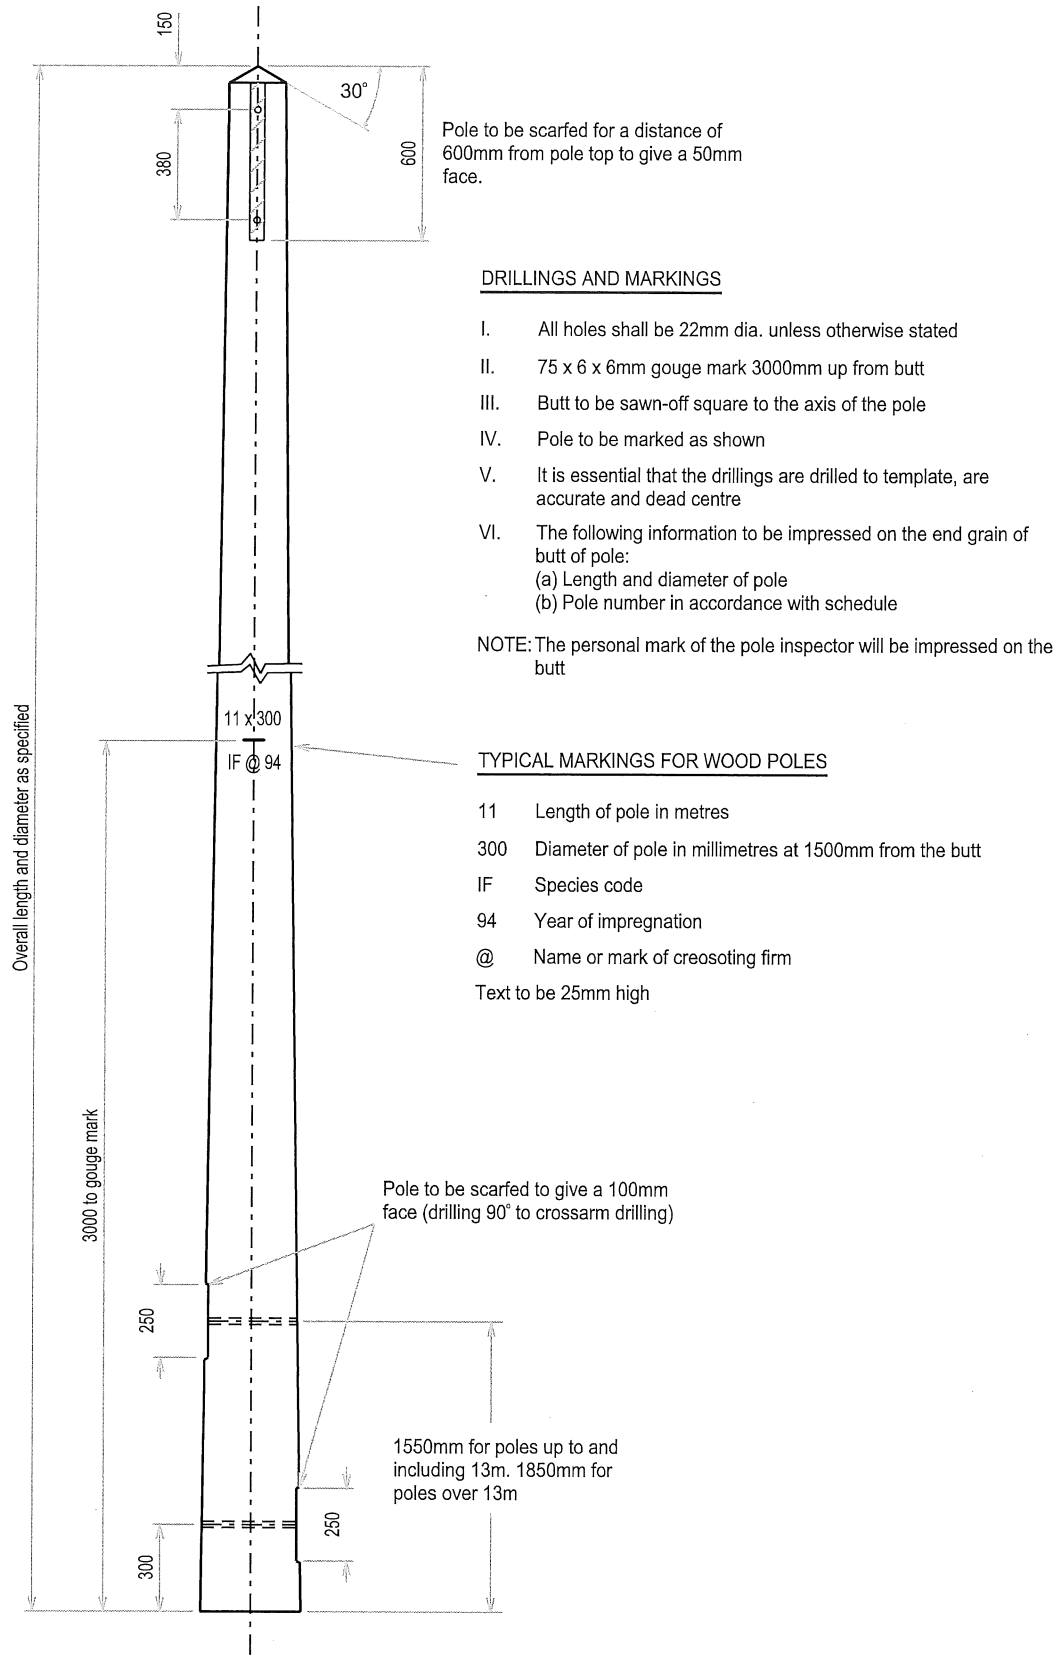

33kV Single Circuit Intermediate Pole

Based on EPN drawing 4/B1000

© UK Power Networks 2014

DRN. RDH 24.06.94	SPECIFICATION DRAWING NUMBER	ISSUE
CKD.	EDS 01-9000.103	1
APP.		