


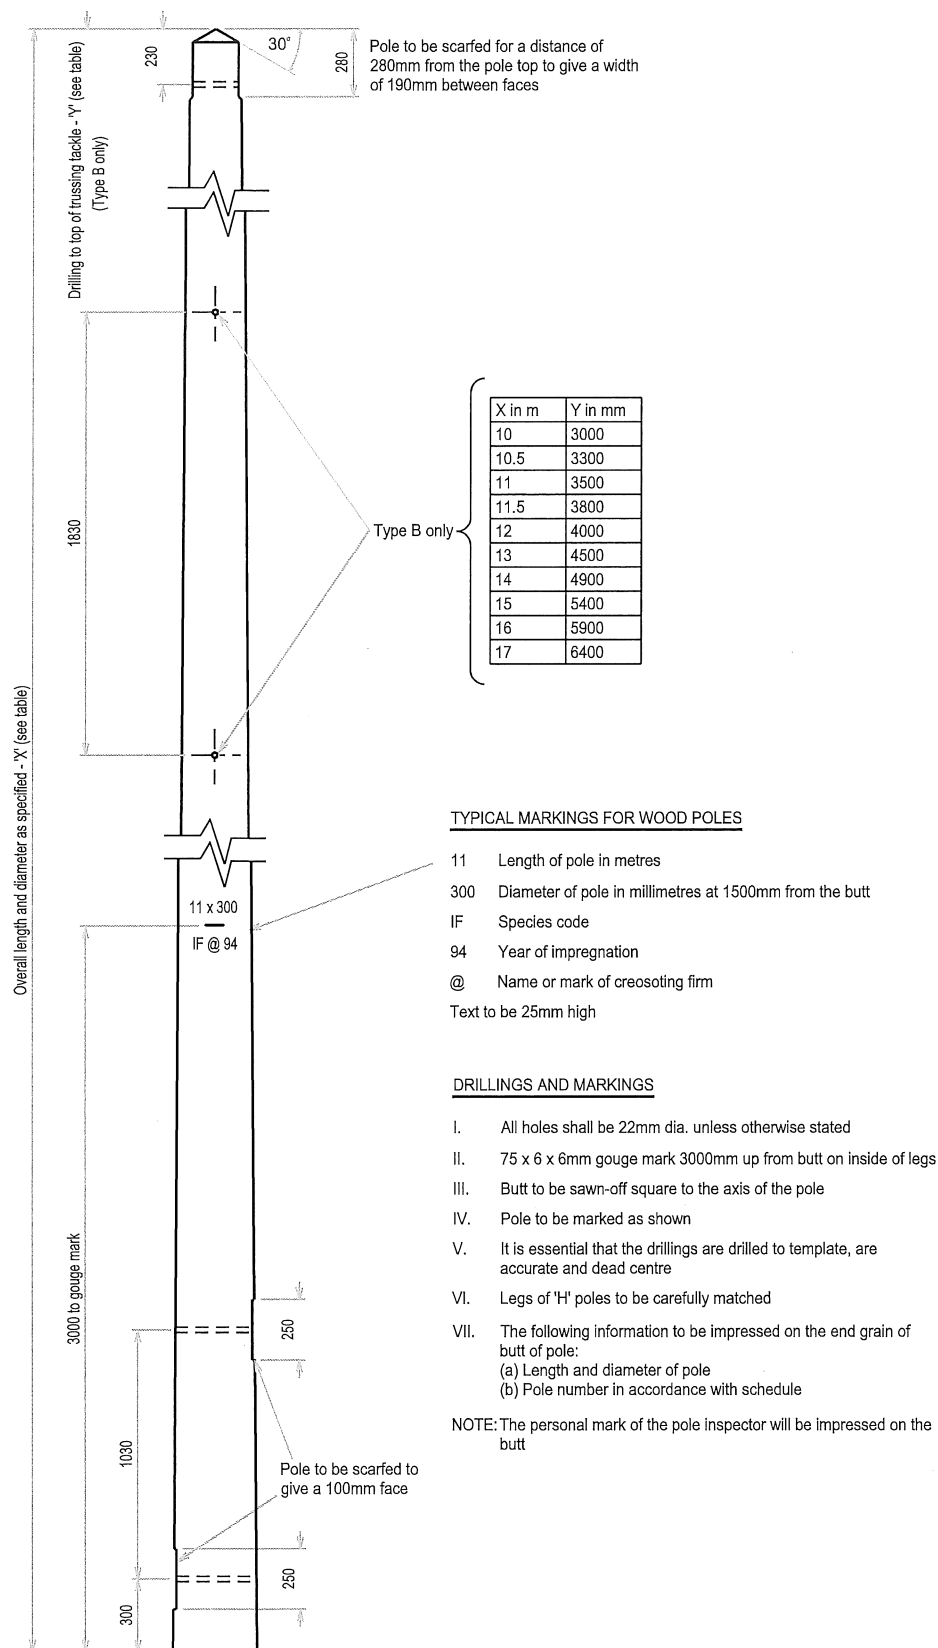

33kV Single Circuit Angle/Section Pole

Based on EPN drawing 4/B1002

© UK Power Networks 2014

DRN. RDH 17.12.13	SPECIFICATION DRAWING NUMBER	ISSUE
CKD.	EDS 01-9000.105	1
APP.		