


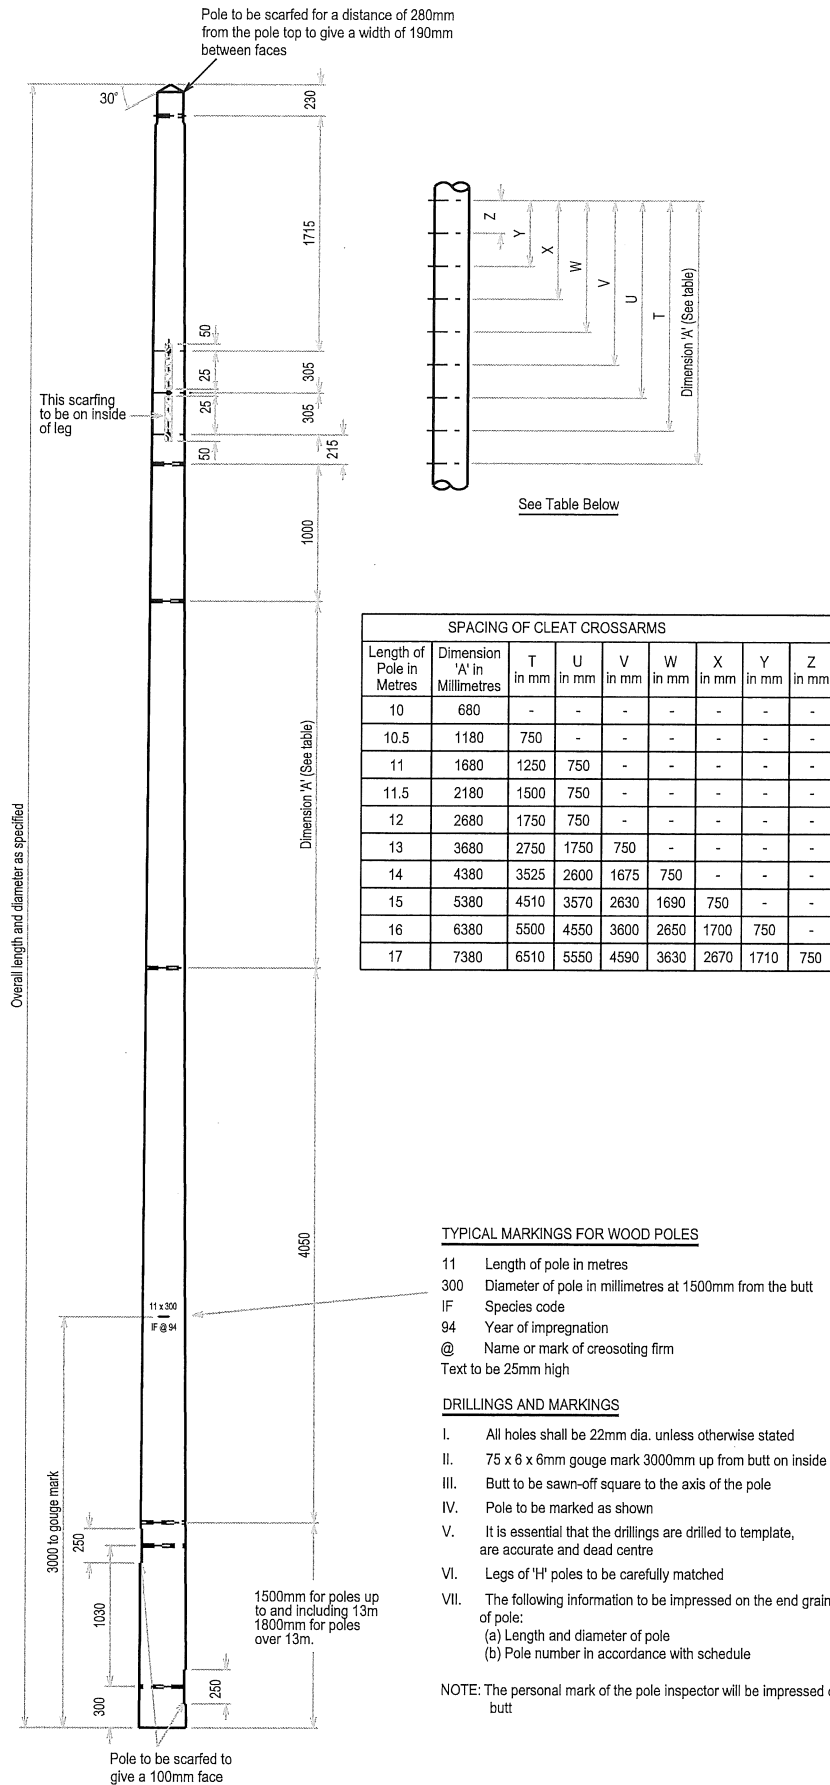

33kV Terminal 'H' Pole

Based on EPN drawing 5/B1007

© UK Power Networks 2014

DRN. RDH 18.12.13

CKD.

APP.

SPECIFICATION
DRAWING NUMBER

EDS 01-9000.106

ISSUE

1