


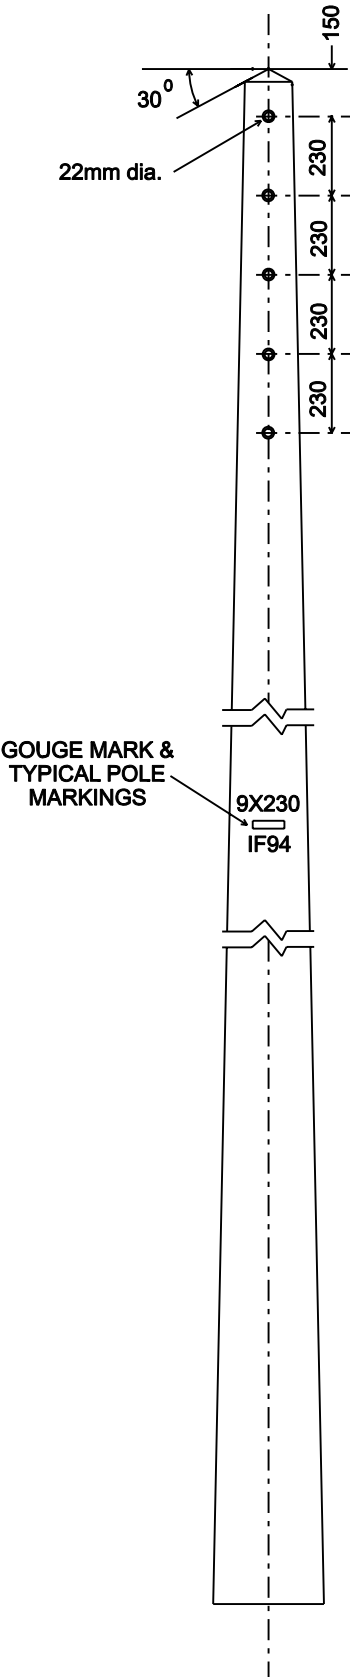

NOTES

1. ALL HOLES SHALL BE 18 mm DIA. WITH THE EXCEPTION OF THE TOP WHICH WILL BE 22 mm DIA.
2. HOLES SHALL BE DRILLED TO TEMPLATE, ACCURATE AND DEAD CENTRE.

All dimensions are shown in millimetres

**INTERMEDIATE POLE
L.V. LINES & SERVICES**

© EDF Energy 2006

DRN.	RDH 23.06.94	SPECIFICATION DRAWING NUMBER	ISSUE
CKD.	DCM 18.07.94		
APP.	DCM 18.07.94	ES 1-9000.1	1