


POLE 1 INFORMATION

POLE GRADE - STOUT.
POLE LENGTH - 13.0m.
POLE DIAMETER - 320mm*.


*FROM 1.5m OF BUTT END.

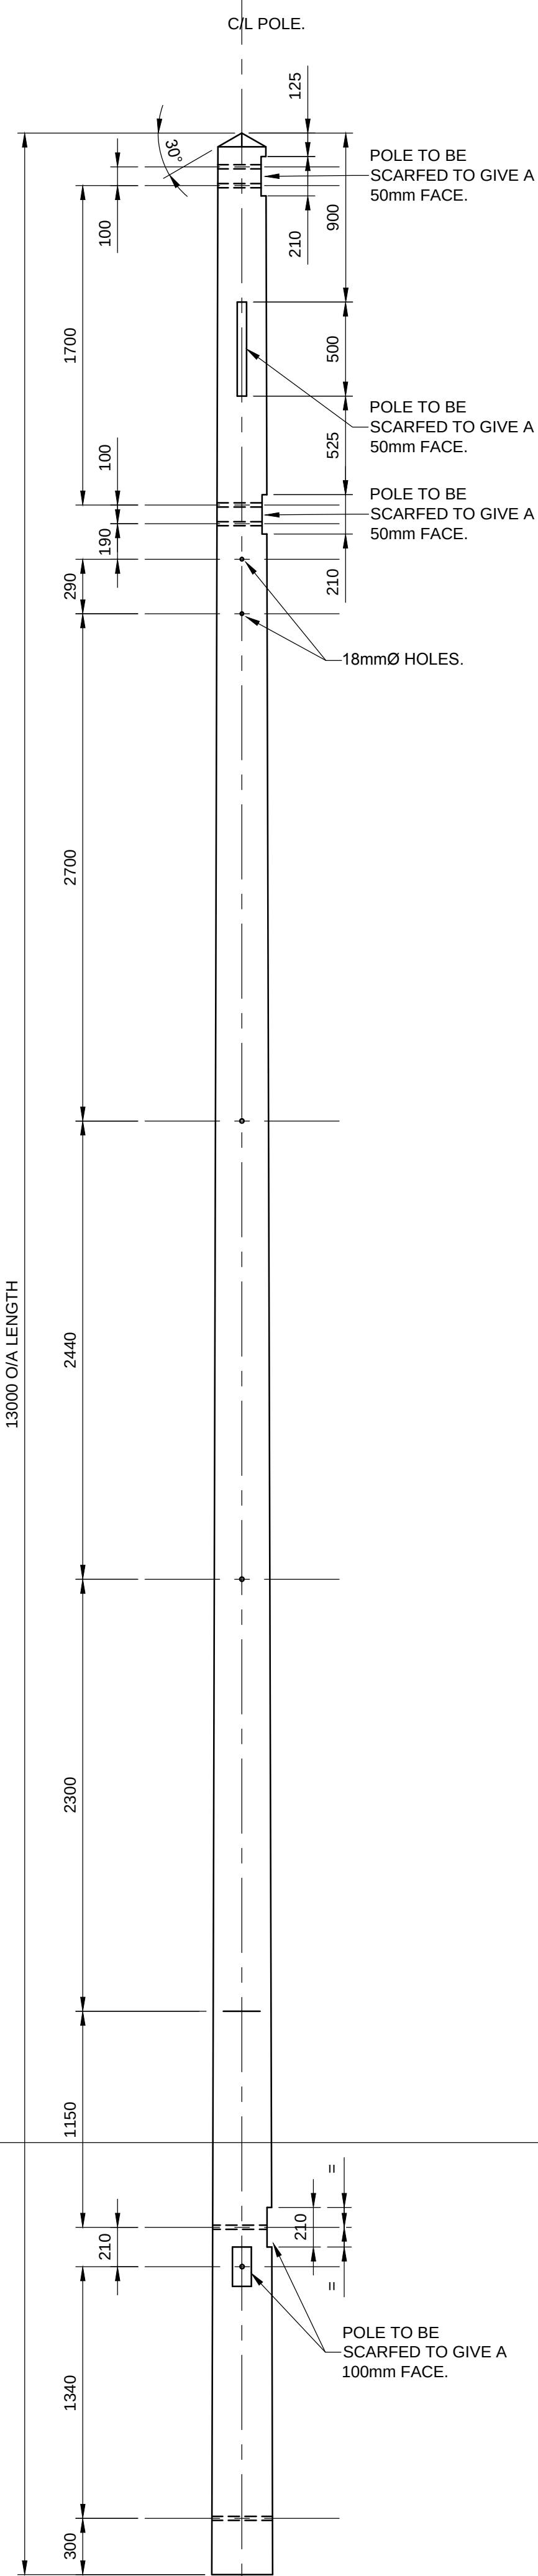

POLE 2 INFORMATION

POLE GRADE - MEDIUM.
POLE LENGTH - 13.0m.
POLE DIAMETER - 260mm*.


*FROM 1.5m OF BUTT END.

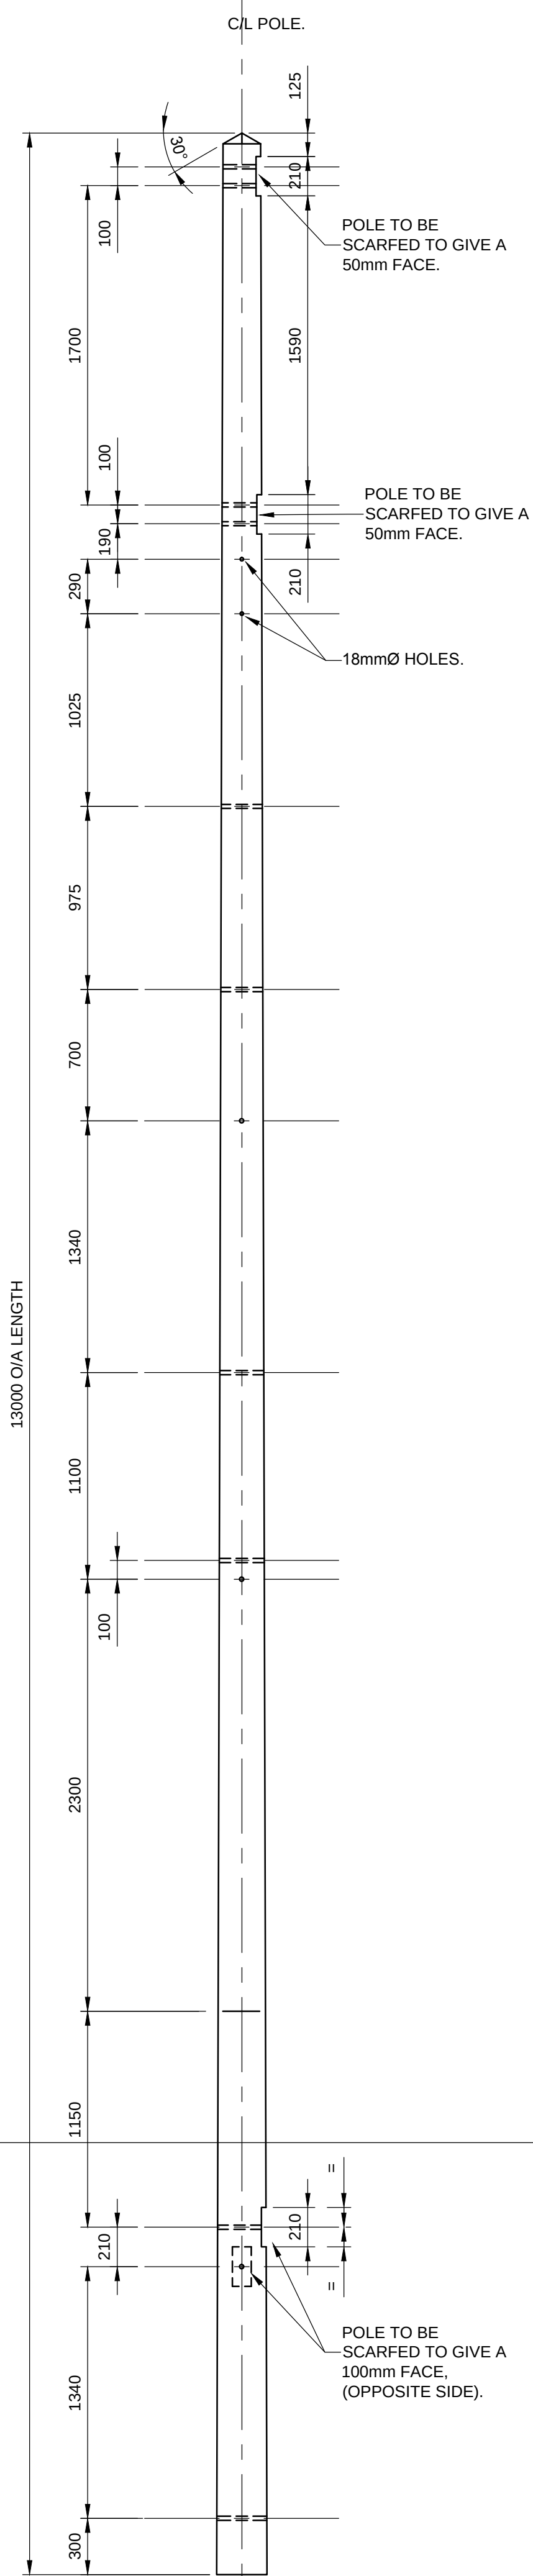

POLE 3 INFORMATION

POLE GRADE - STOUT.
POLE LENGTH - 13.0m.
POLE DIAMETER - 320mm*.


*FROM 1.5m OF BUTT END.

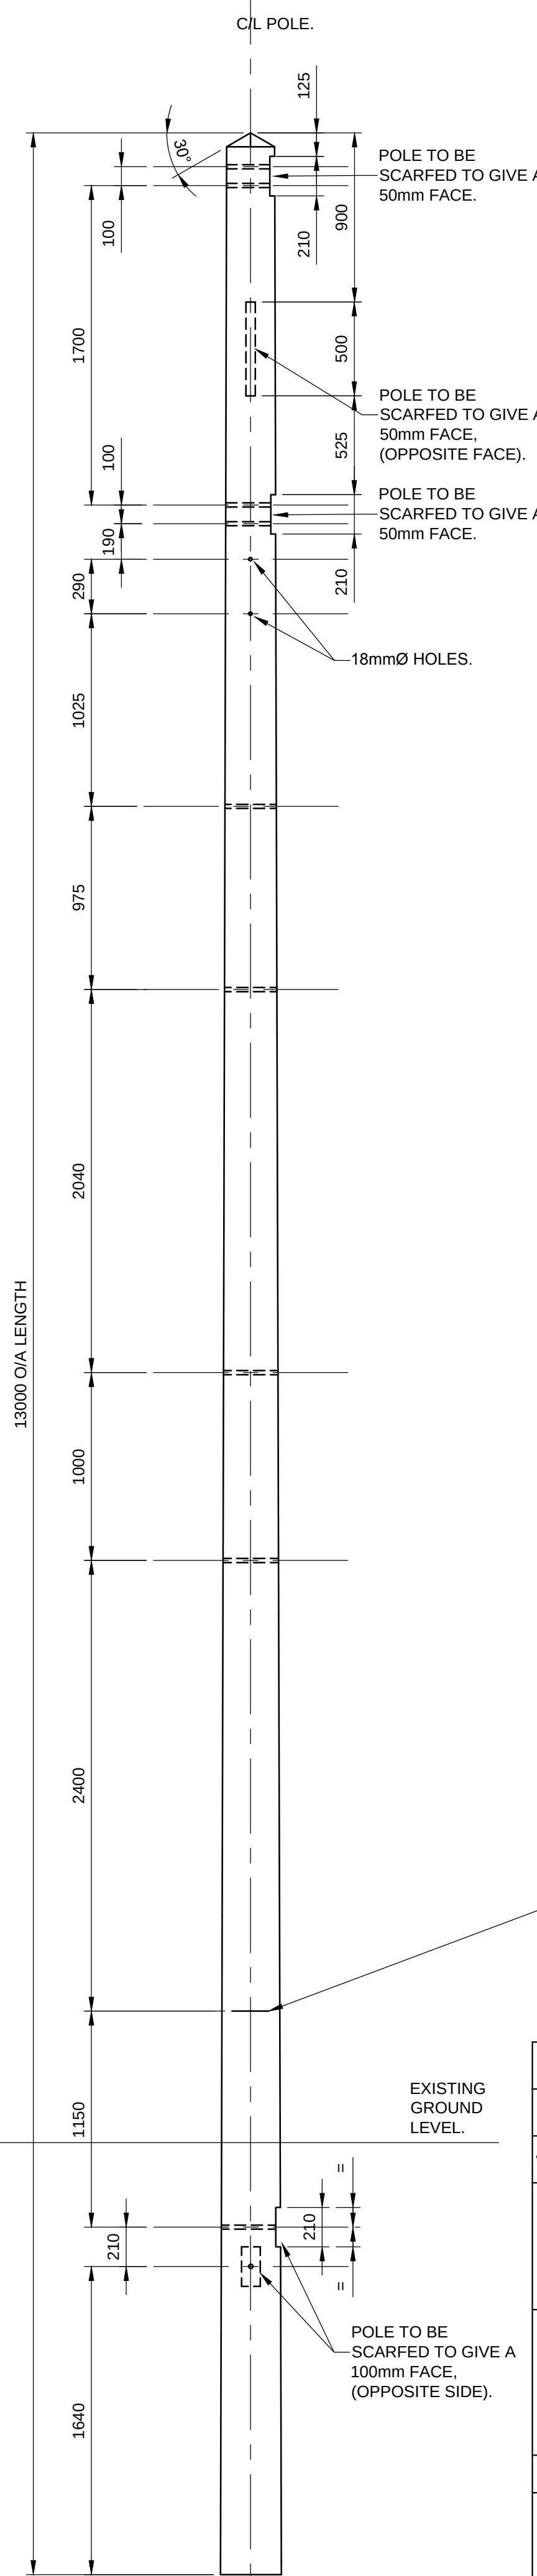

DRILLING & MARKINGS NOTES.

1. ALL HOLES TO BE 22mm DIAMETER UNLESS OTHERWISE STATED.
2. BUTT TO BE SAWN-OFF SQUARE TO THE AXIS OF THE POLE.
3. POLE TO BE MARKED AS BELOW.
4. IT IS ESSENTIAL THAT THE DRILLINGS ARE DRILLED TO TEMPLATE, ARE ACCURATE AND DEAD CENTRE. ANY INCONSISTENCIES TO BE INDICATED TO UK POWER NETWORKS AS SOON AS POSSIBLE.
5. THE FOLLOWING INFORMATION IS TO BE IMPRESSED ON THE END GRAIN OF THE BUTT:
(i) LENGTH AND DIAMETER OF THE POLE.
(ii) POLE NUMBER IN ACCORDANCE WITH SCHEDULE).

NOTE! THE PERSONAL MARK OF THE POLE INSPECTOR WILL BE IMPRESSED ON THE BUTT.

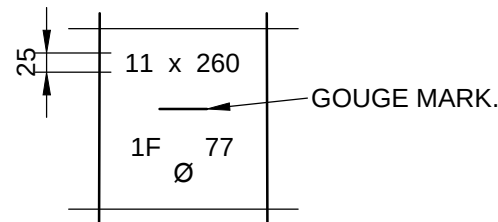

- 11 LENGTH OF POLE IN METRES.
- 260 DIAMETER OF POLE IN MILLIMETRES AT 1.5m FROM THE BUTT.
- 1F SPECIES CODE.
- 77 YEAR OF IMPREGNATION.
- Ø NAME OR MARK OF CREOSOTING FIRM.

B	17.01.14	ADDITIONAL DIMENSIONS ADDED TO POLES 2 & 3	JA
A	19.12.13	ISSUED FOR COMMENT.	JA
Version	Date	DESCRIPTION	Designed Drawn
33kV POINT OF CONNECTION AT POLE NUMBER 90A POLE FABRICATION DRAWING			
SCALE	1:25	@ A1	TENDER
DRAWING NO.	HQ-2000-4720	Version	B
STD	DRAPERS SOLAR FARM		