


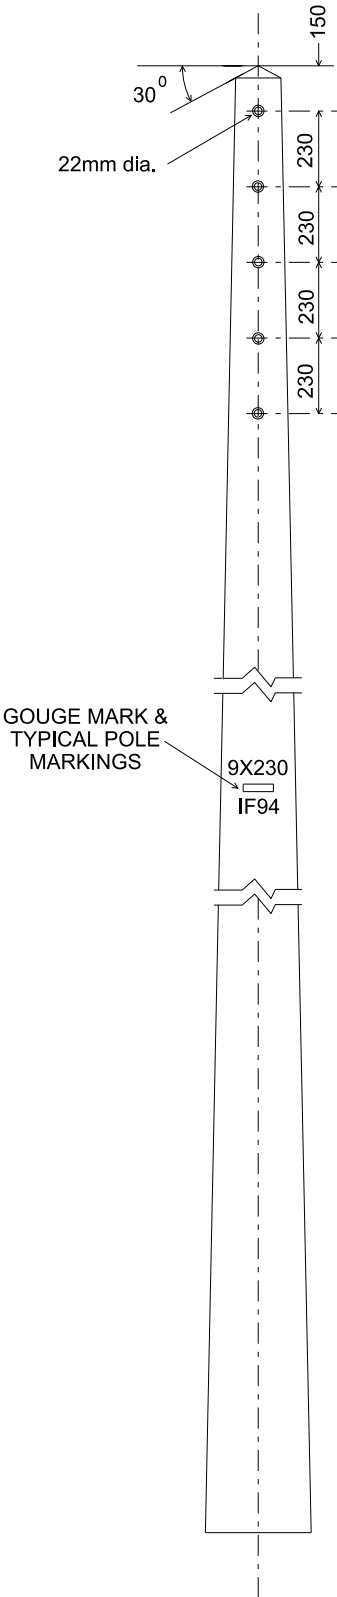

NOTES

- 1. ALL HOLES SHALL BE 18 mm DIA. WITH THE EXCEPTION OF THE TOP WHICH WILL BE 22 mm DIA.
- 2. HOLES SHALL BE DRILLED TO TEMPLATE, ACCURATE AND DEAD CENTRE.

All dimensions in millimetres

Intermediate Pole LV Lines & Services	© UK Power Networks 2020		
	DRN. June 1994	DRAWING NUMBER	ISSUE
	CKD. January 2014	ETS 01-0200.01	1
	APP.		