


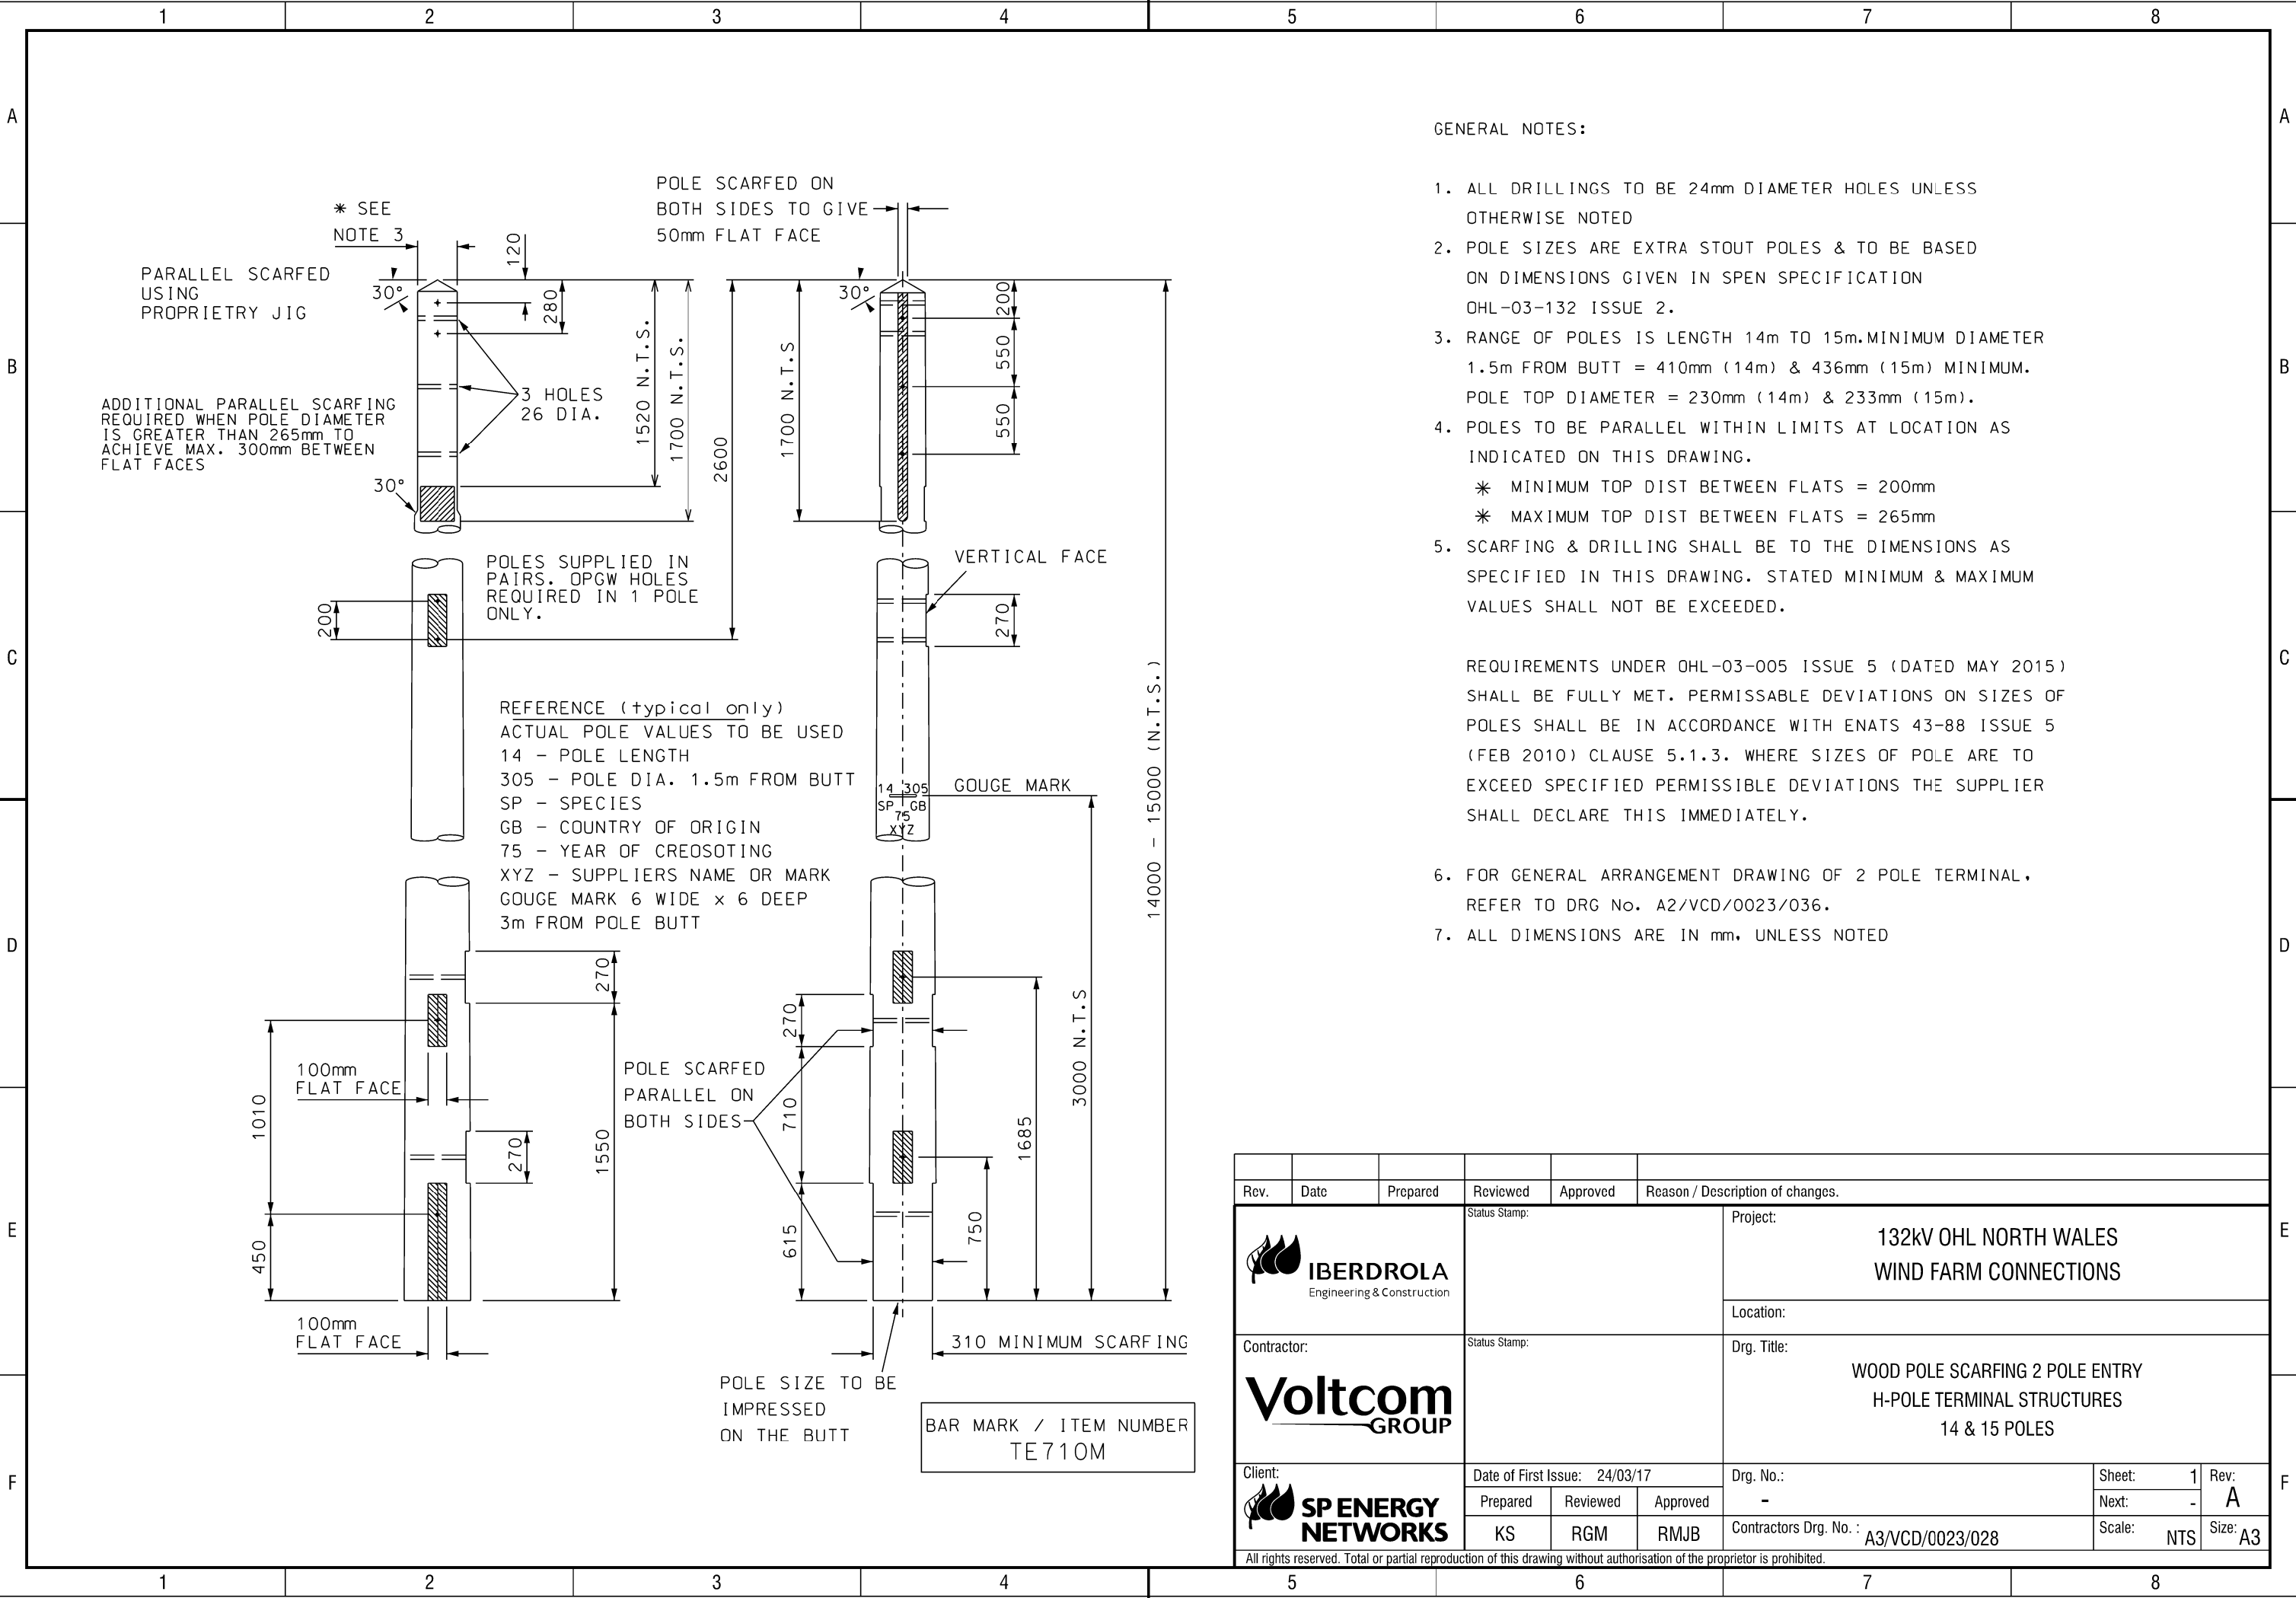

Rev.	Date	Prepared	Reviewed	Approved	Reason / Description of changes.					
			Status Stamp:			Project: 132kV OHL NORTH WALES WIND FARM CONNECTIONS				
						Location:				
			Status Stamp:			Drg. Title: WOOD POLE SCARFING 2 POLE ENTRY H-POLE TERMINAL STRUCTURES 14 & 15 POLES				
			Date of First Issue: 24/03/17			Drg. No.: -		Sheet:	1	Rev: A
			Prepared	Reviewed	Approved			Next:	-	
			KS	RGM	RMJB	Contractors Drg. No. : A3/VCD/0023/028		Scale:	NTS	Size:
All rights reserved. Total or partial reproduction of this drawing without authorisation of the proprietor is prohibited.										

All rights reserved. Total or partial reproduction of this drawing without authorisation of the proprietor is prohibited.