


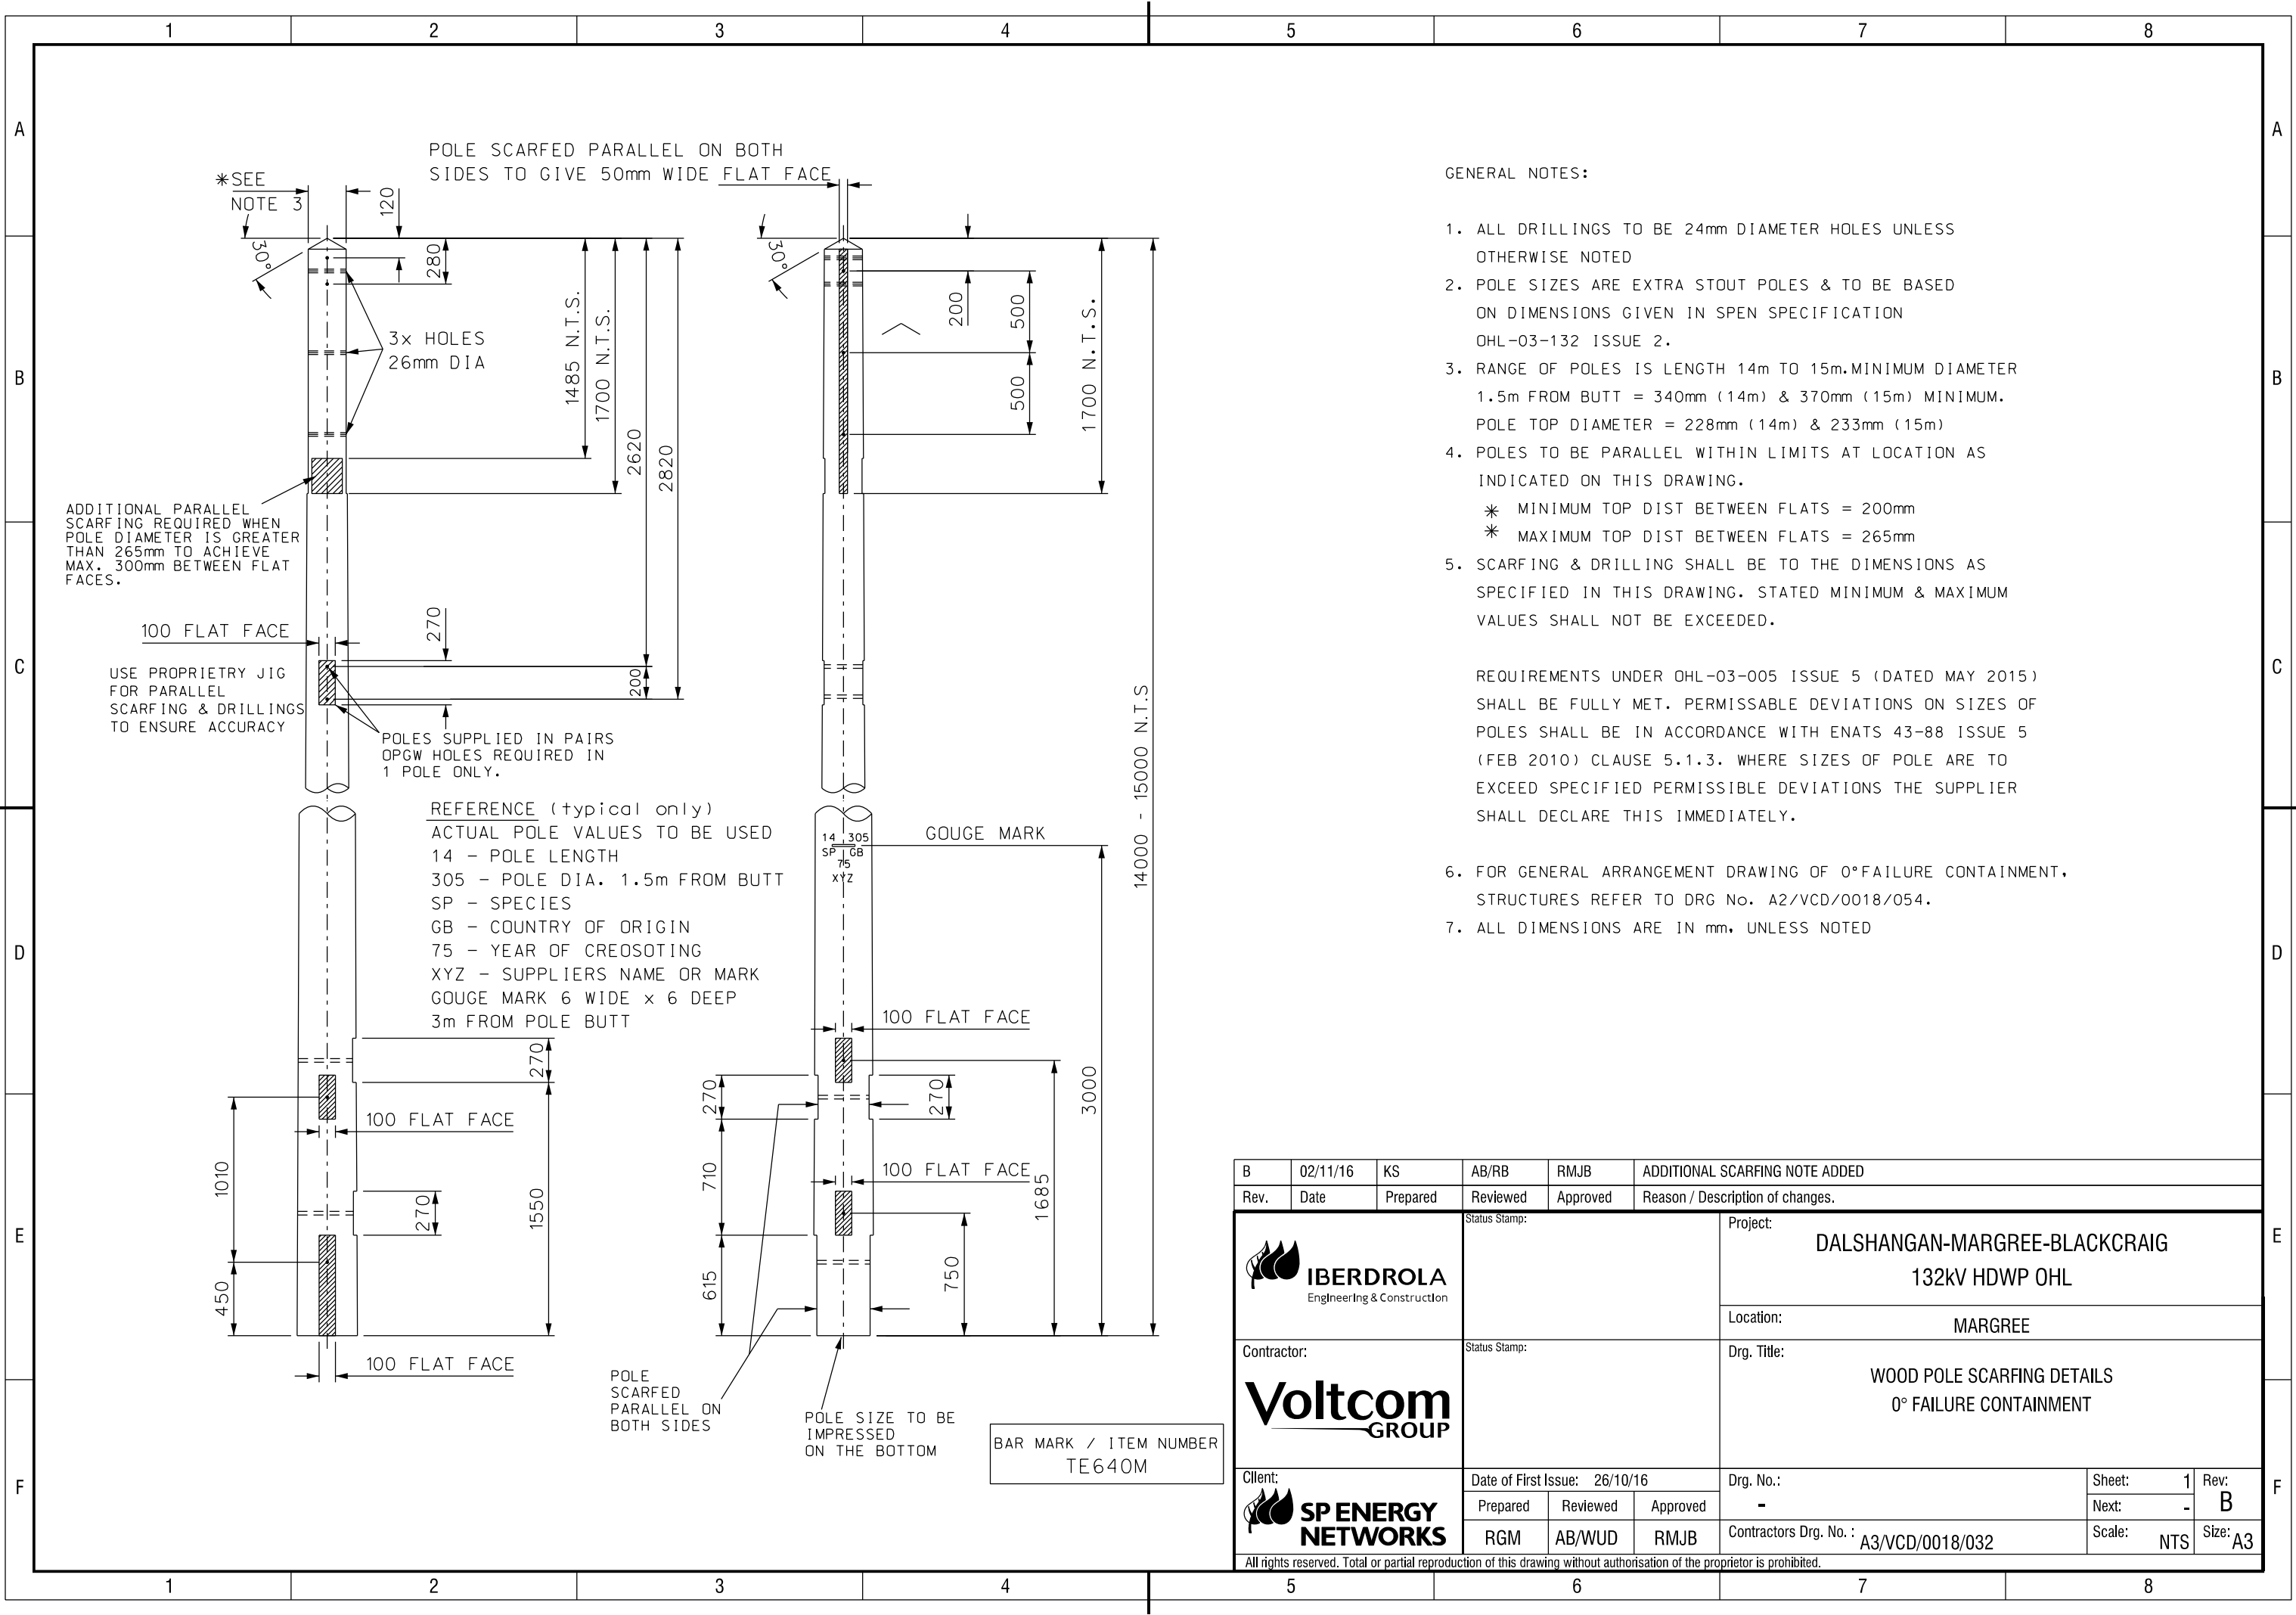

B	02/11/16	KS	AB/RB	RMJB	ADDITIONAL SCARFING NOTE ADDED	
Rev.	Date	Prepared	Reviewed	Approved	Reason / Description of changes.	
			Status Stamp:		Project: DALSHANGAN-MARGREE-BLACKCRAIG 132kV HDWP OHL	
Contractor: 			Status Stamp:		Location: MARGREE	
Client: 			Date of First Issue: 26/10/16		Drg. Title: WOOD POLE SCARFING DETAILS 0° FAILURE CONTAINMENT	
			Prepared	Reviewed	Approved	Drg. No.: -
			RGM	AB/WUD	RMJB	Contractors Drg. No.: A3/VCD/0018/032
						Sheet: 1 Next: - Scale: NTS
						Rev: B Size: A3

All rights reserved. Total or partial reproduction of this drawing without authorisation of the proprietor is prohibited.