

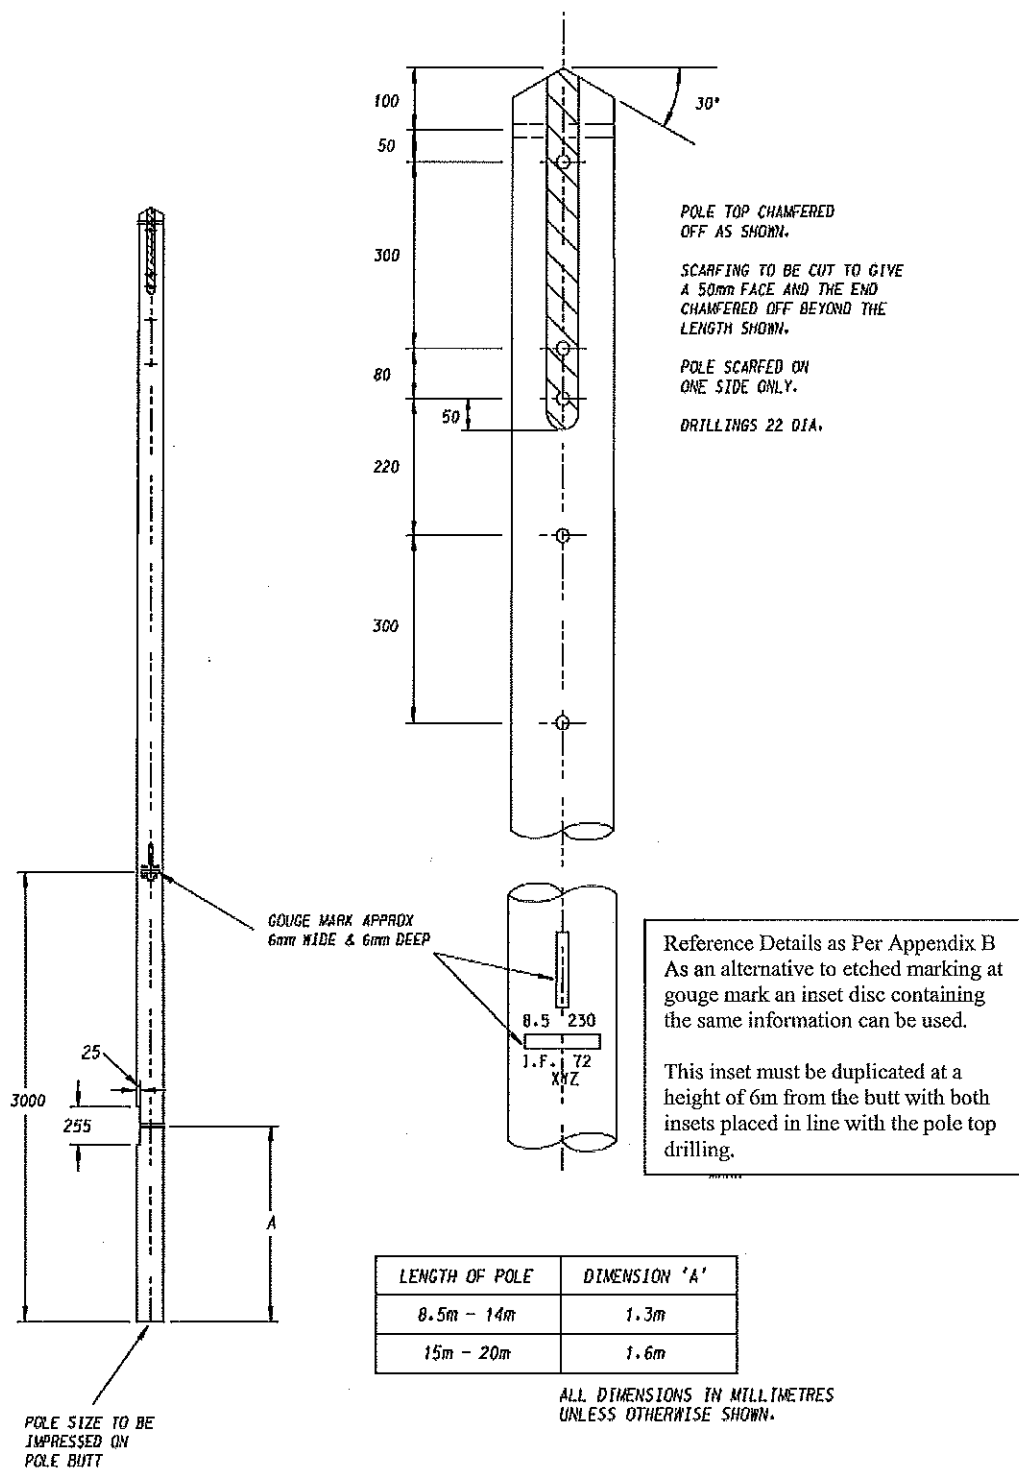


Fig 14 - Single Pole Drillings and Markings
(For LV Open Wire Lines to ESI 43-30, LV ABC to 43-12 & 11kV Light Construction)